



CORTE A-A'

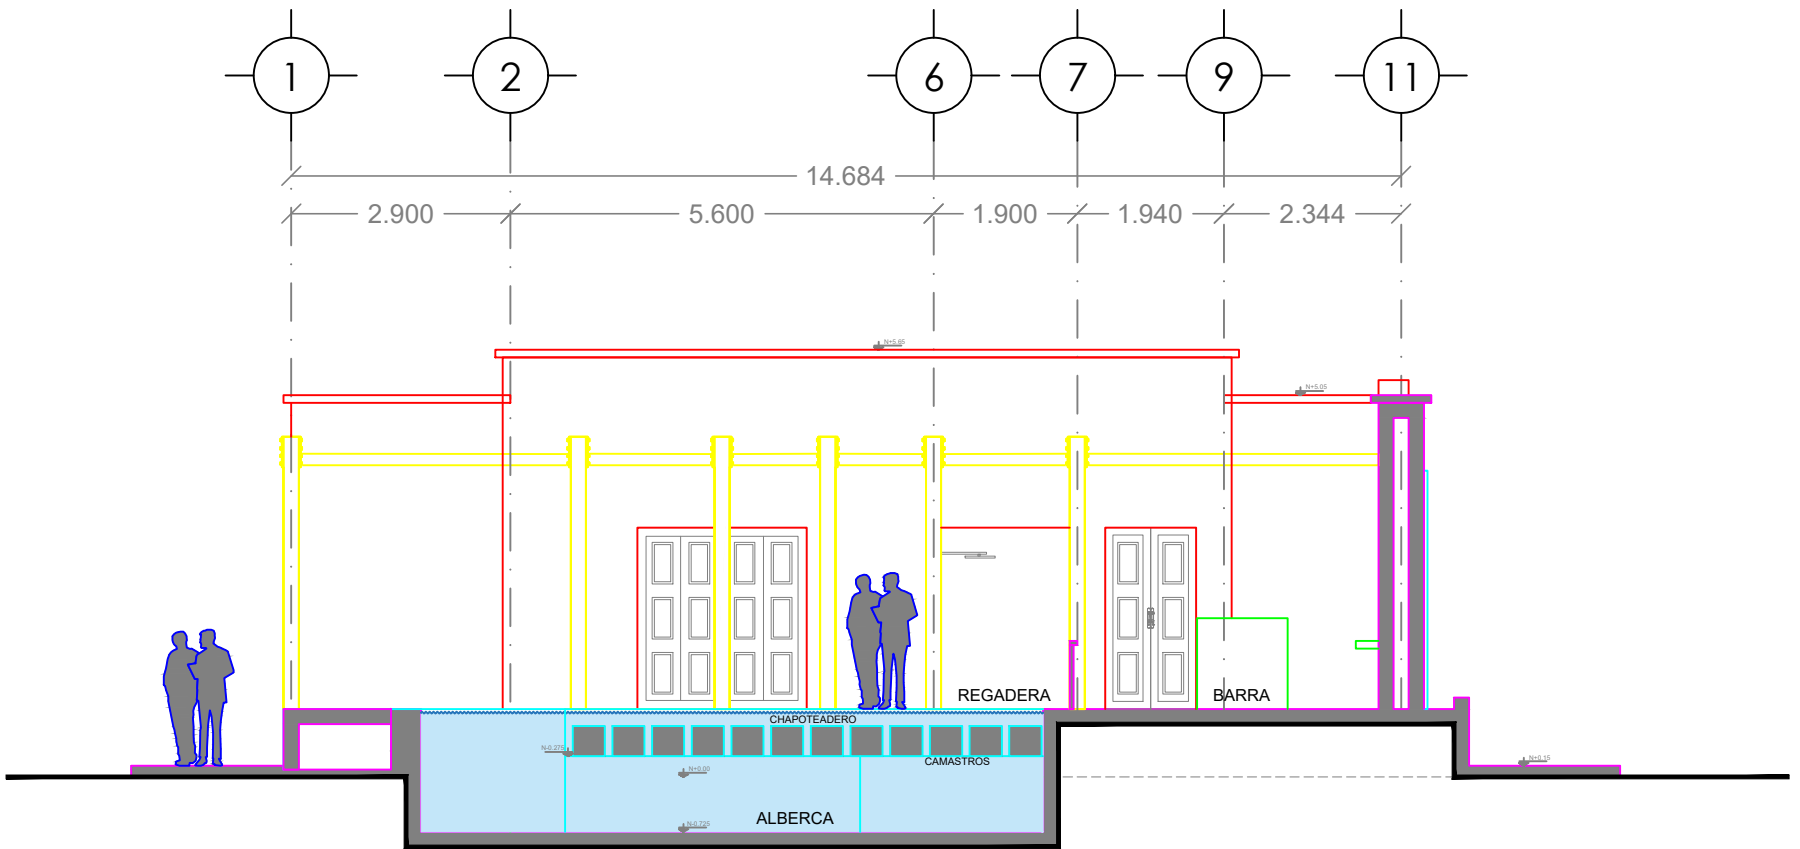

CORTE B-B'

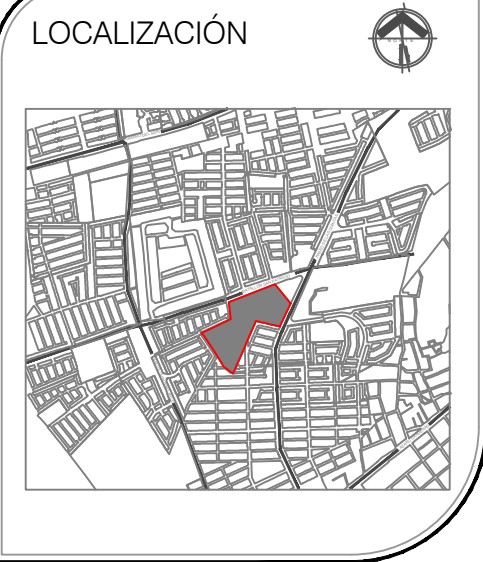

REVISIONES

--	--

NOTAS Y ESPECIFICACIONES

--

RESPONSABLES

RESPONSABLE DE DISEÑO ARQUITECTÓNICO:
ARO. FRANCISCA ELIZABETH FLORES GARCIA
PROPIETARIO:
R.L. ING. ADRIAN CASTRO GUERRERO
DIRECTOR RESPONSABLE DE OBRA:
ING. RAFAEL MONDRAGON GARCIA

PROPIETARIO:	
DESARROLLOS RESIDENCIALES LANDER S. A. DE C. V.	
Bulevard Naimari #1116 + Jalisco y Sufragio CD. OBREGÓN, SONORA. TEL. 413 52 79 413 52 80 413 52 83	
ESCALA:	VERSIÓN:
Esc: 1:100	2.0
DIBUJO: ARQ. GUADALUPE VAZQUEZ	FECHA: NOV/2025
REVISO: ARQ. ELIZABETH FLORES	ACOTACIONES: METROS

PROYECTO:

CASA CLUB

UBICACIÓN:

MAR DE PLATA HERMOSILLO, SONORA

CONTENIDO:

CORTES

PLANO No:

ARQ - 04

ARCHIVO: 01.ARQ-CC-MDP NORTE V.03.dwg

ESC 1:100