



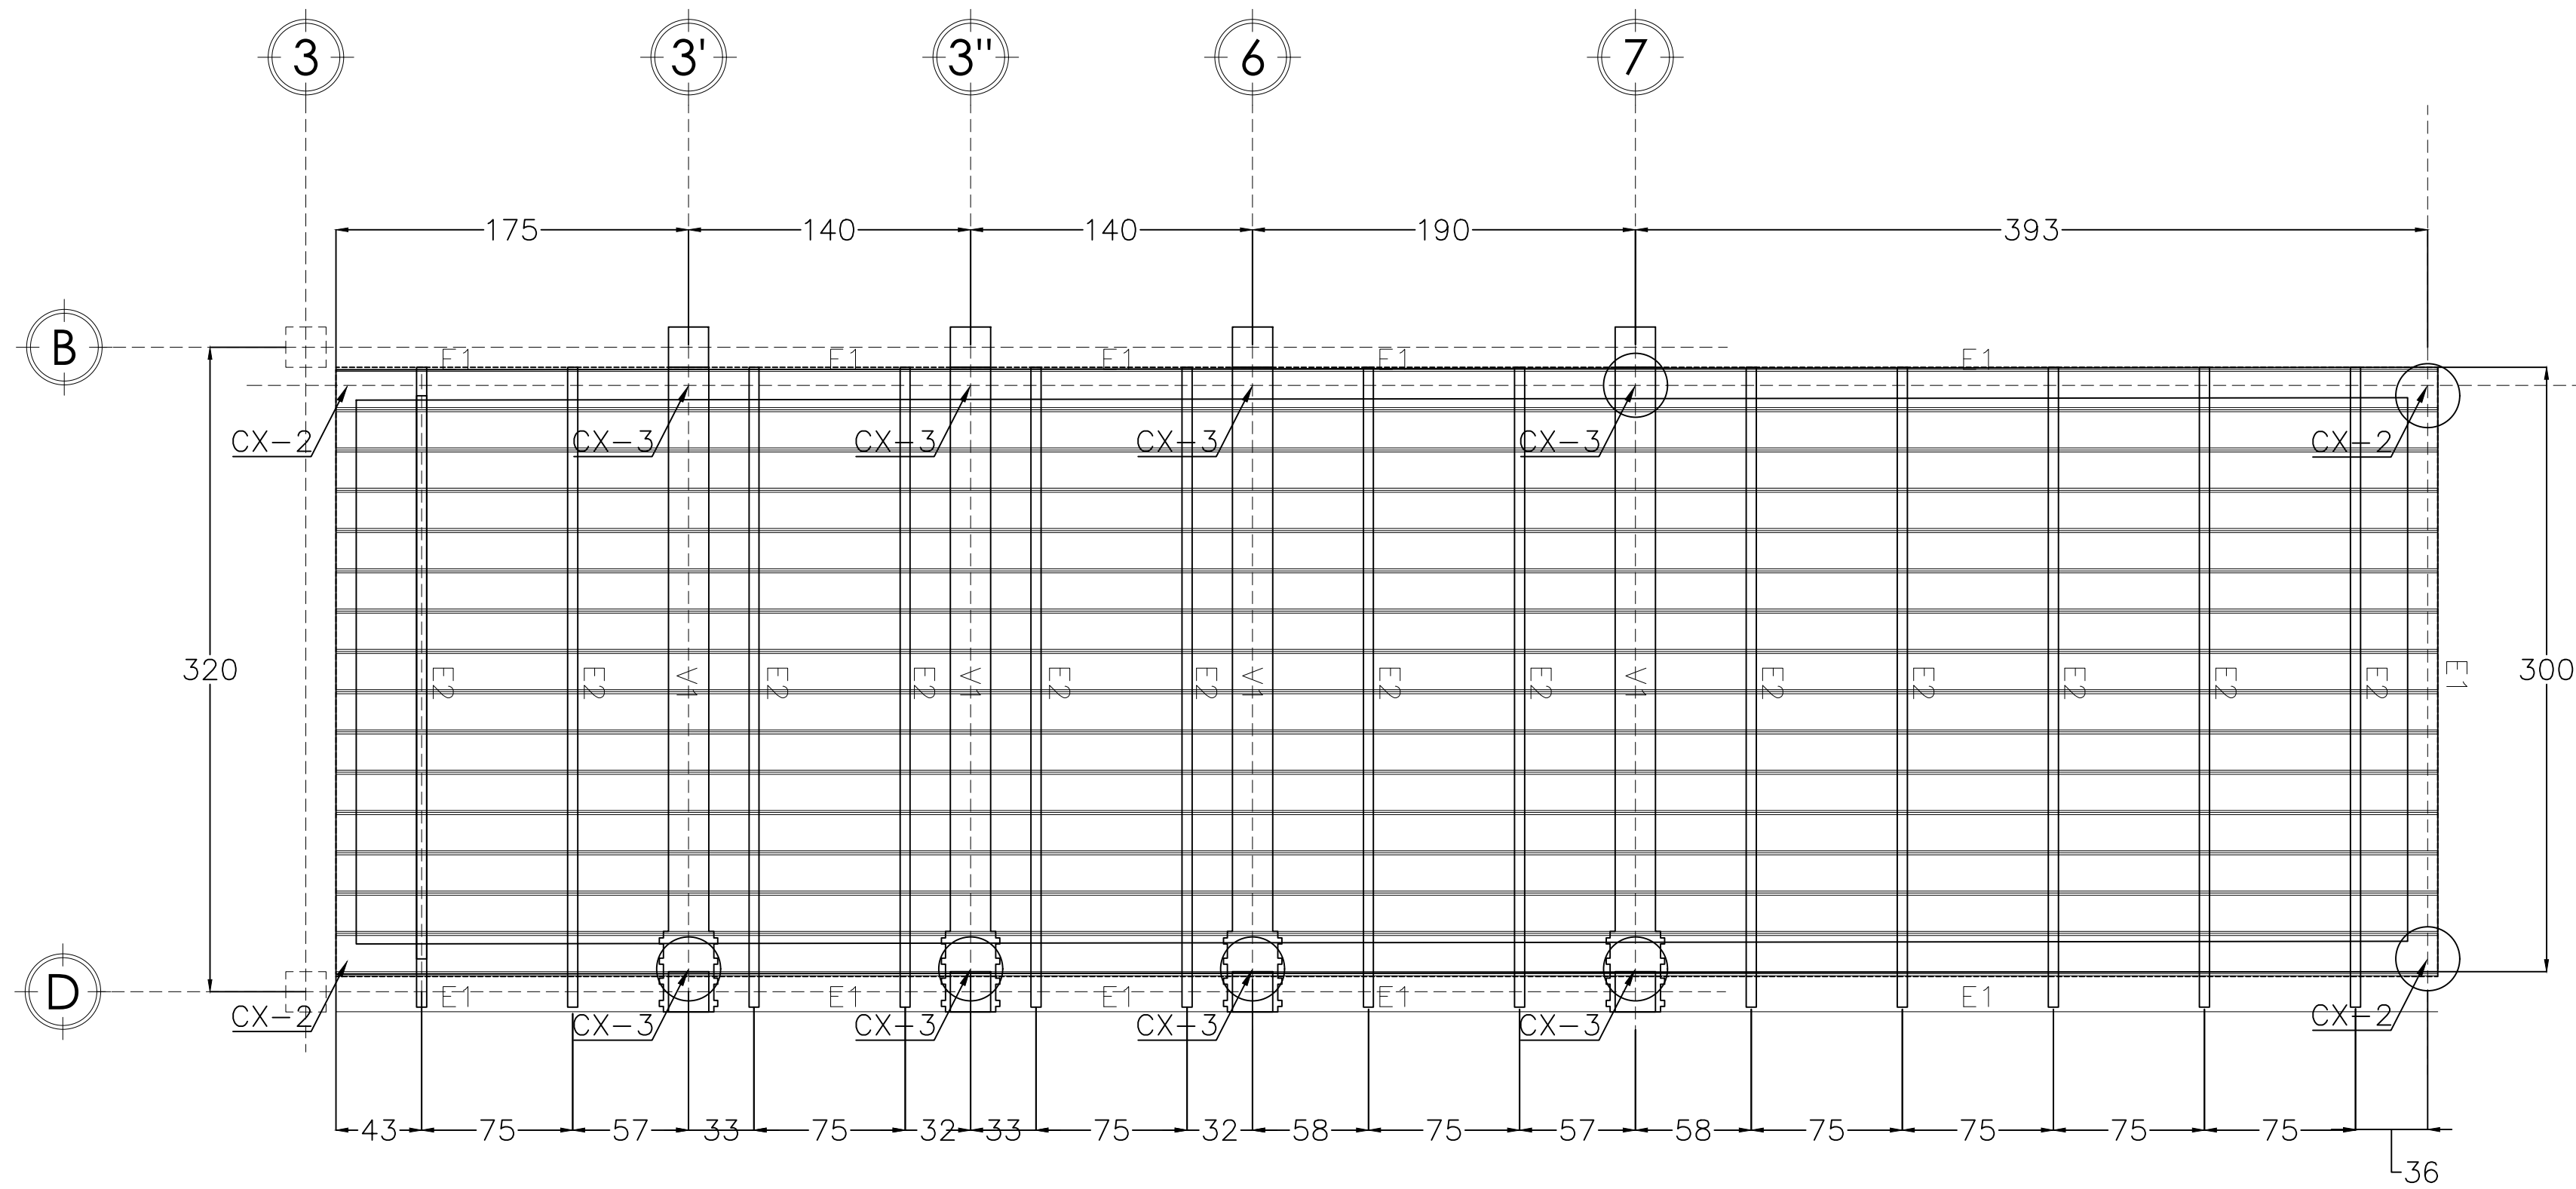


PLANTA DE CUBIERTA METÁLICA 1

Acot: mm

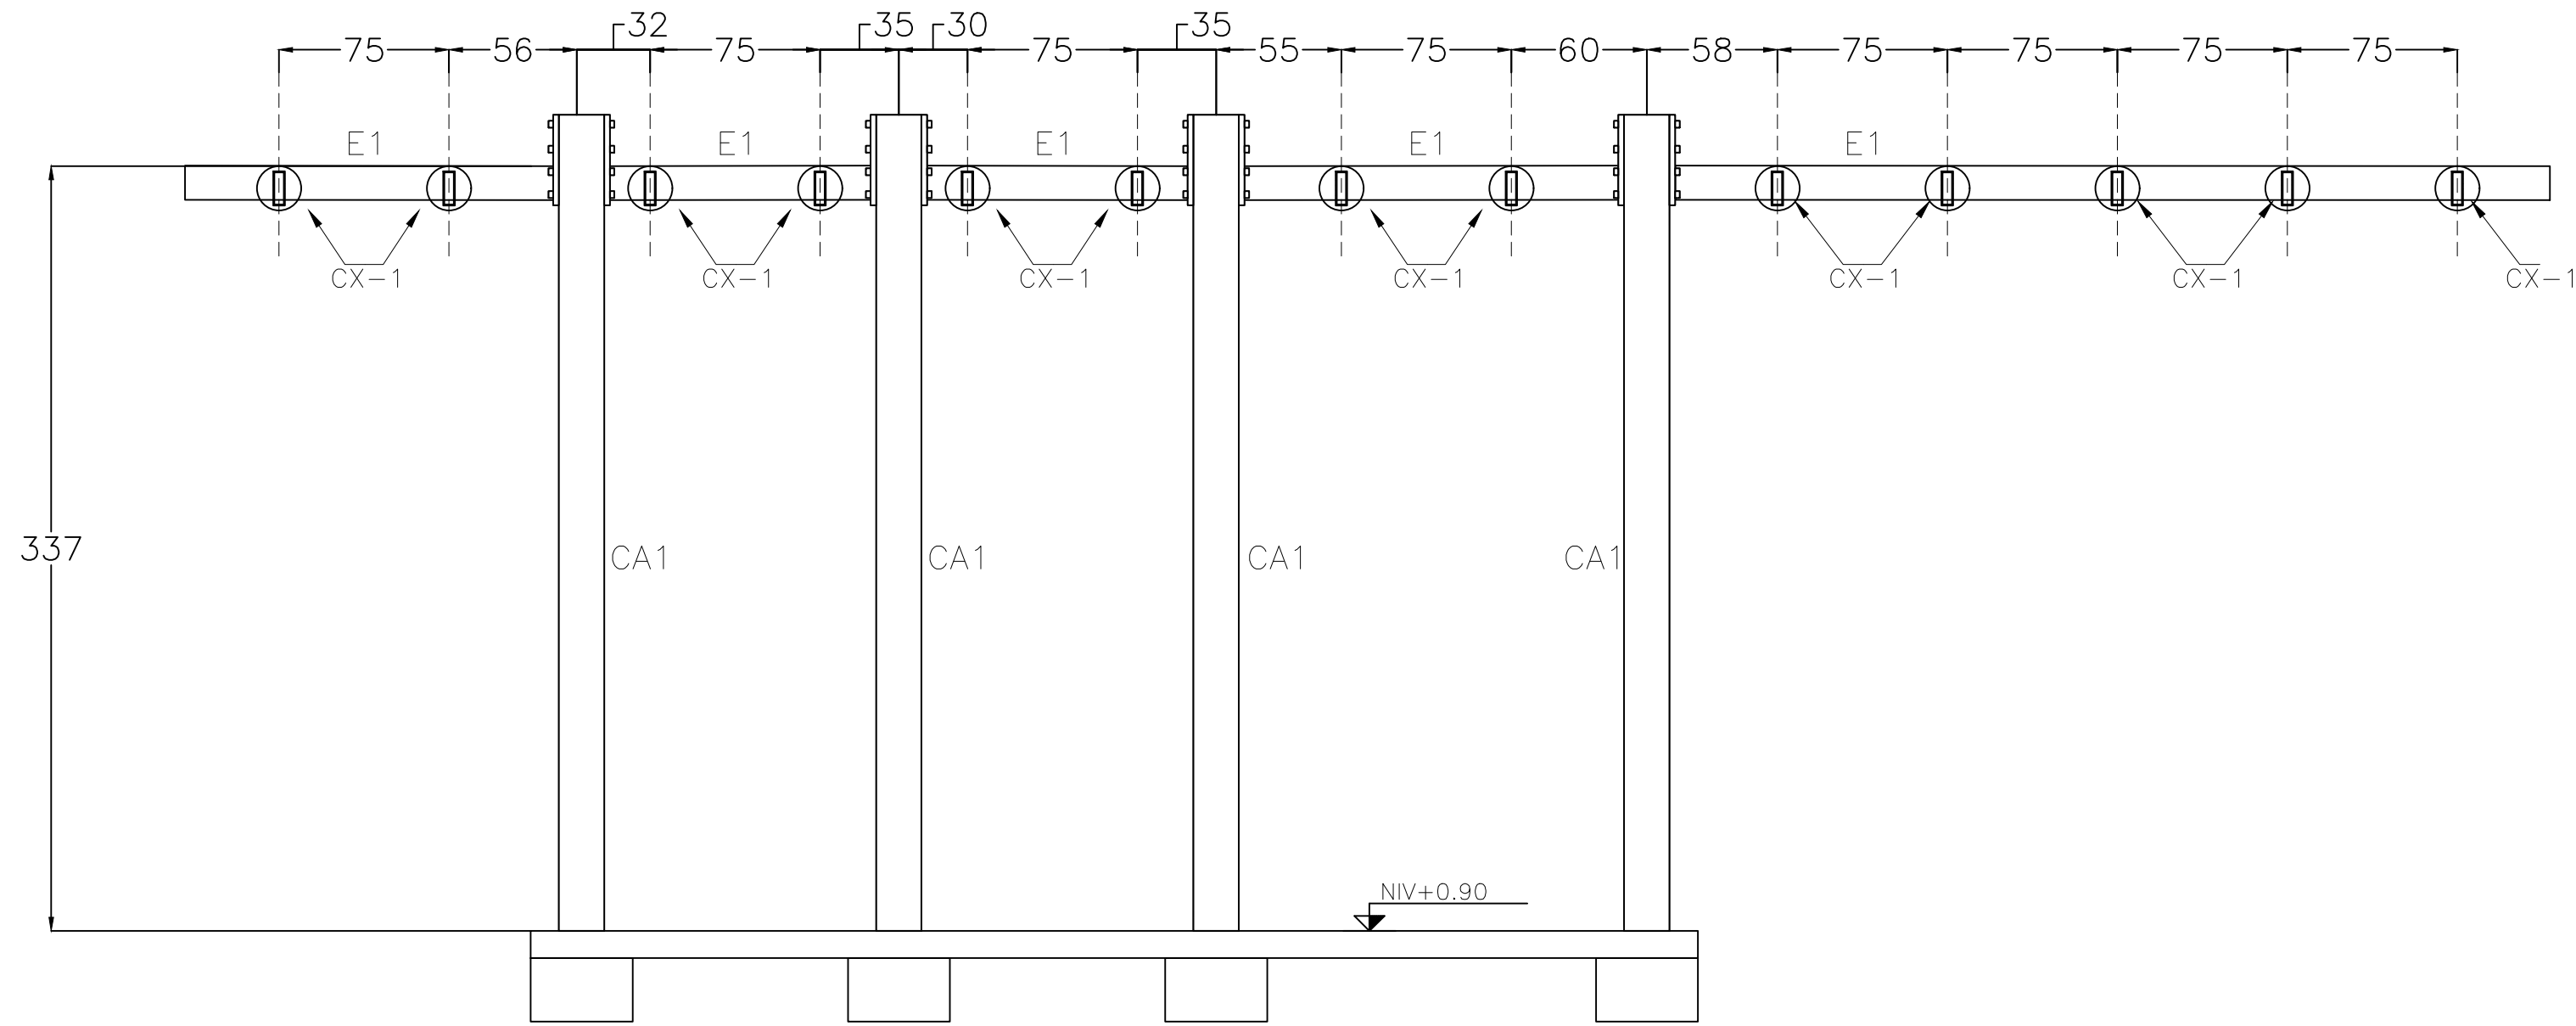

MARCO LONGITUDINAL CUBIERTA 1

Acot: mm

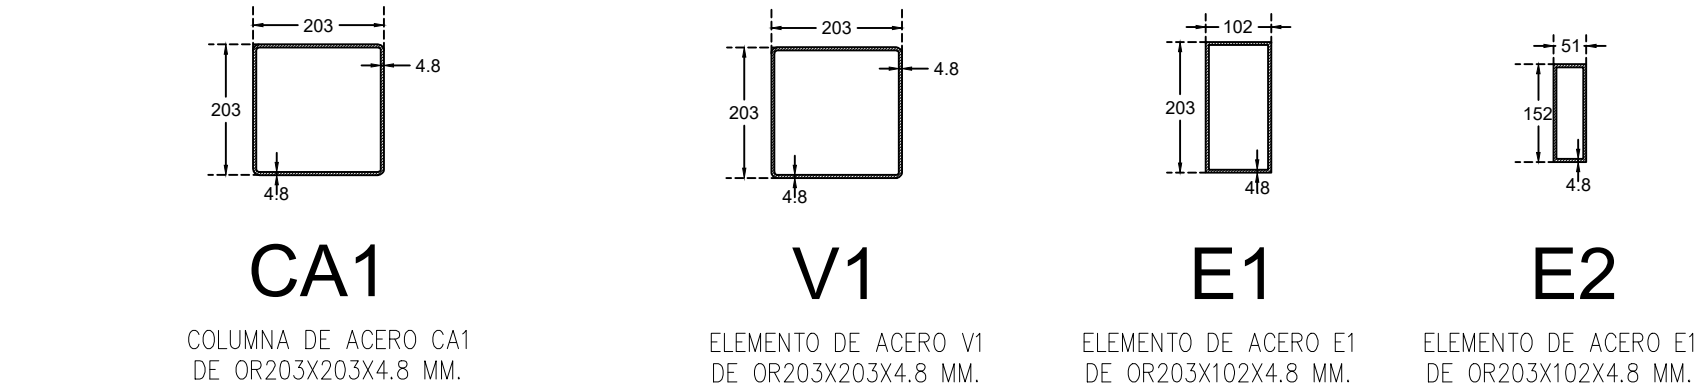


DETALLE COLUMNA CA1

Acot: mm


DETALLE ELEMENTOS CUBIERTA

Acot: mm

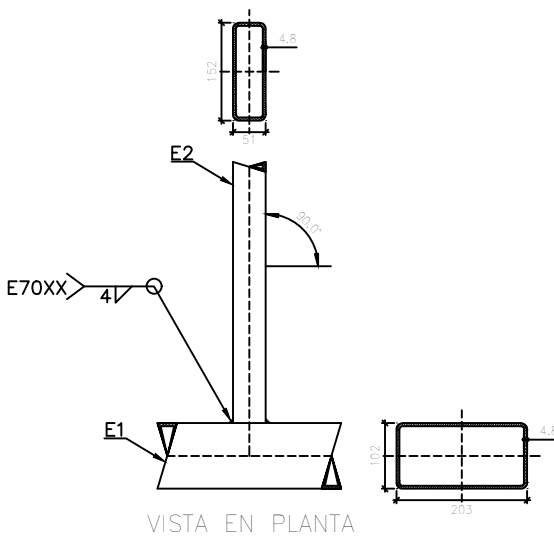


DETALLE CX-1

Acot: mm

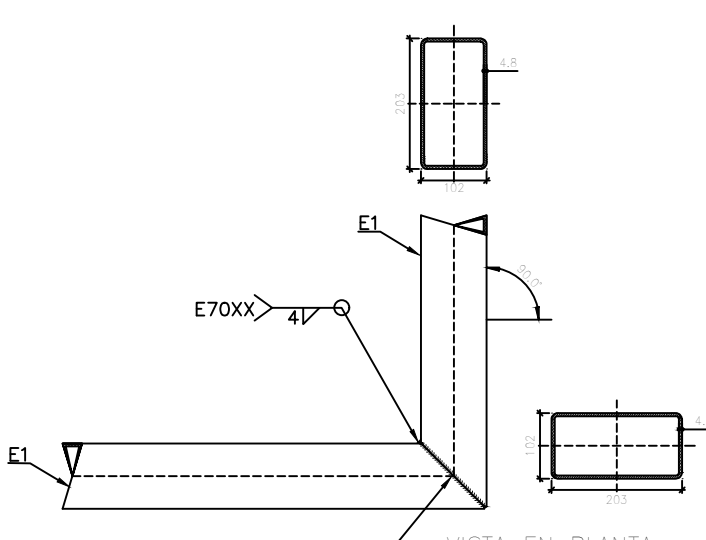


DETALLE CX-2

Acot: mm

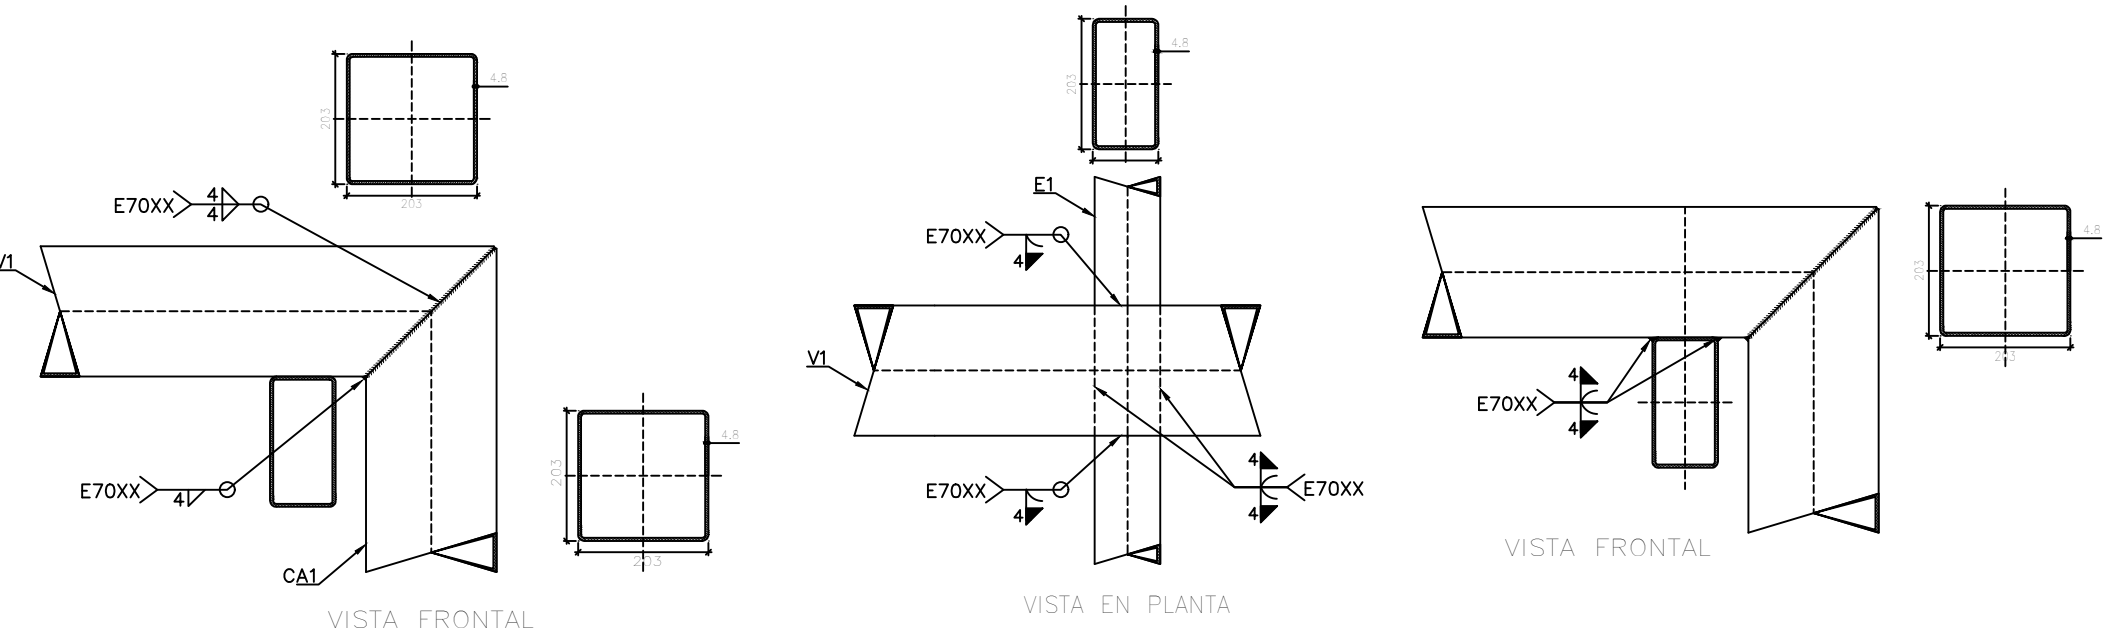


DETALLE CONEXION TIPO CX-3

Acot: mm

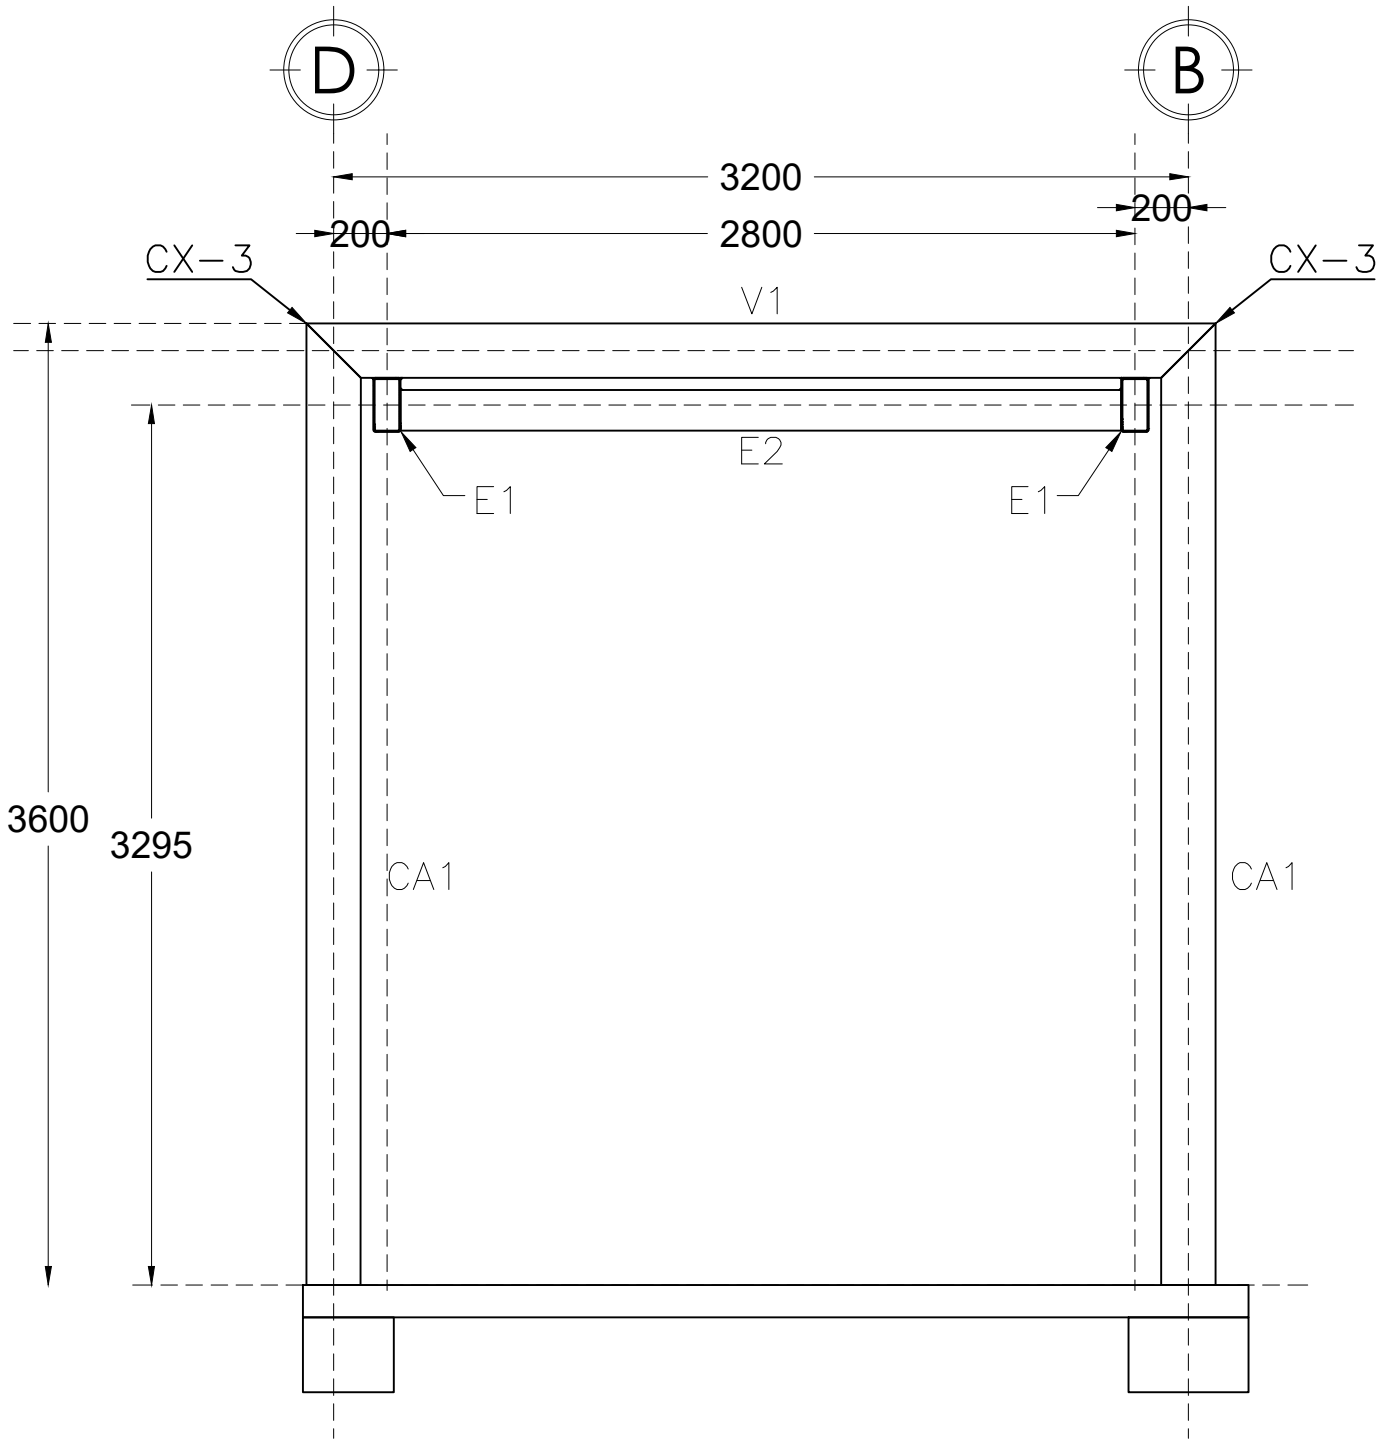

MARCO TRANSVERSAL CUBIERTA 1

Acot: mm

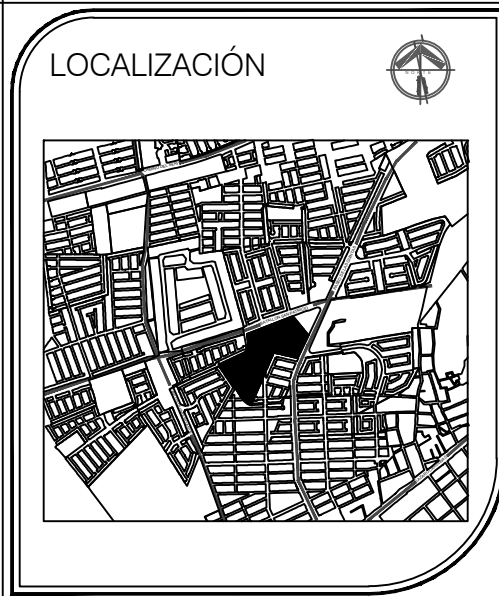

REVISIONES

NOTAS Y ESPECIFICACIONES

RESPONSABLES

RESPONSABLE DE DISEÑO ARQUITECTÓNICO:
ARQ. FRANCISCA ELIZABETH FLORES GARCIA
PROPIETARIO:
R.L. ING. ADRIAN CASTRO GUERRERO
DIRECTOR RESPONSABLE DE OBRA:
ING. RAFAEL MONDRAGON GARCIA

PROPIETARIO:
DESARROLLOS RESIDENCIALES
LANDER S. A. DE C. V.
Bulevard Naiman #1116 - Jalisco y Sultagio
CD. OREGON, SONORA
TEL. 413 52 79 413 52 80 413 52 83 fax 413 52 82
ESCALA:
Esc: 1:50
DIBUJO:
E.F.G.
REVISO:
ARQ.
ELIZABETH FLORES
REGION:
1.0
FECHA:
FEB/2026
ACOTACIONES:
METROS

PROYECTO:
CASA CLUB MDP NORTE

UBICACION:
MAR DE PLATA
HERMOSILLO, SONORA

CONTENIDO:
ESTRUCTURAL DE
CUBIERTA METÁLICA 1

PLANO No:
EST - 02

ARCHIVO: 03- ESTRUCTURAL CASA CLUB MDP NORTE 260223.dwg