



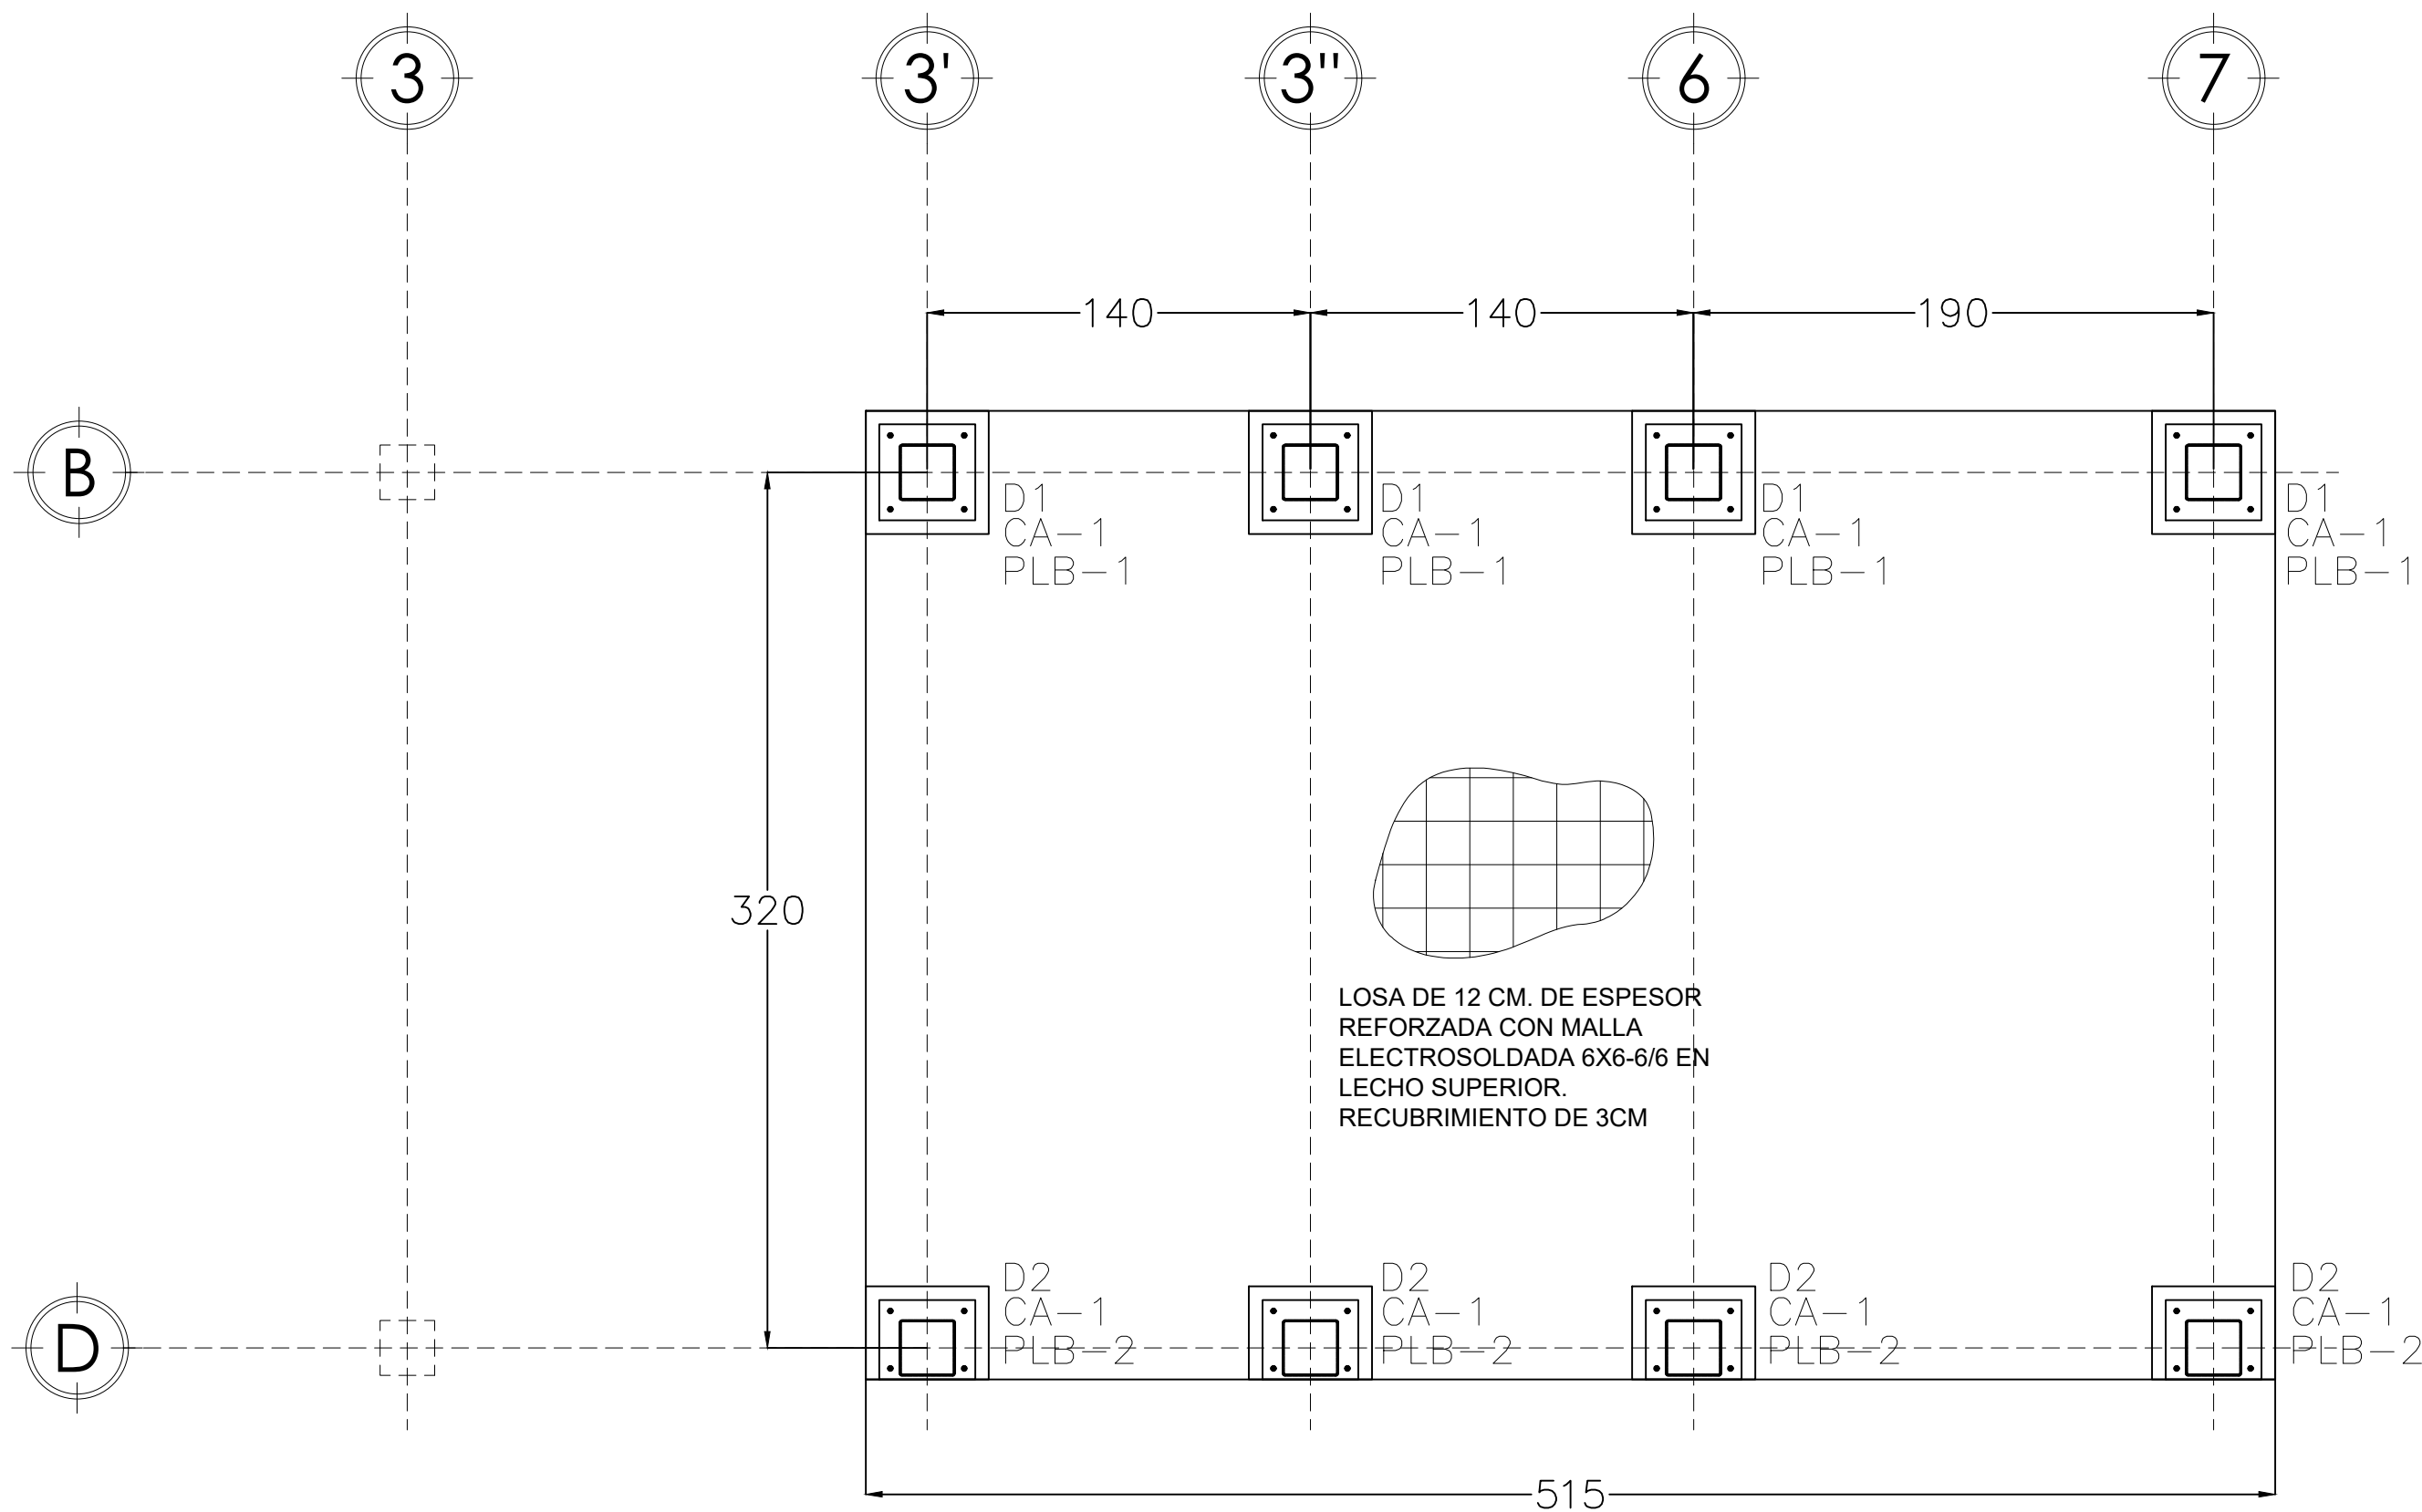


LOSA DE CIMENTACIÓN 1

Acot: mm

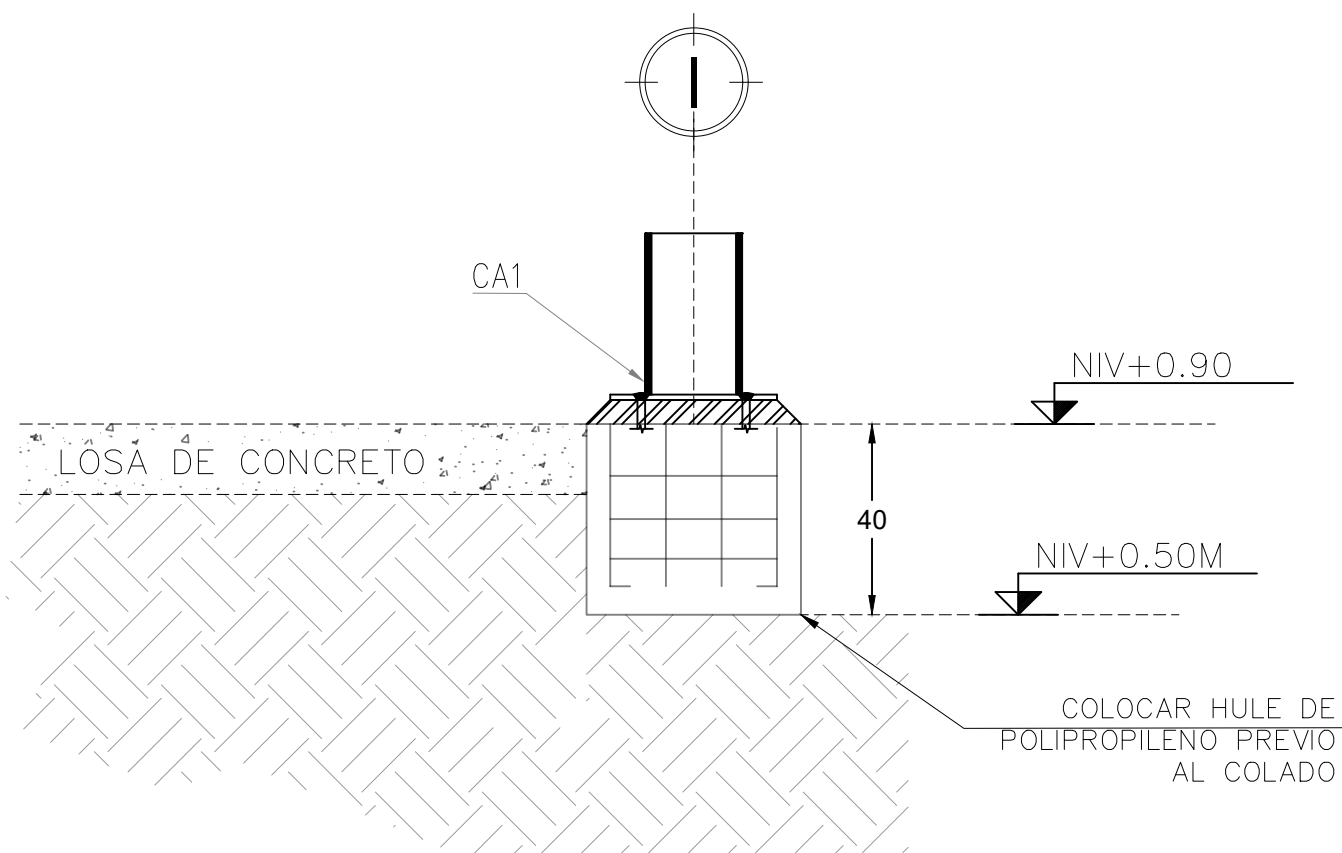


DETALLE - CONEXIÓN COLUMNA ALZADO

Acot: cm

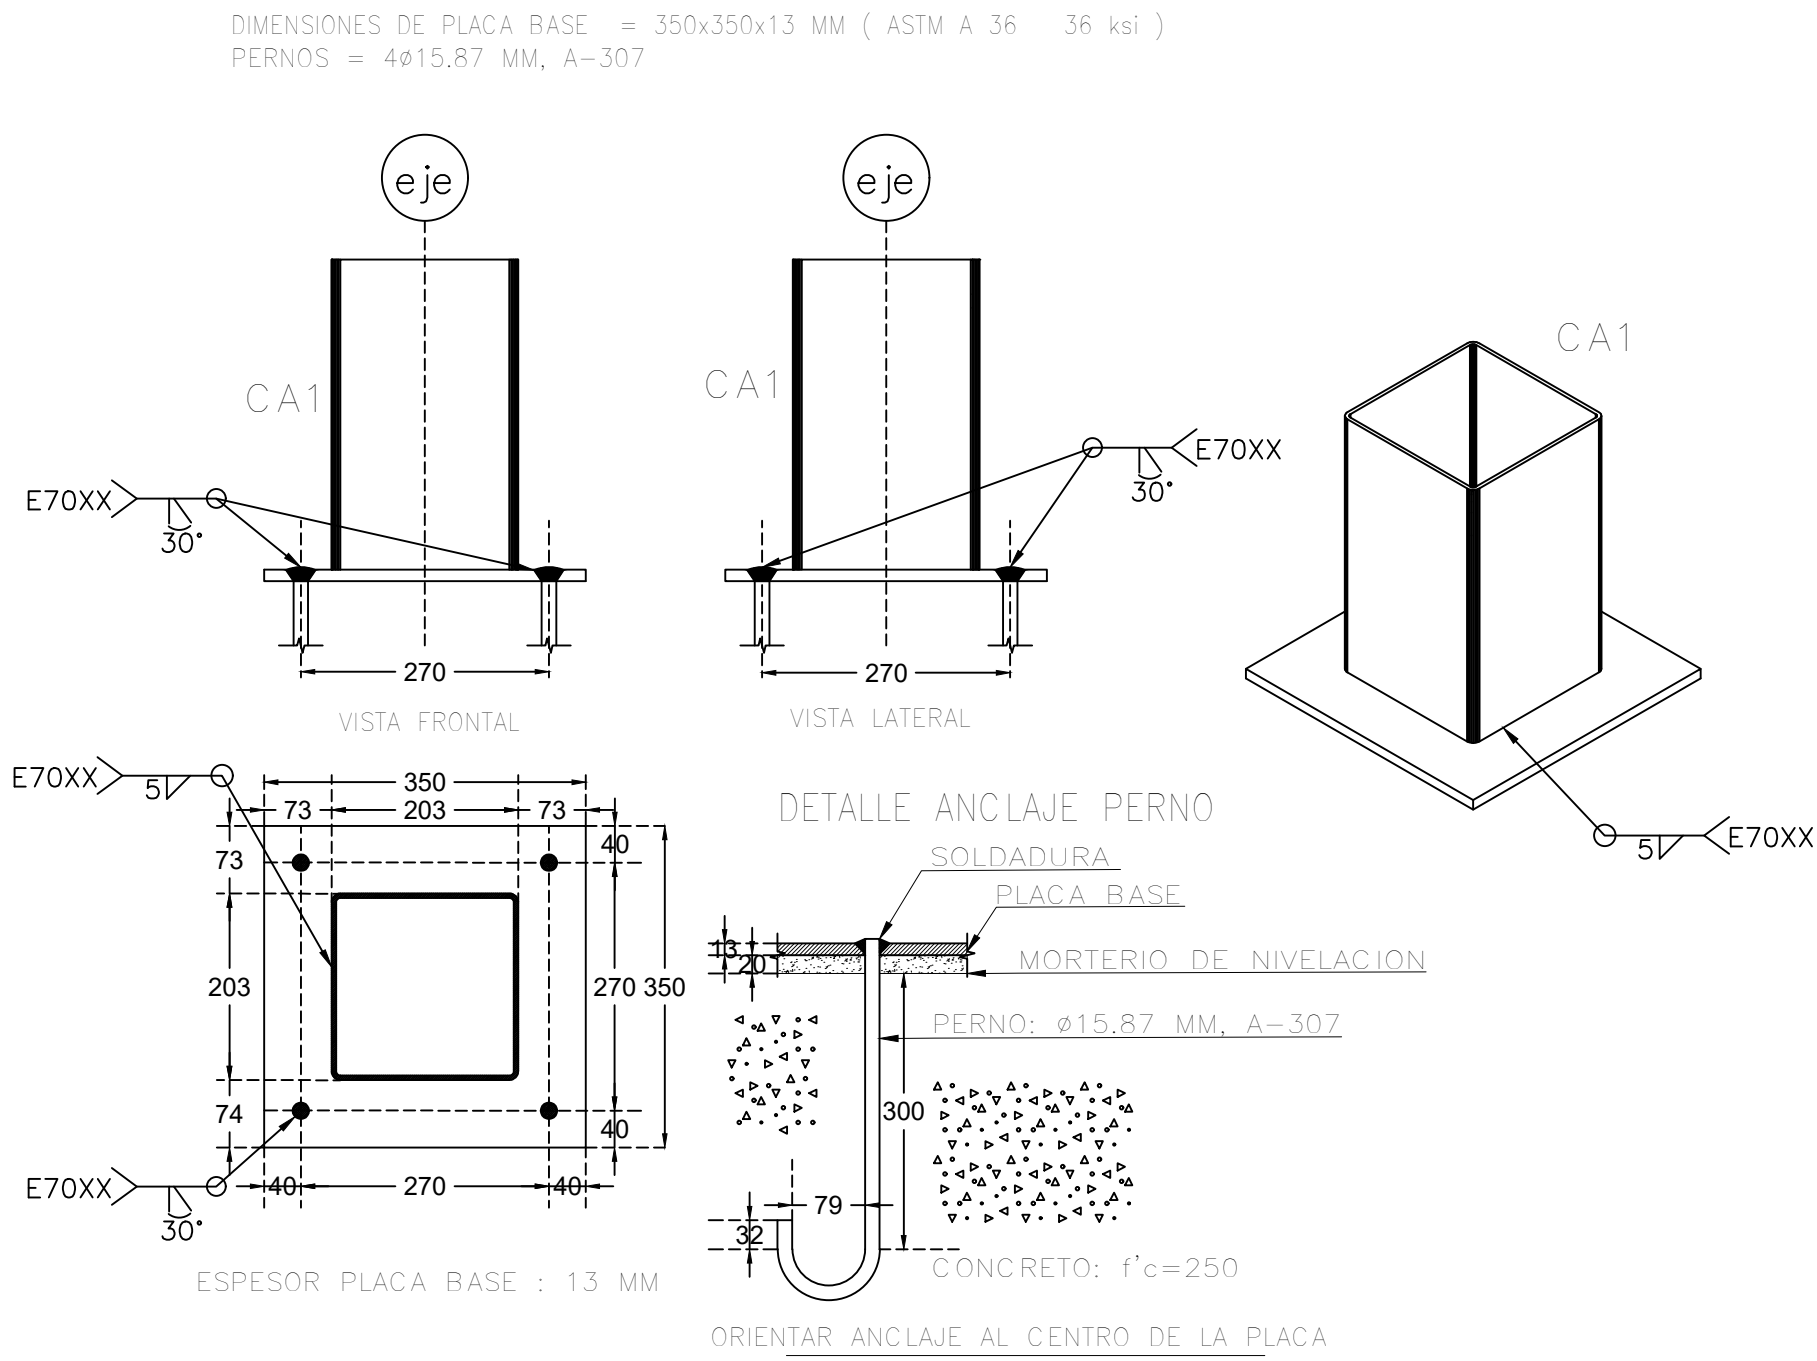


DETALLE PLACA BASE PLB -1

Acot: mm

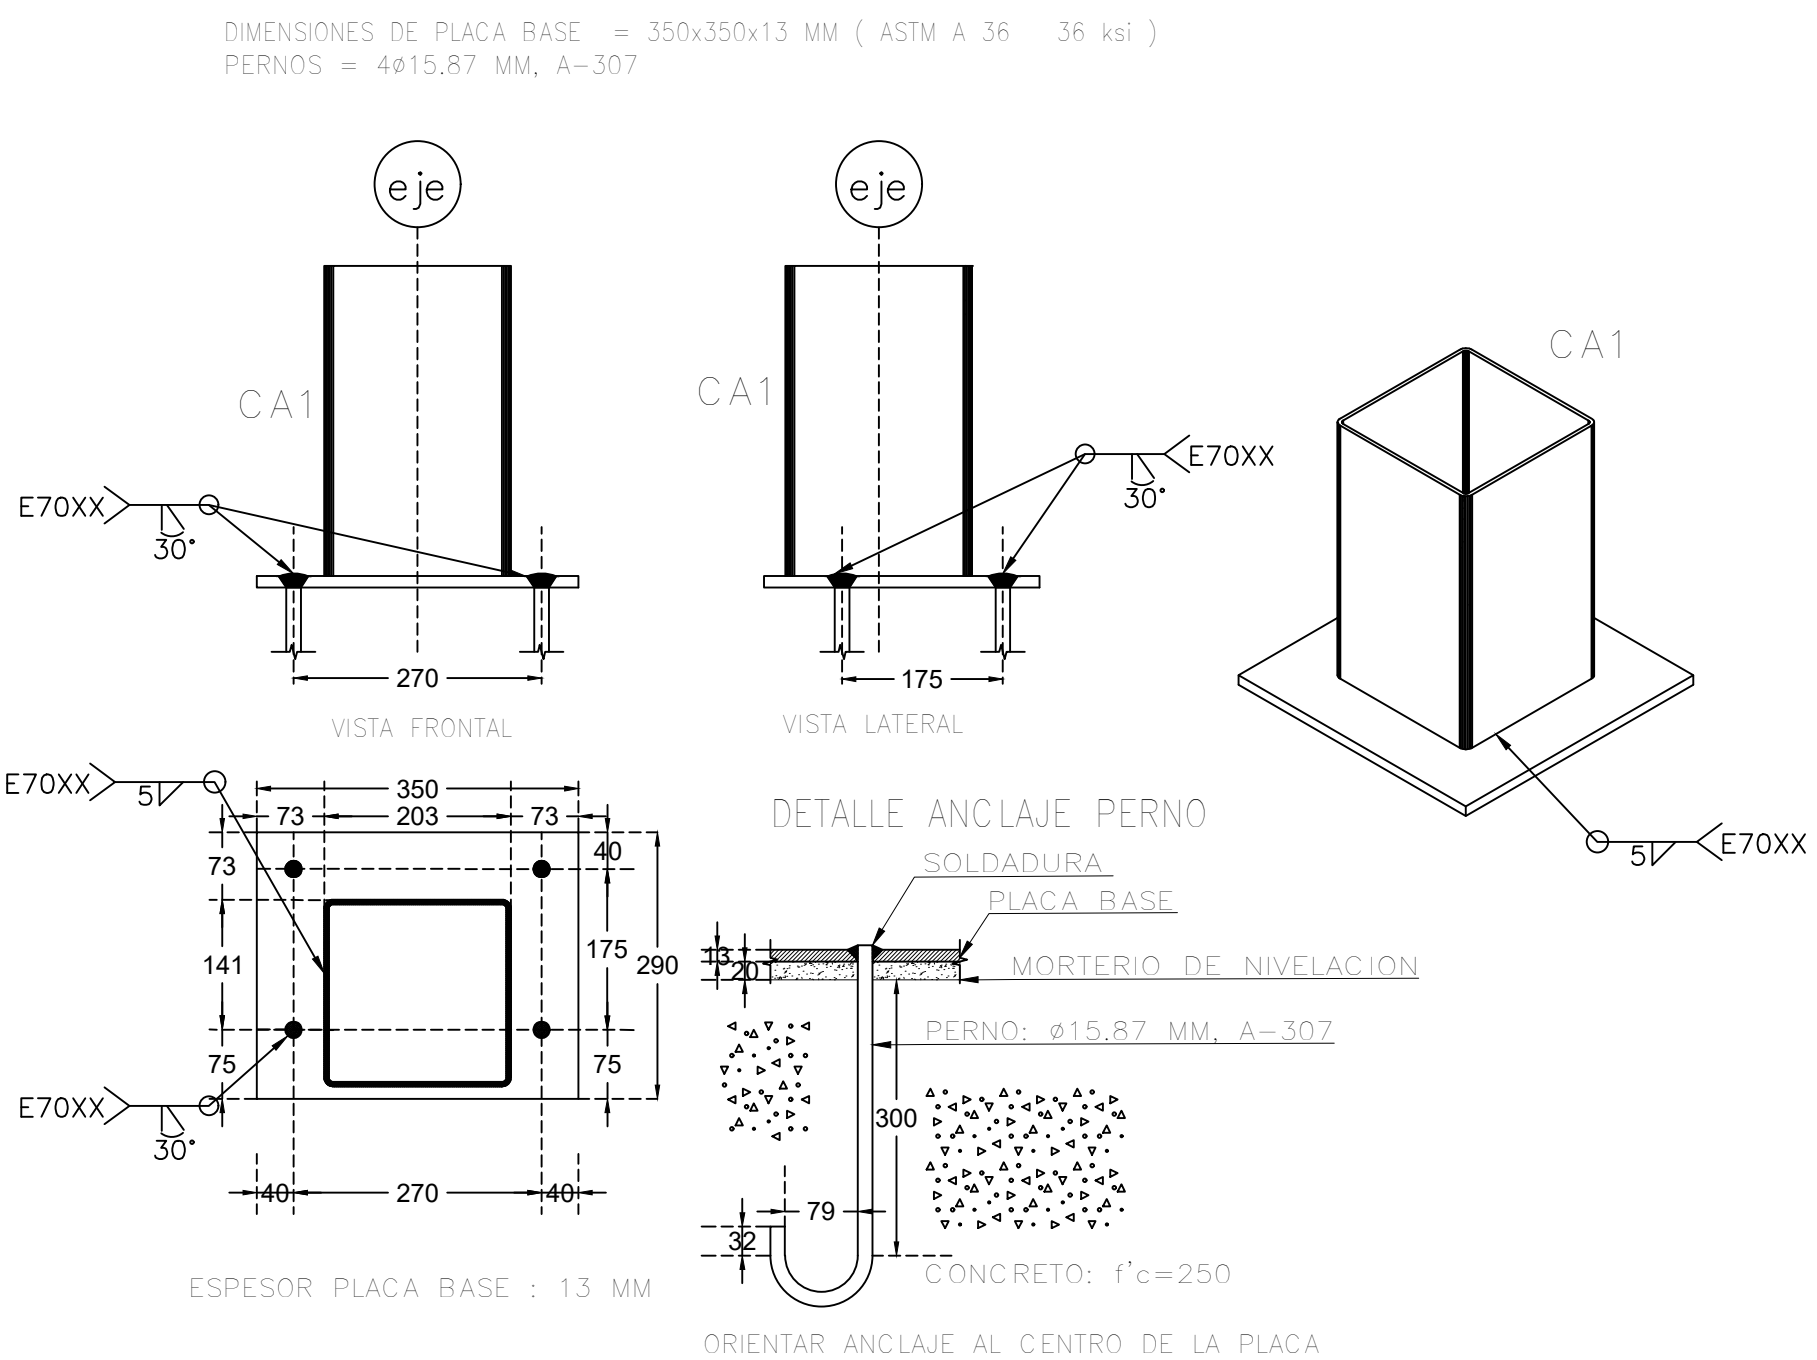

DETALLE PLACA BASE PLB -2

Acot: mm

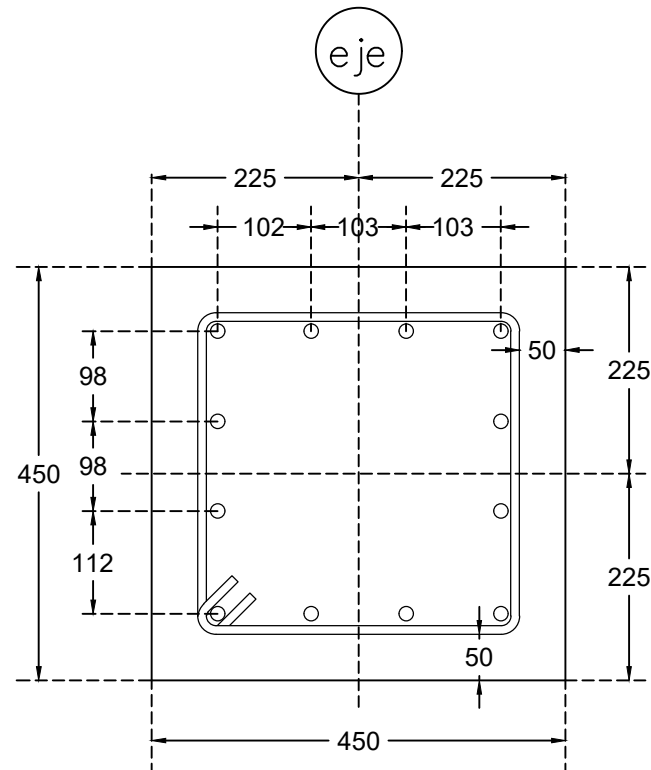


D1

DADO D1 DE 45x45CM BASE
DE CONCRETO F'C=250KG/CM²
,ARMADA CON 12VAR #5
EST.#3 @20CM

DETALLE DADO D1

Acot: mm

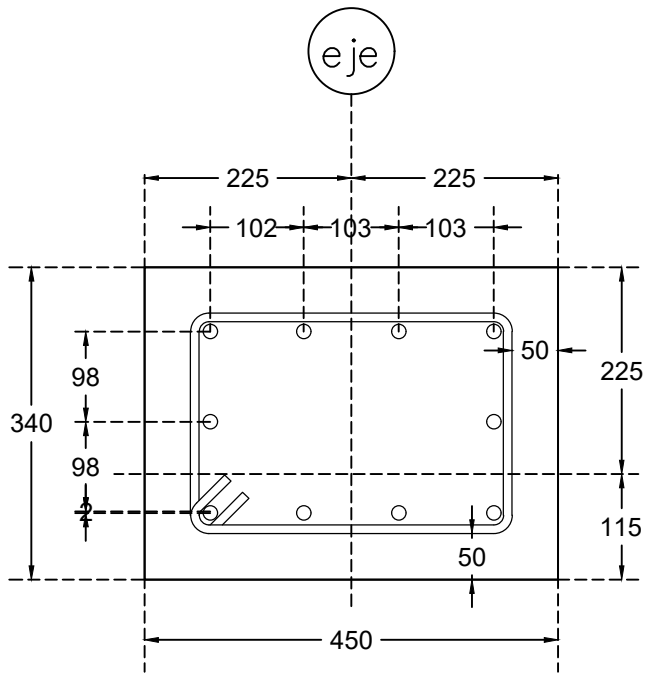

D2

DADO D1 DE 45x45CM BASE
DE CONCRETO F'C=250KG/CM²
,ARMADA CON 12VAR #5
EST.#3 @20CM

DETALLE DADO D2

Acot: mm



REVISIONES

NOTAS Y ESPECIFICACIONES

RESPONSABLES

RESPONSABLE DE DISEÑO ARQUITECTÓNICO:
ARQ. FRANCISCA ELIZABETH FLORES GARCIA
PROPIETARIO:
R.L. ING. ADRIAN CASTRO GUERRERO
DIRECTOR RESPONSABLE DE OBRA:
ING. RAFAEL MONDRAGON GARCIA

PROPIETARIO:
DESARROLLOS RESIDENCIALES LANDER S. A. DE C. V.
Bulevard Naiman #1116 - Jalisco y Sufragio CD. OREGÓN, SONORA. TEL. 413 52 79 413 52 80 413 52 83 fax 413 52 82
ESCALA:
Esc: 1:50
FECHA:
FEB/2026
REVISOR:
ARQ. ELIZABETH FLORES
ACOTACIONES:
METROS

PROYECTO:
CASA CLUB MDP NORTE

UBICACION:
MAR DE PLATA
HERMOSILLO, SONORA

CONTENIDO:
CIMENTACIÓN
CUBIERTA METÁLICA 1

PLANO No:
EST - 03

ARCHIVO: 03- ESTRUCTURAL CASA CLUB MDP NORTE 260223.dwg