



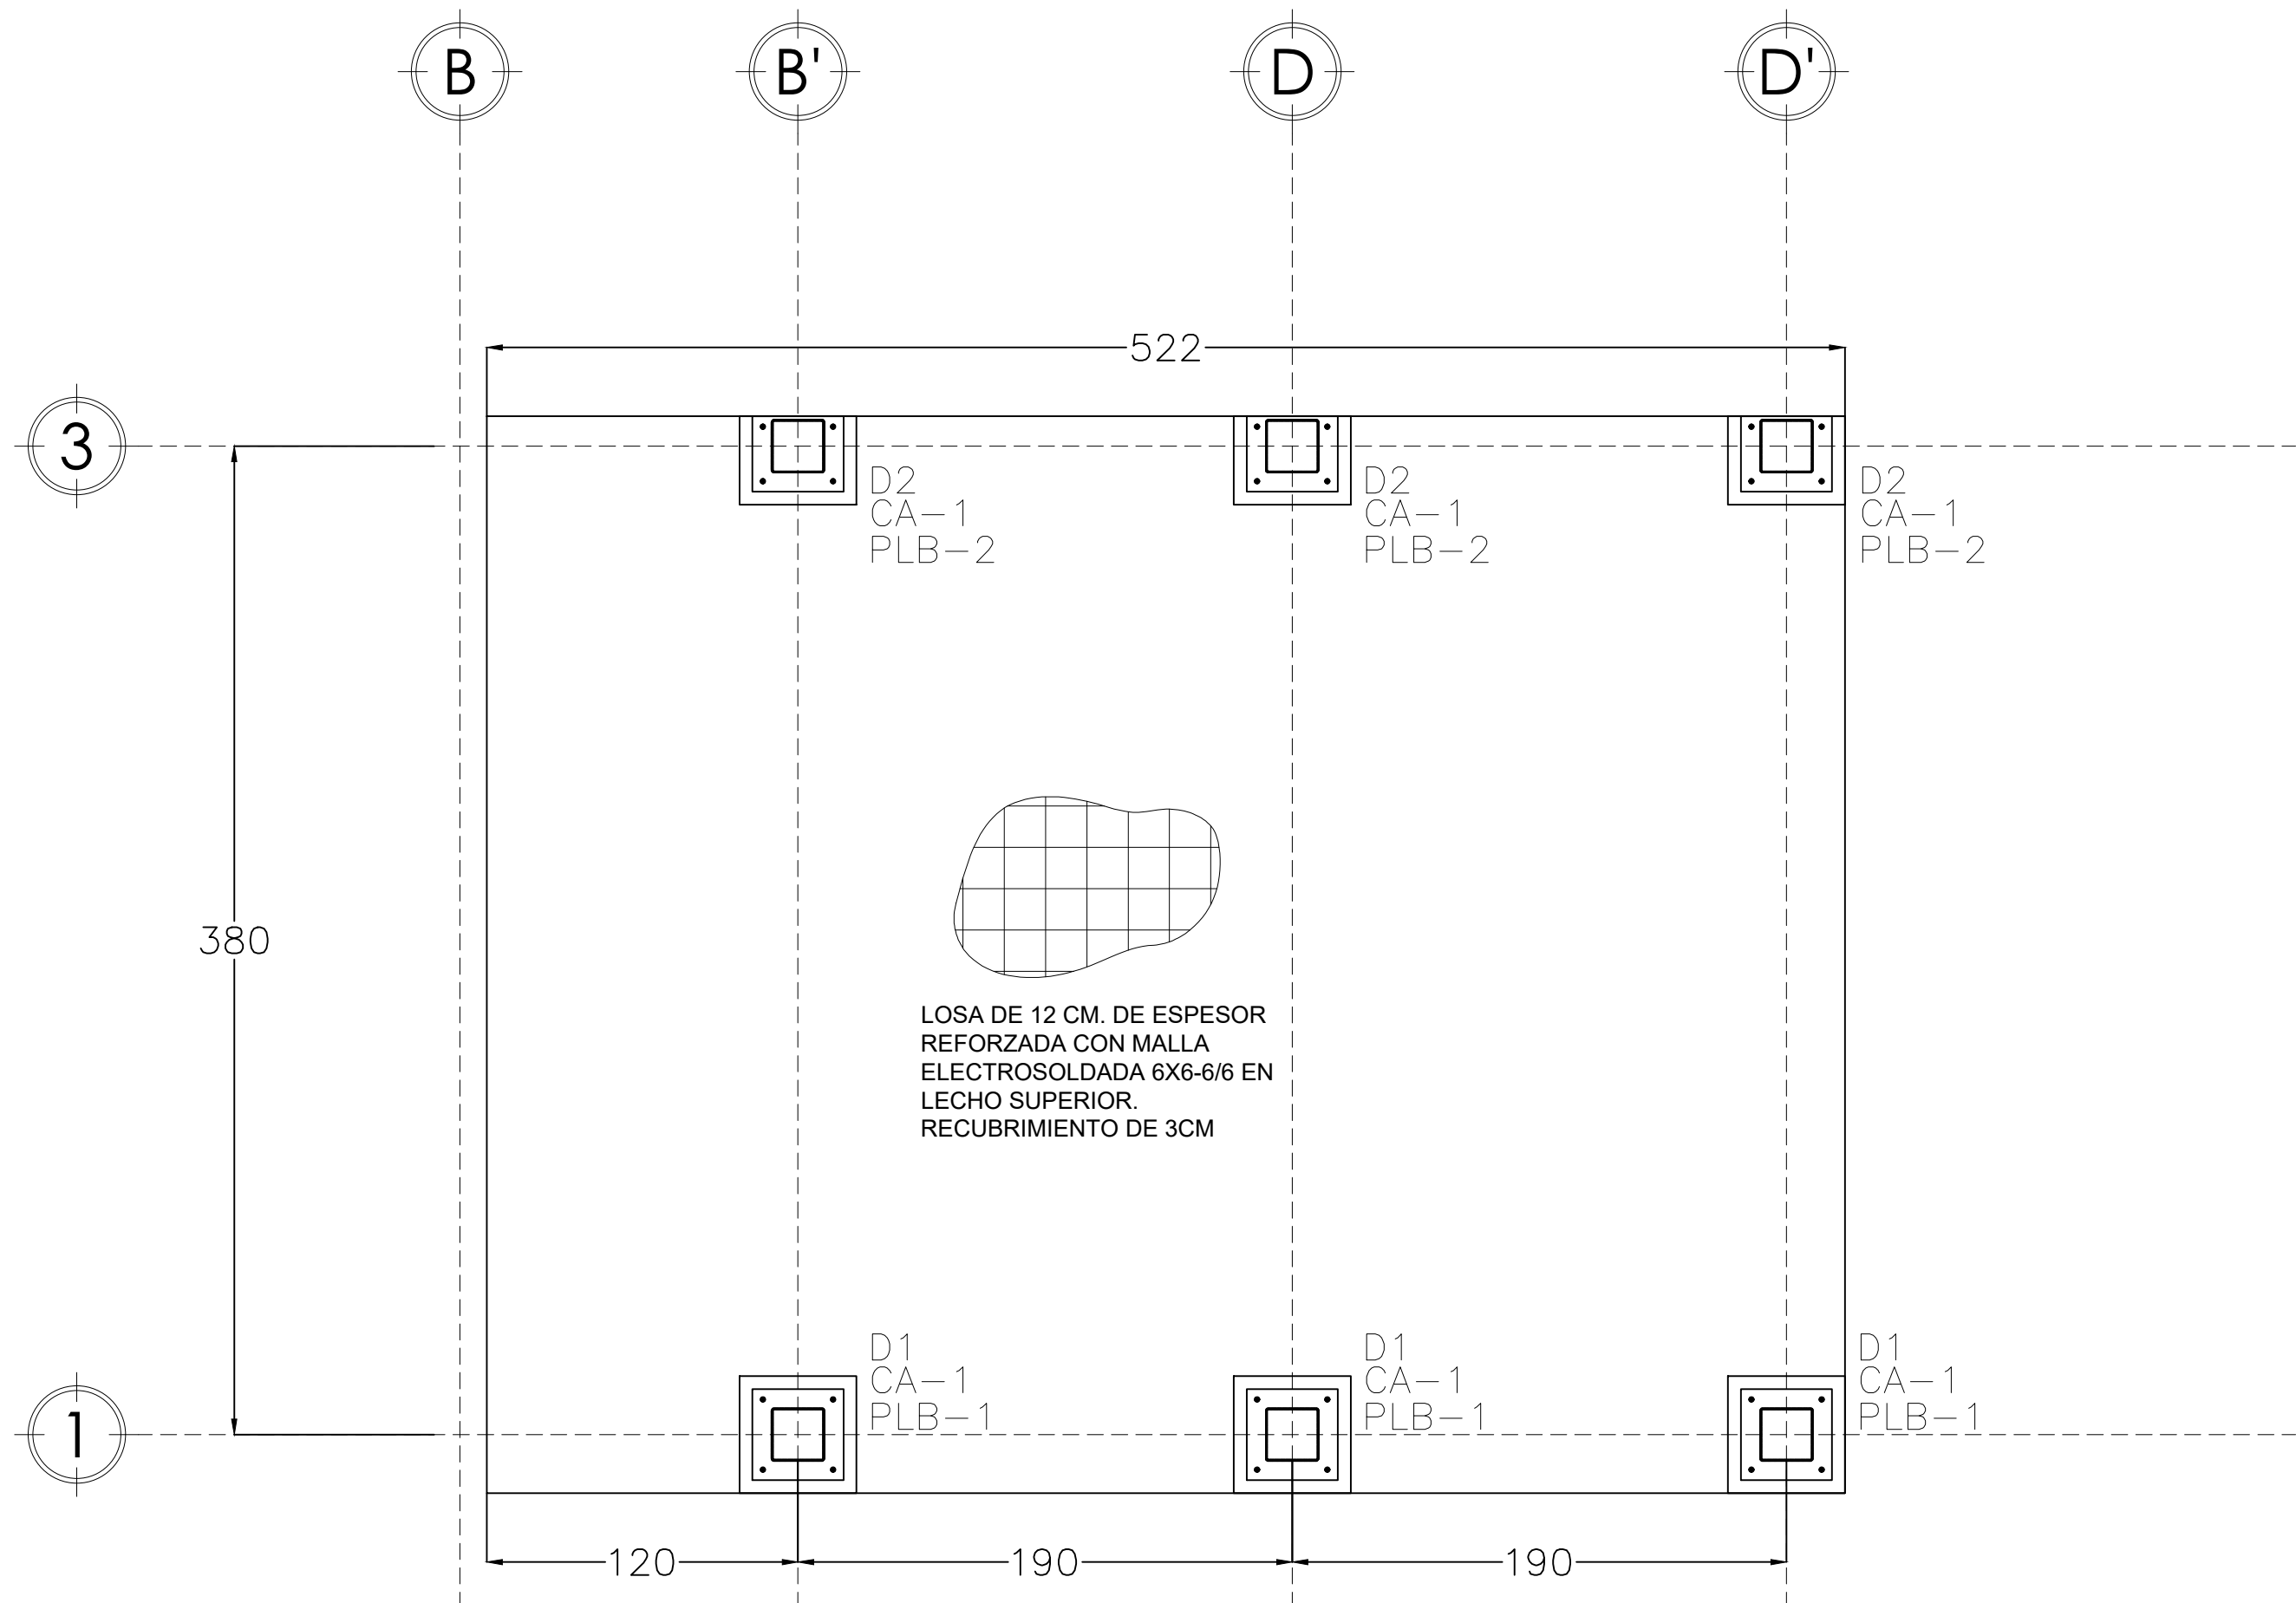


LOSA DE CIMENTACIÓN 2

Acot: mm

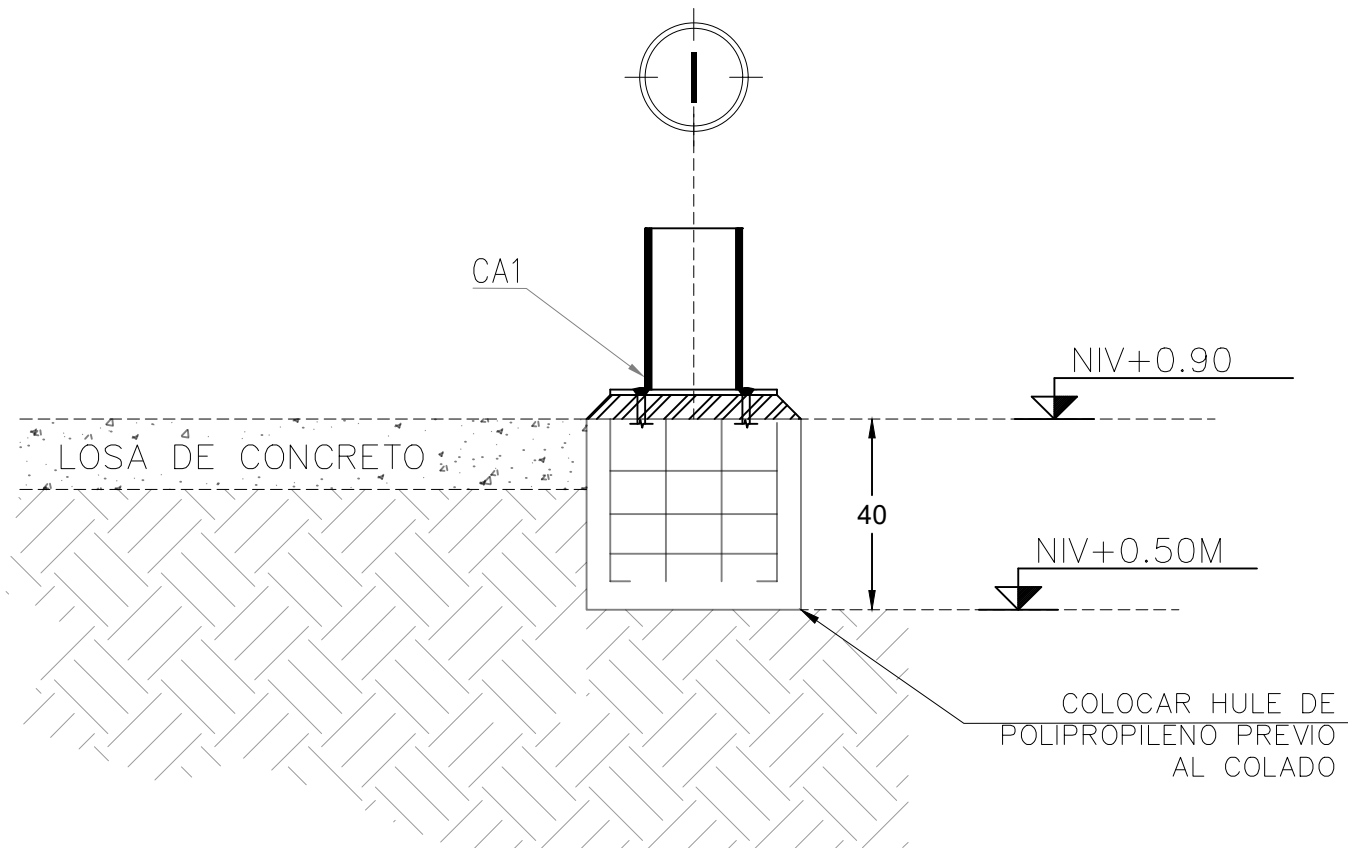


DETALLE - CONEXIÓN COLUMNA ALZADO

Acot: cm

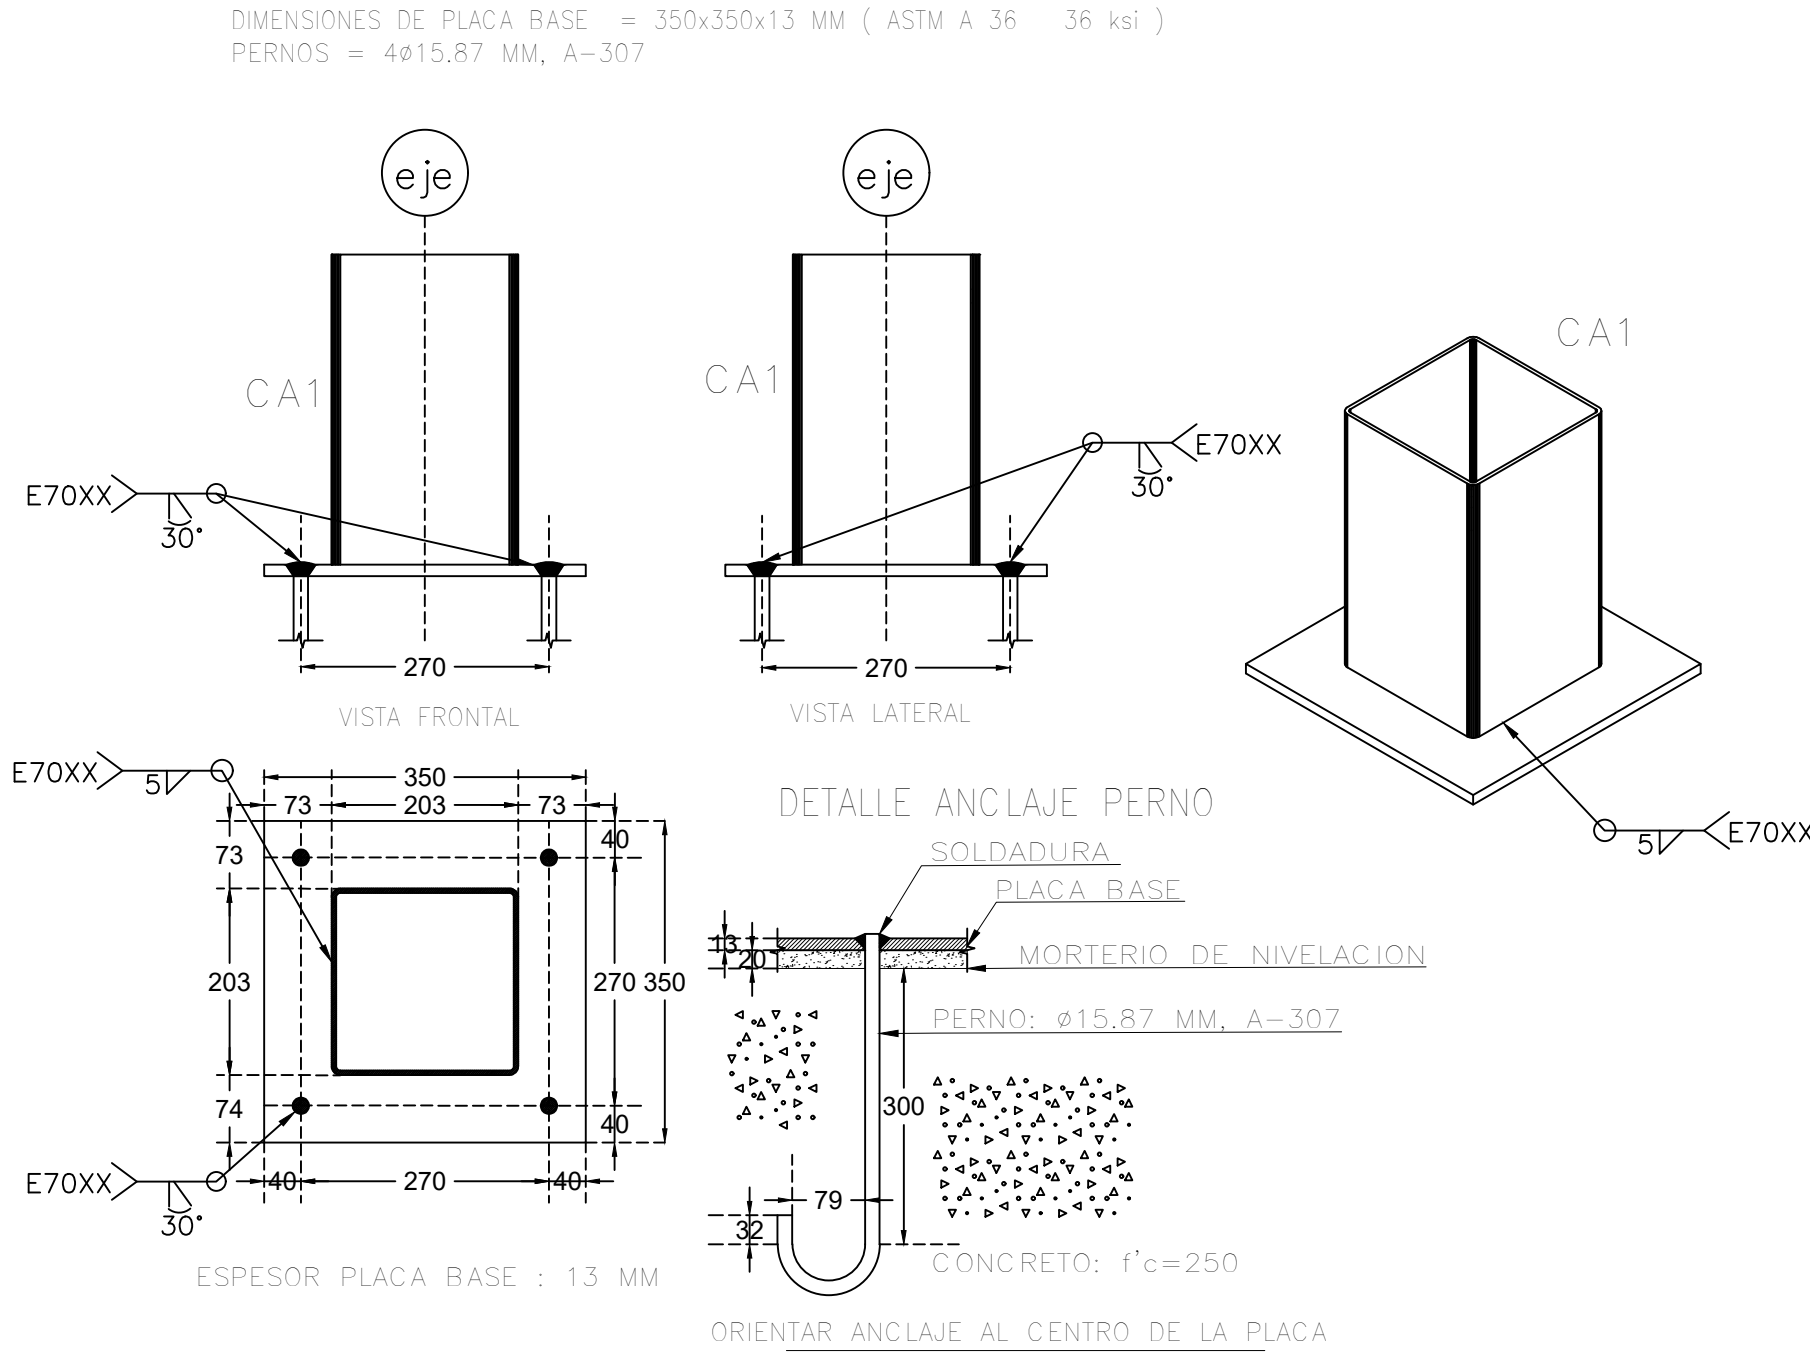


DETALLE PLACA BASE PLB -1

Acot: mm

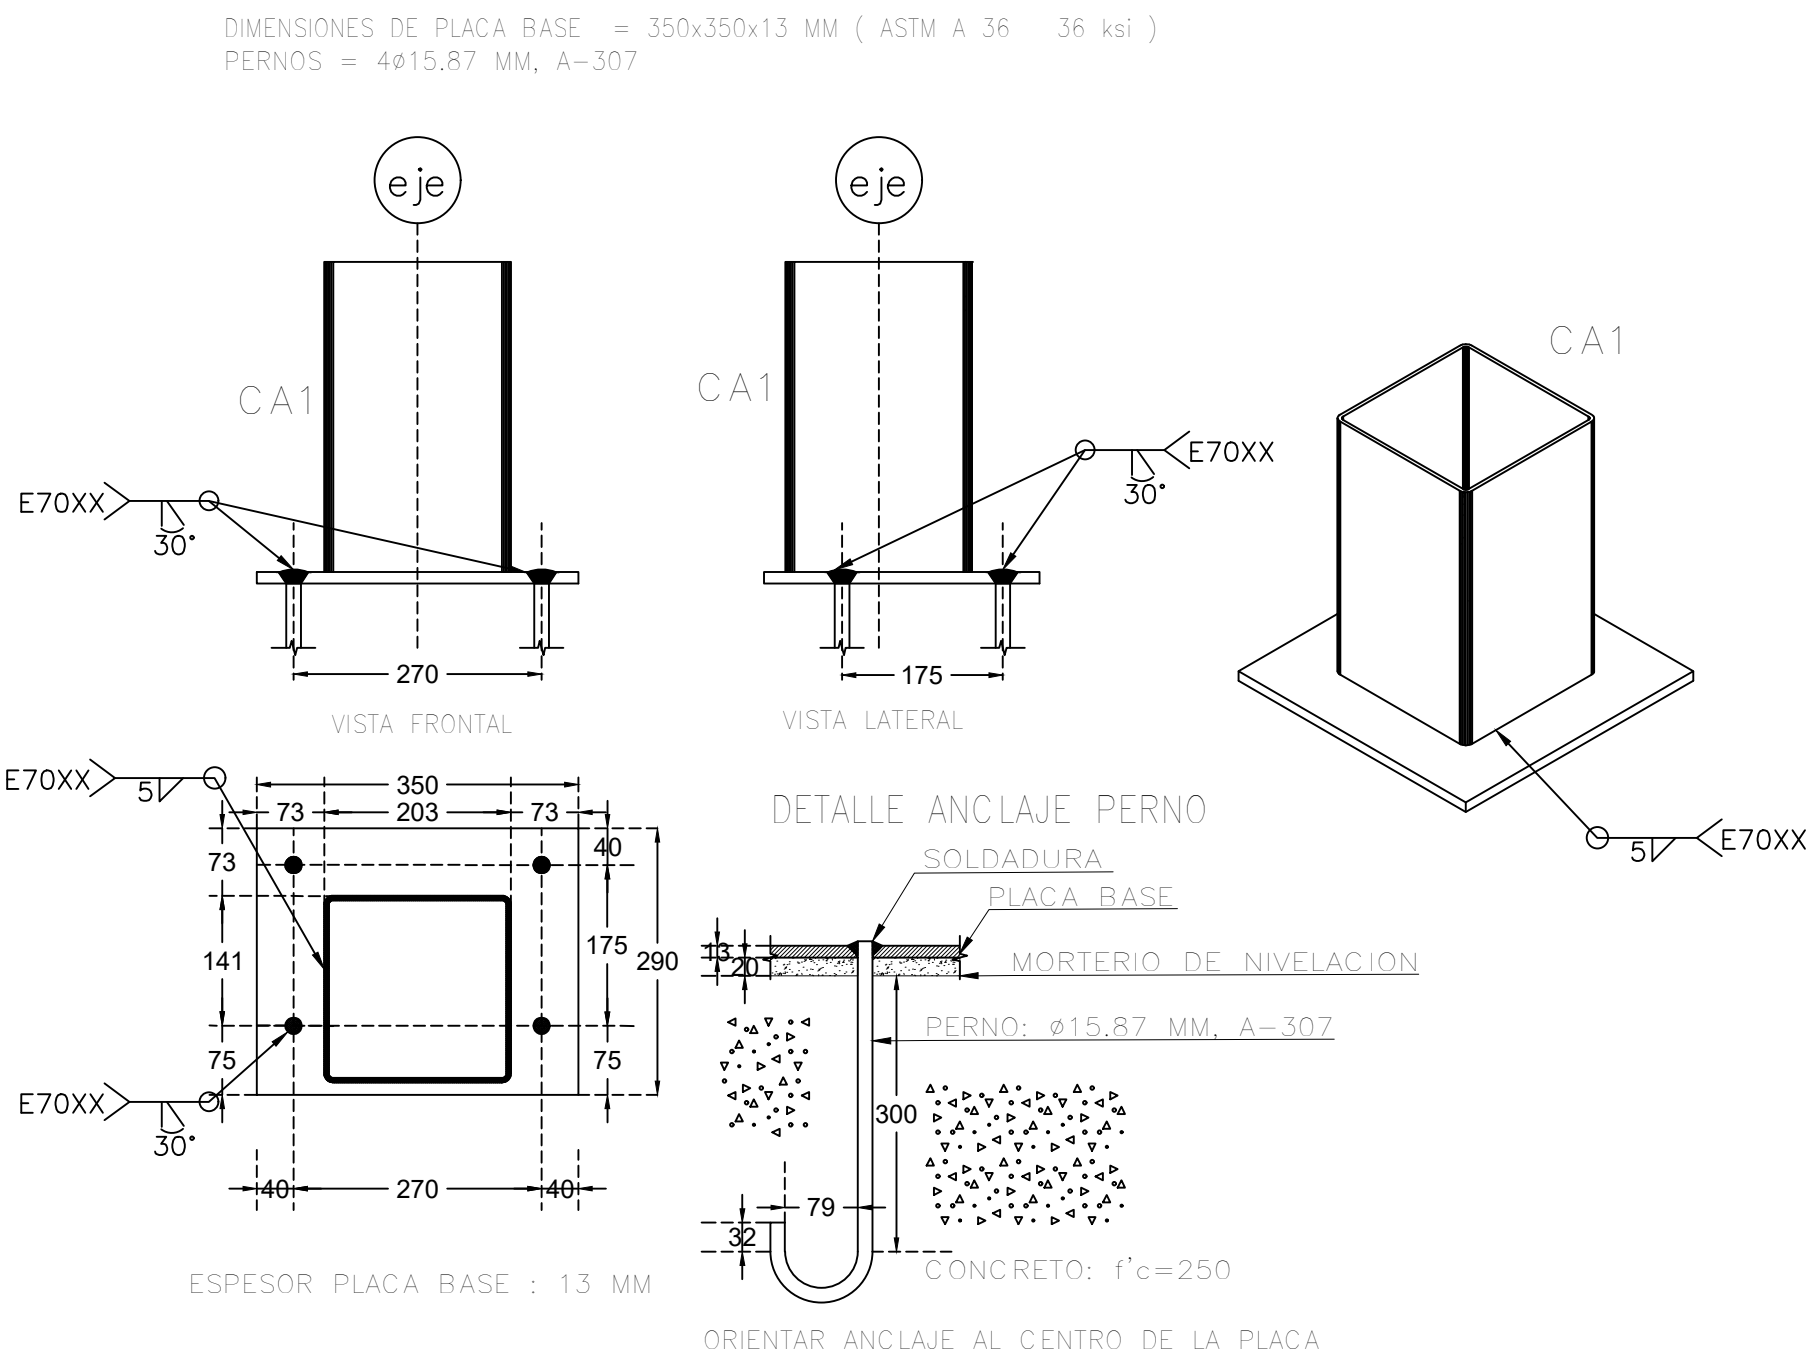

DETALLE PLACA BASE PLB -2

Acot: mm

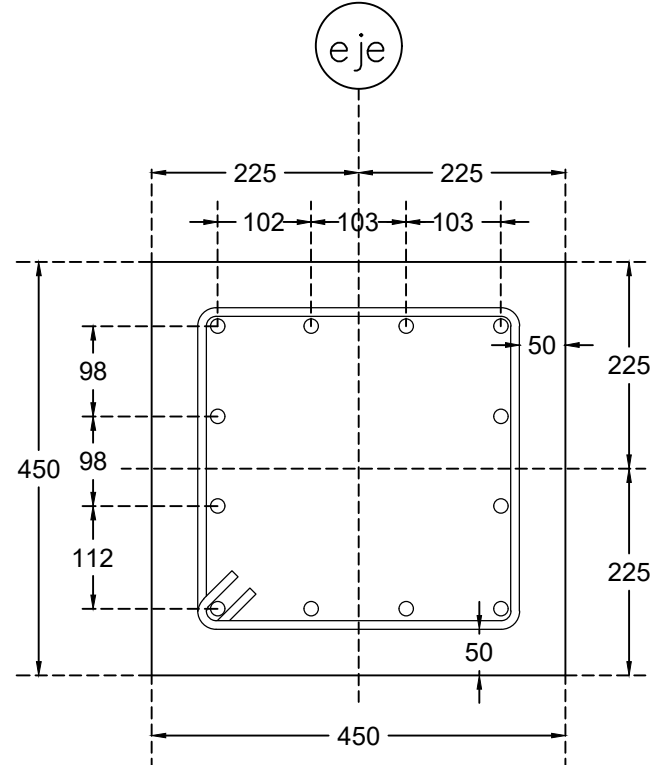


D1

DADO D1 DE 45x45CM BASE DE CONCRETO F'C=250KG/CM², ARMADA CON 12VAR #5 EST.#3 @20CM

DETALLE DADO D1

Acot: mm

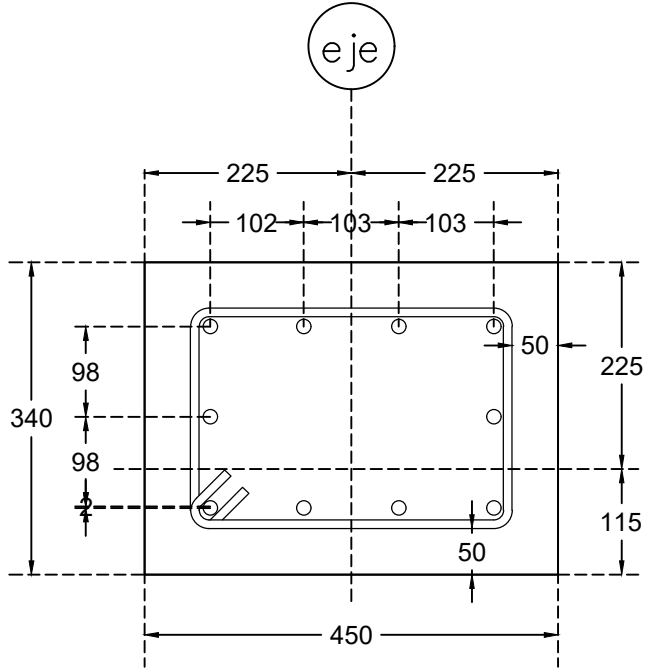

D2

DADO D1 DE 45x45CM BASE DE CONCRETO F'C=250KG/CM², ARMADA CON 12VAR #5 EST.#3 @20CM

DETALLE DADO D2

Acot: mm

LOCALIZACIÓN

LANDER

REVISIONES

NOTAS Y ESPECIFICACIONES

RESPONSABLES

RESPONSABLE DE DISEÑO ARQUITECTÓNICO:

ARQ. FRANCISCA ELIZABETH FLORES GARCIA

PROPIETARIO:

R.L. ING. ADRIAN CASTRO GUERRERO

DIRECTOR RESPONSABLE DE OBRA:

ING. RAFAEL MONDRAGON GARCIA

PROPIETARIO:

DESARROLLOS RESIDENCIALES LANDER S. A. DE C. V.

Bulevar Naiman #1116 - Jalisco y Sultagio
CD. OREGON, SONORA
TEL. 413 52 79 413 52 80 413 52 83 fax 413 52 82

ESCALA:

Esc: 1:50

REVISION:

1.0

FECHA:

E.F.G.

FECHA:

FEB/2026

REVISOR:

ARQ. ELIZABETH FLORES

ACOTACIONES:

METROS

PROYECTO:

CASA CLUB MDP NORTE

UBICACION:

MAR DE PLATA HERMOSILLO, SONORA

CONTENIDO:

CIMENTACIÓN CUBIERTA METÁLICA 2

PLANO No:

EST - 05

ARCHIVO: 03- ESTRUCTURAL CASA CLUB MDP NORTE 260223.dwg