




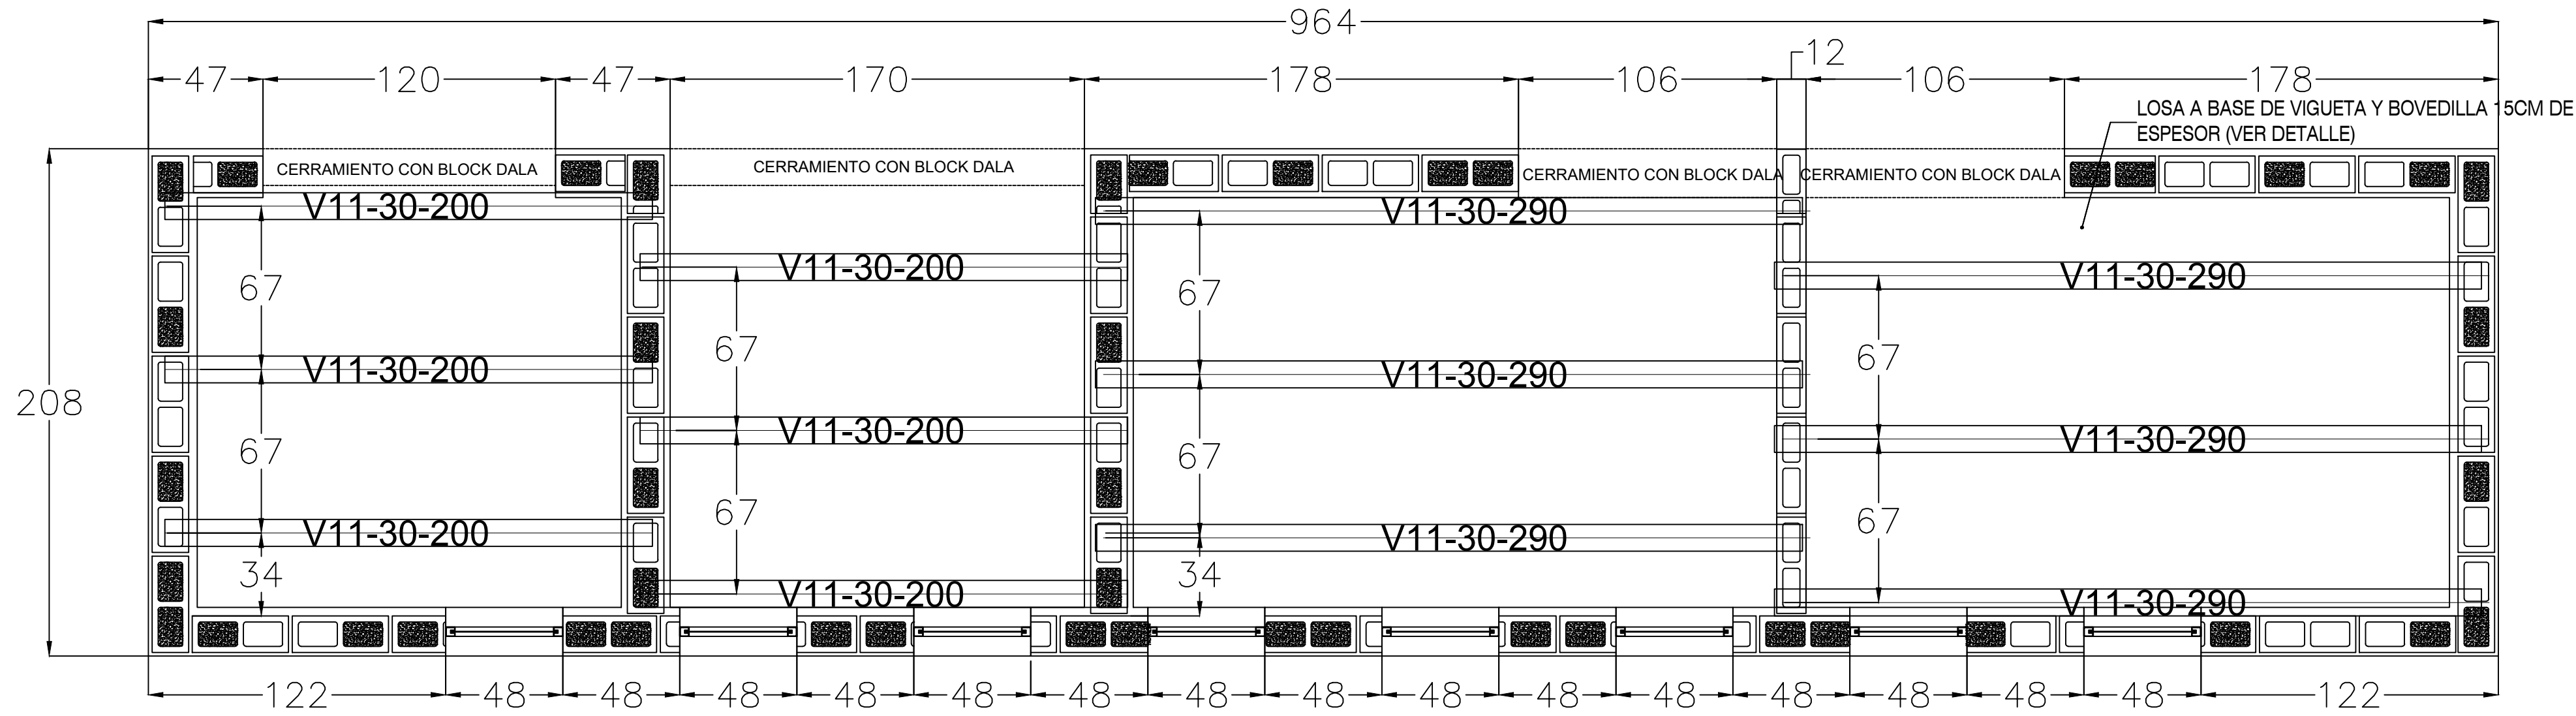


PLANTA ESTRUCTURAL DE AZOTEA MÓDULO DE BAÑOS
PLANTA

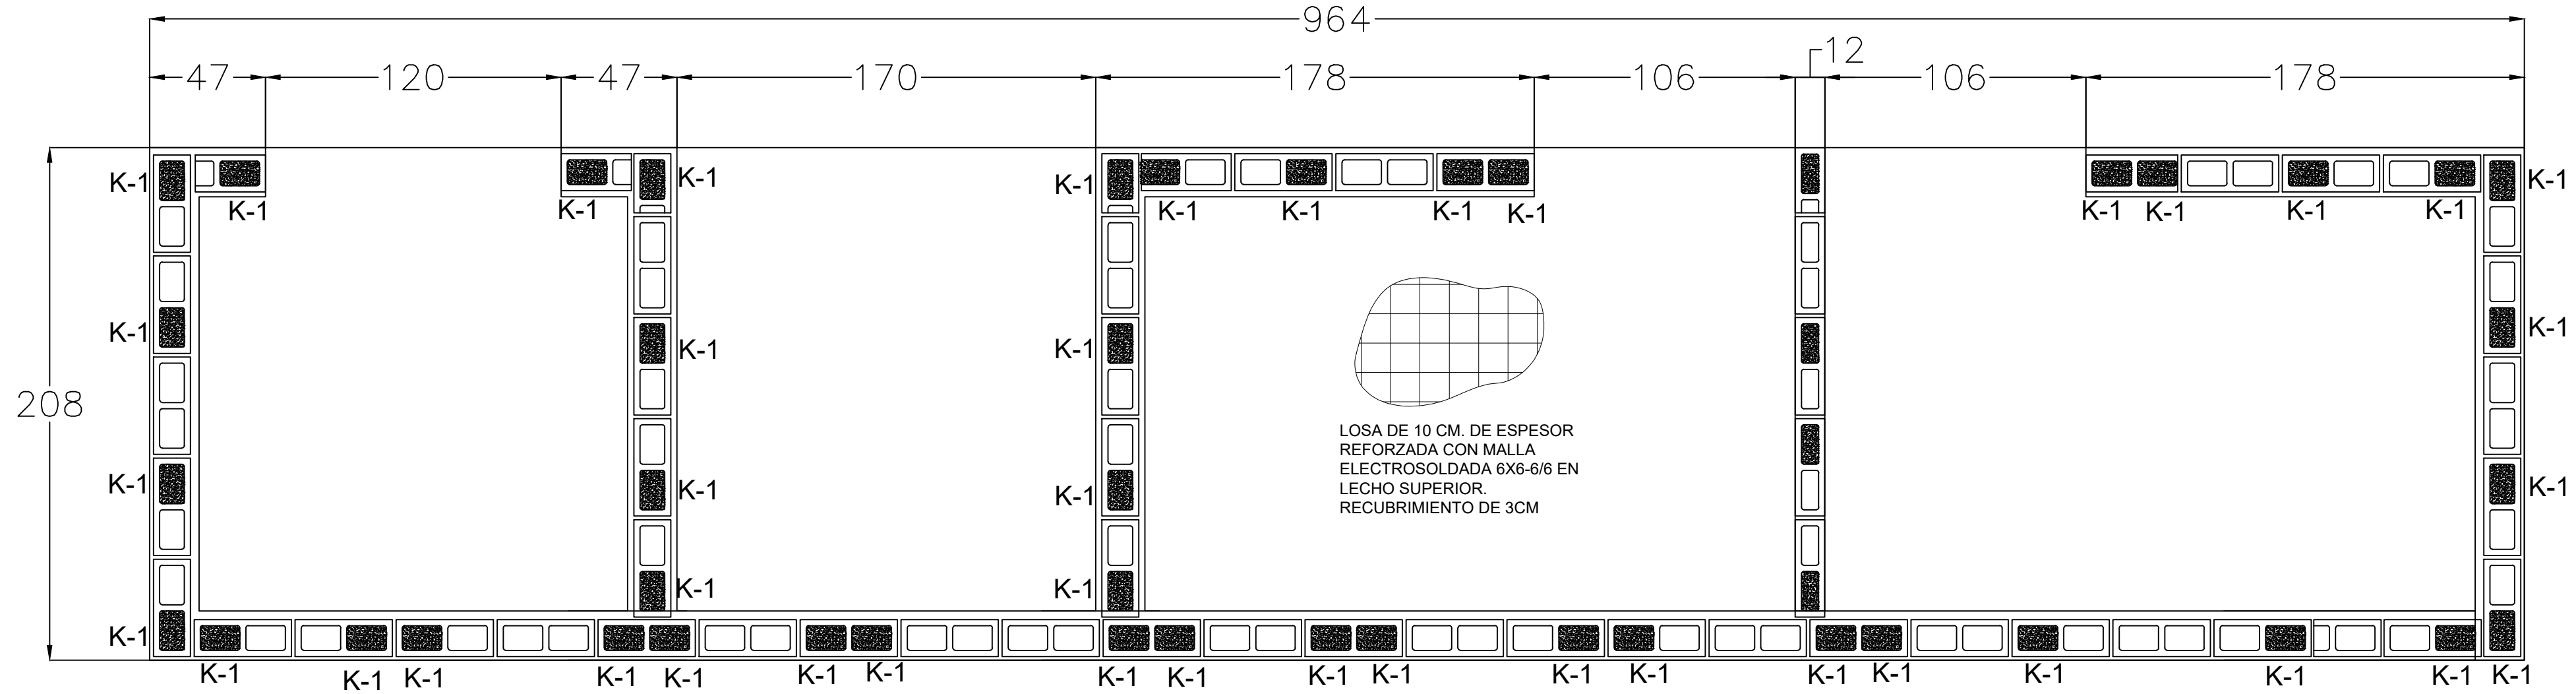


CIMENTACIÓN MÓDULO DE BAÑOS
PLANTA

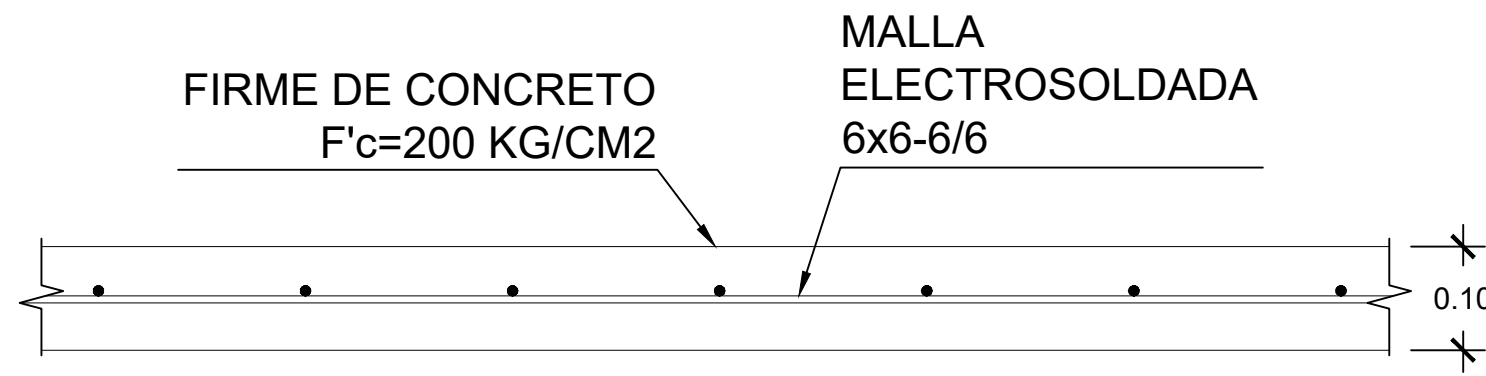


ARMADO DE FIRME DE CONCRETO
ALZADO
ESCALA 1:10

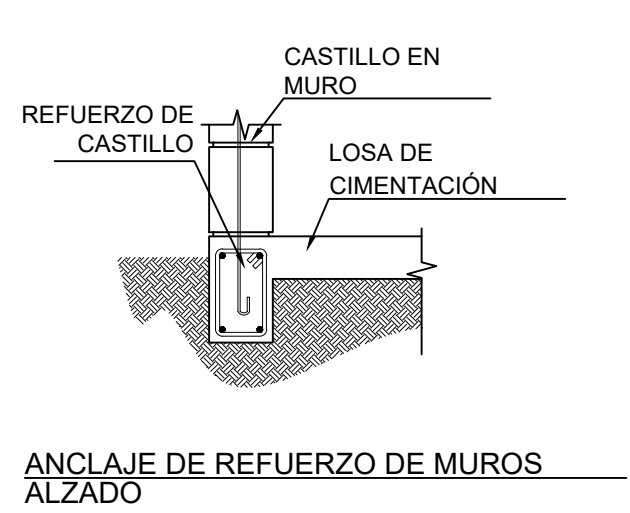



DETALLE DE ANCLAJE DE
CASTILLO EN ESQUINA Ó INTERSECCIÓN
ISOMETRICO-ESCALA 1:20

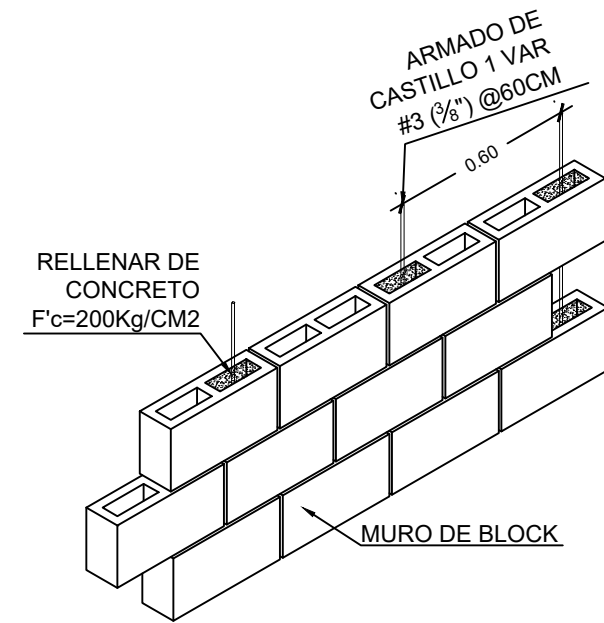


DETALLE TIPO DE REFUERZO PARA MURO DE BLOCK
ISOMETRICO
ESCALA 1:20

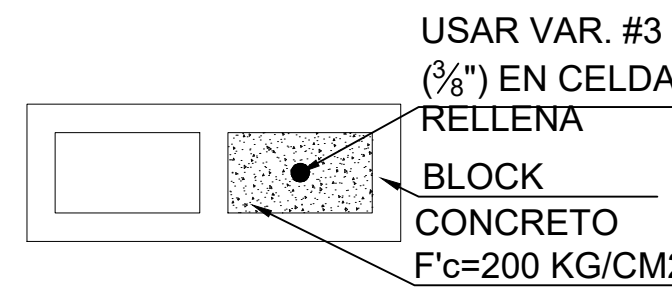

CASTILLO
PLANTA
K-1
ESC. 1:10

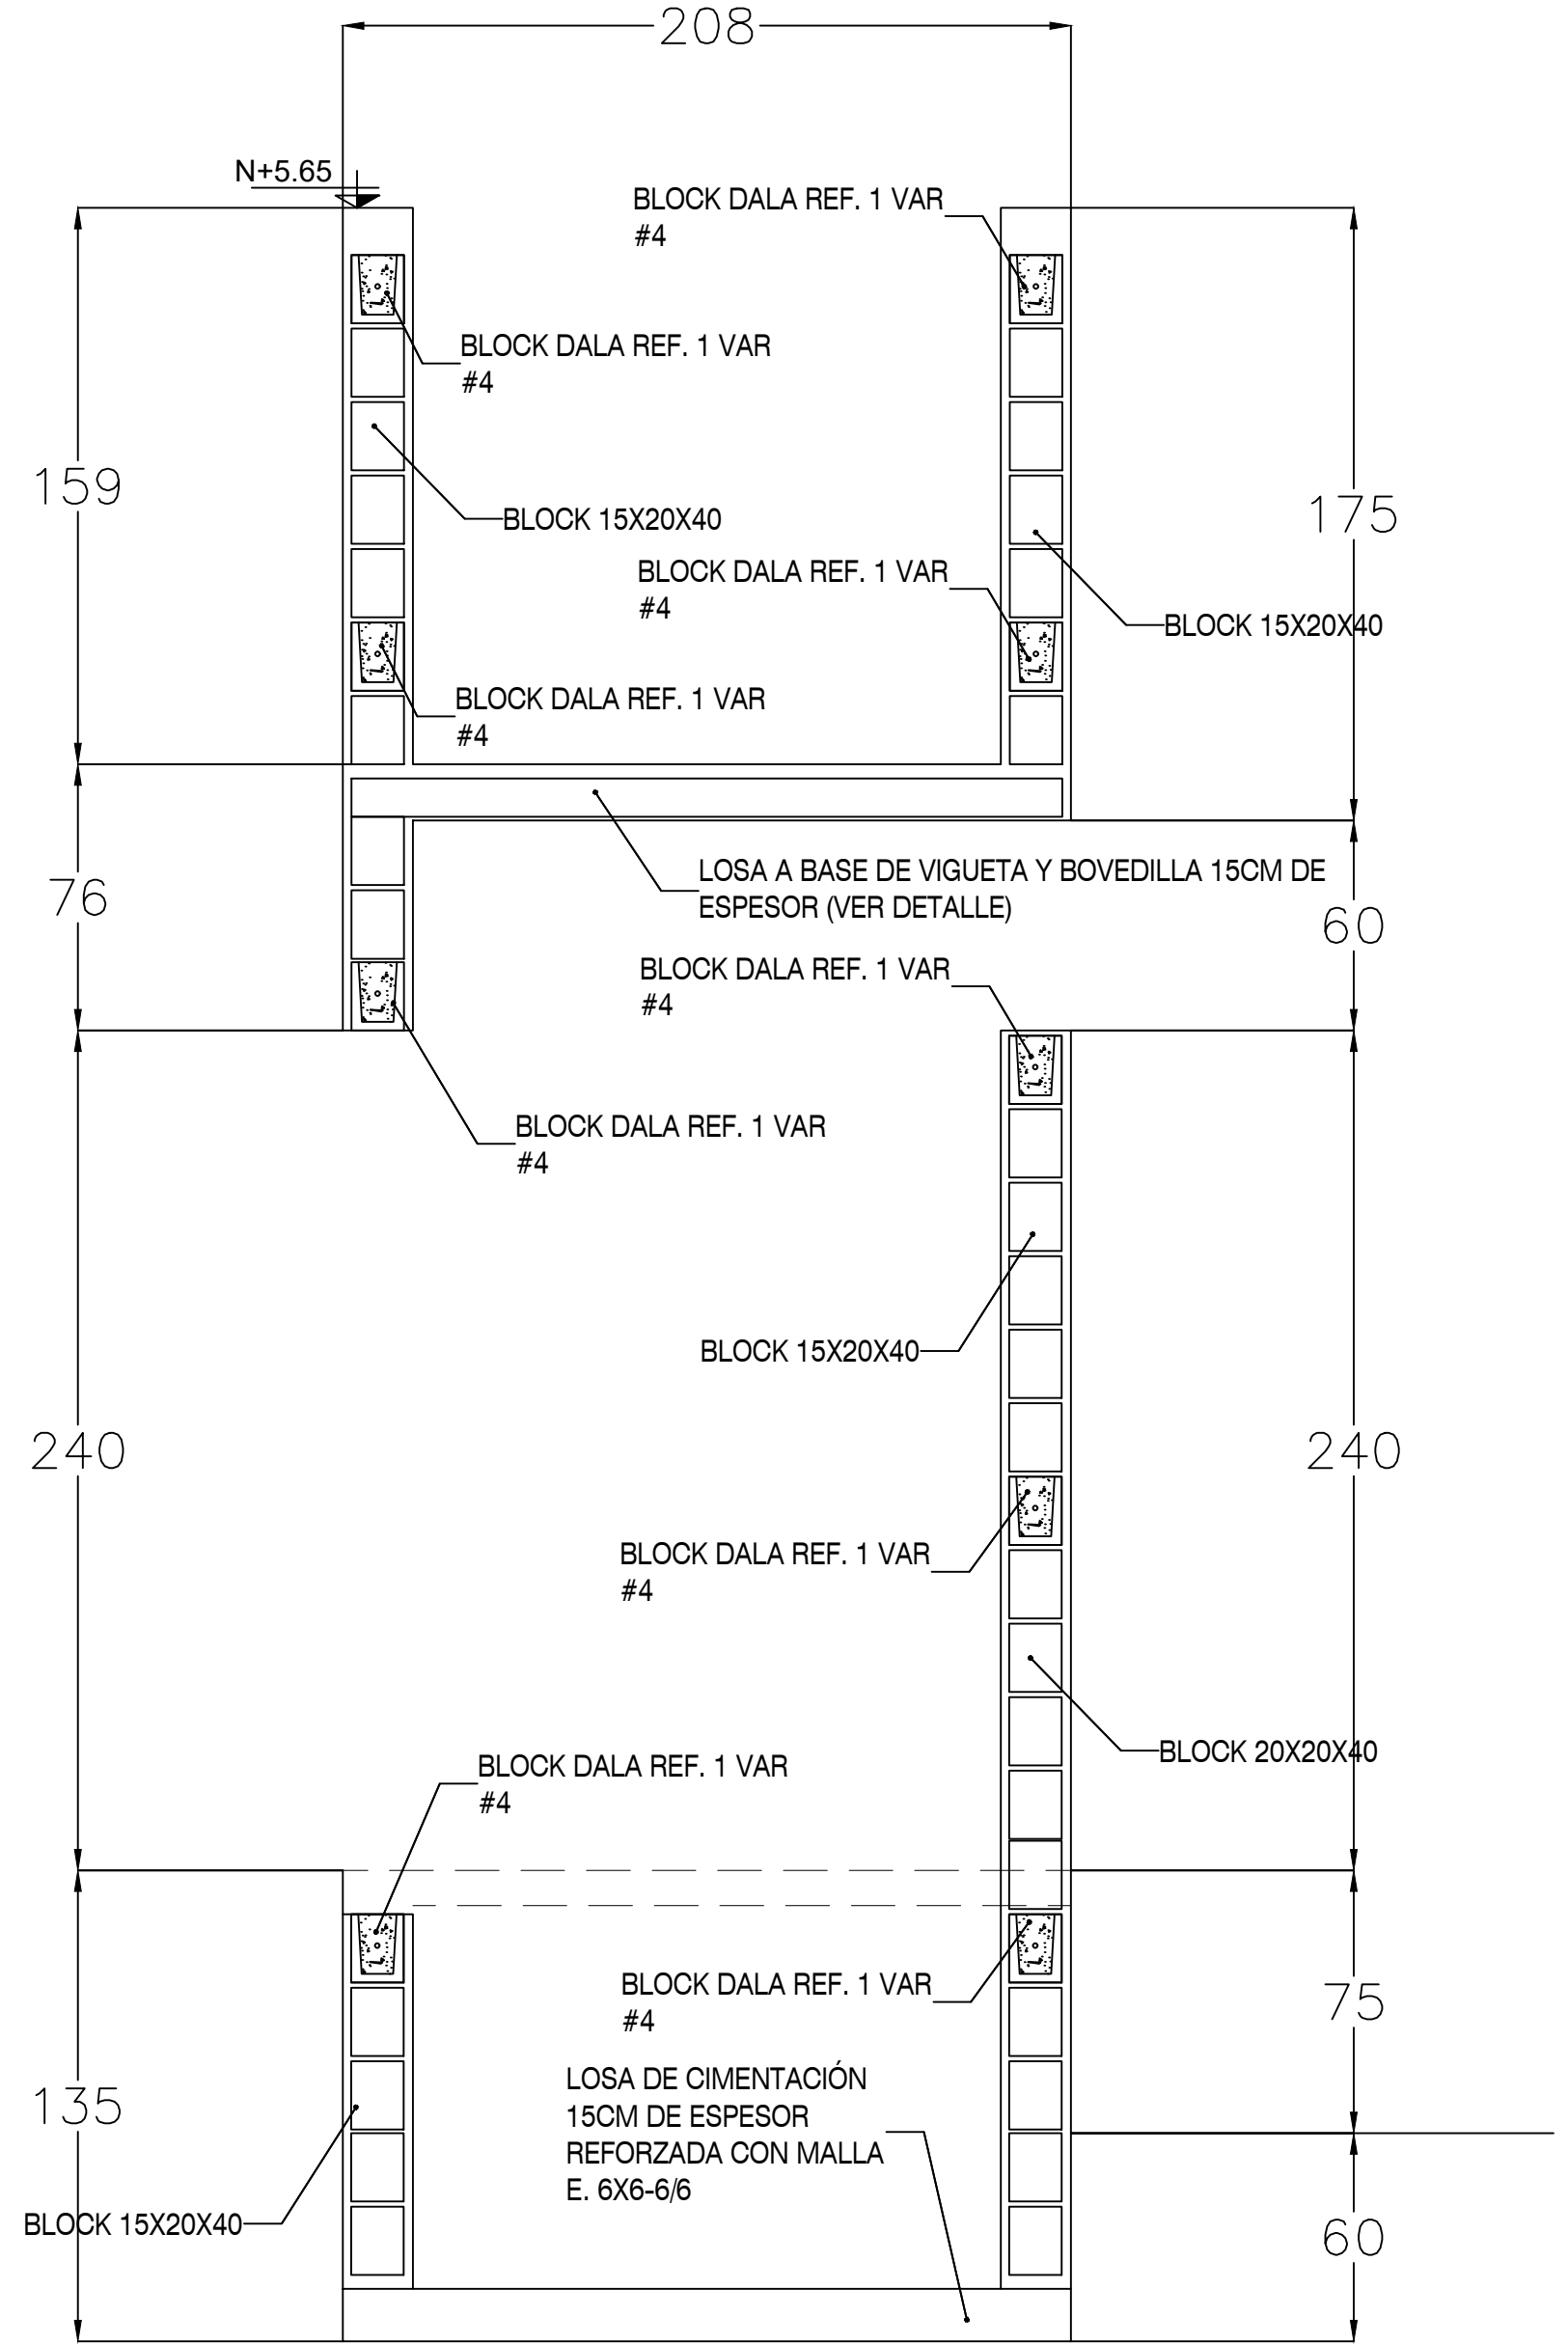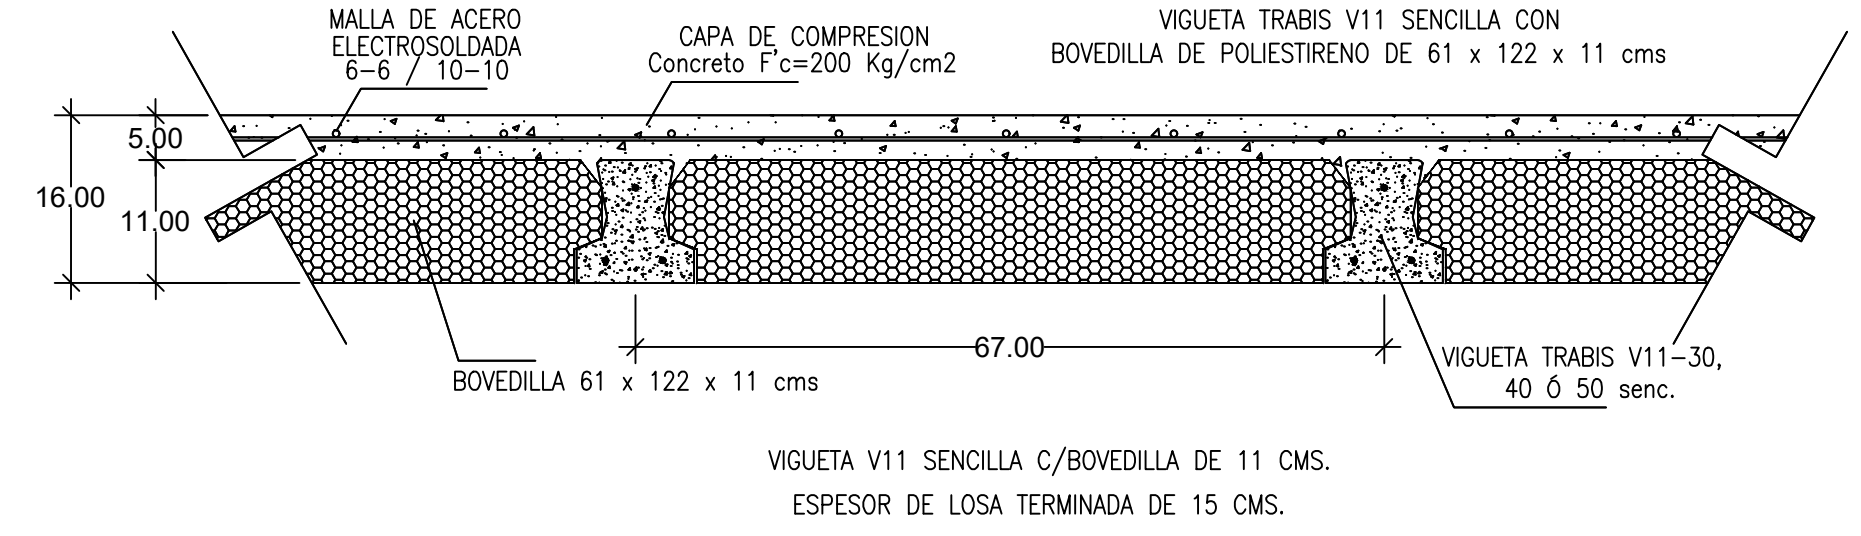

SECCIÓN MÓDULO DE BAÑOS
ALZADO

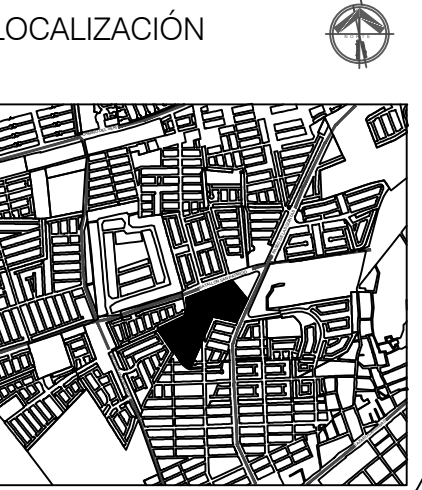

REVISIONES

NOTAS Y ESPECIFICACIONES

RESPONSABLES

RESPONSABLE DE DISEÑO ARQUITECTÓNICO:

ARQ. FRANCISCA ELIZABETH FLORES GARCIA

PROPIETARIO:

R.L. ING. ADRIAN CASTRO GUERRERO

DIRECTOR RESPONSABLE DE OBRA:

ING. RAFAEL MONDRAGON GARCIA

PROPIETARIO:

DESARROLLOS RESIDENCIALES

LANDER S. A. DE C. V.

Bulevar Naimar #1116 - Jalisco y Sufragio

CD. OREGÓN, SONORA.

TEL. 413 52 79 413 52 80 413 52 83 fax 413 52 82

ESCALA:

Esc: 1:50 REGION: 1.0

UBIC: E.F.G. FECH: FEB/2026

REVIS: ARQ. ELIZABETH FLORES ACOTACIONES: METROS

PROYECTO:

CASA CLUB MDP NORTE

UBICACION:

MAR DE PLATA

HERMOSILLO, SONORA

CONTENIDO:

ESTRUCTURAL DE

MÓDULO DE BAÑOS

PLANO No:

EST - 06

ARCHIVO: 03.-ESTRUCTURAL CASA CLUB MDP NORTE 260223.dwg