




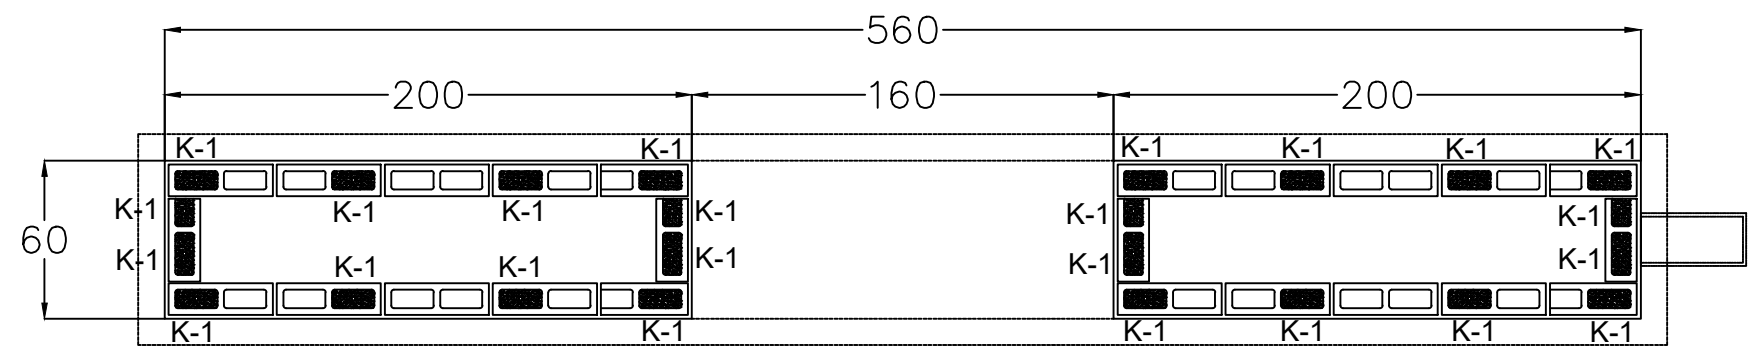


ESTRUCTURA DE PÓRTICO PR-01
PLANTA

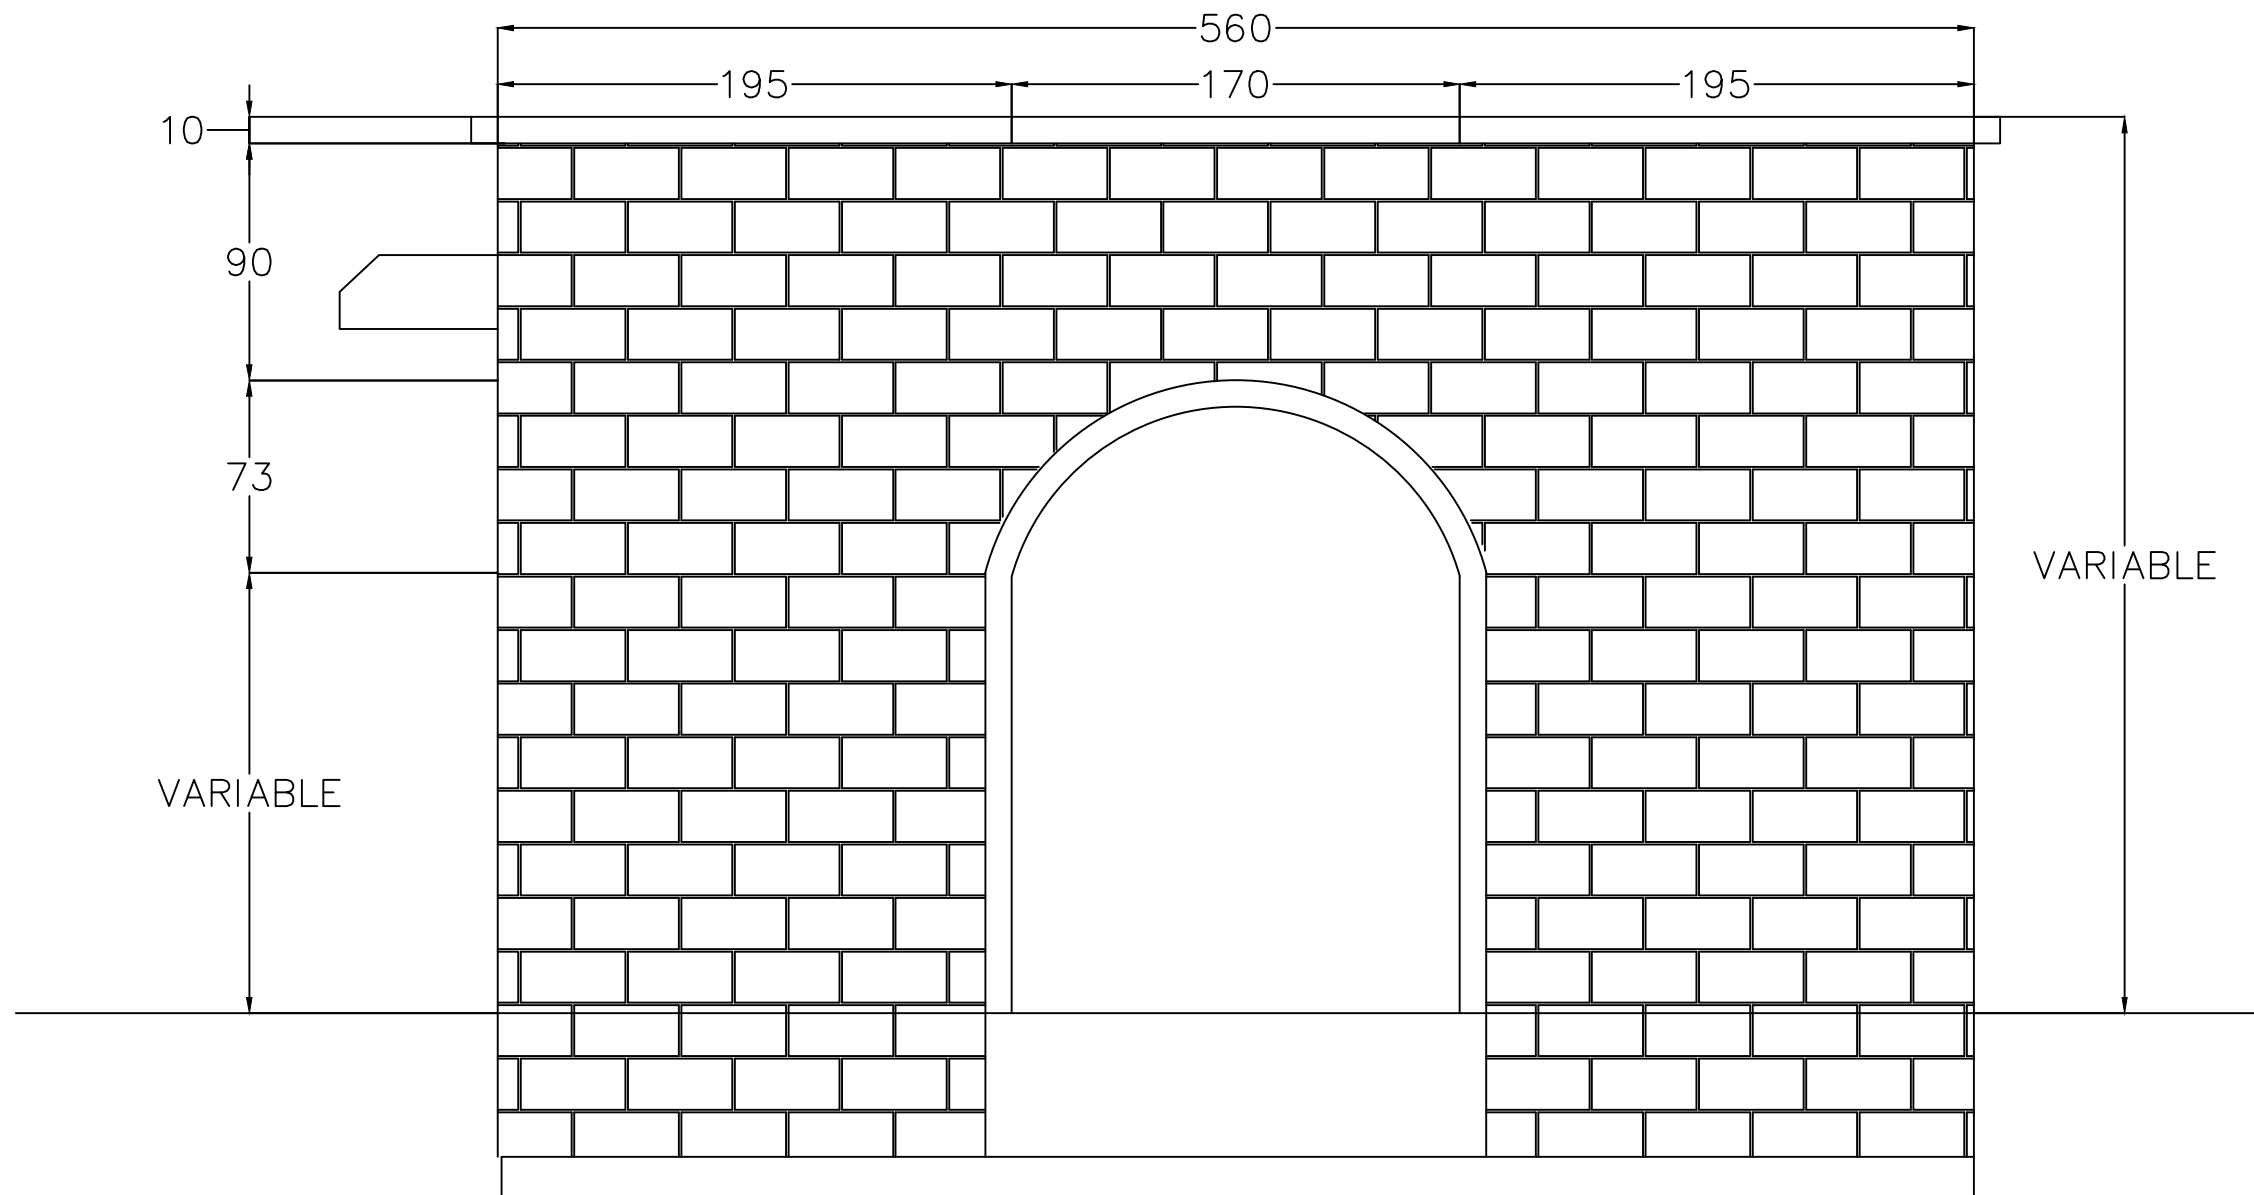


ESTRUCTURA DE PÓRTICO PR-01
ALZADO

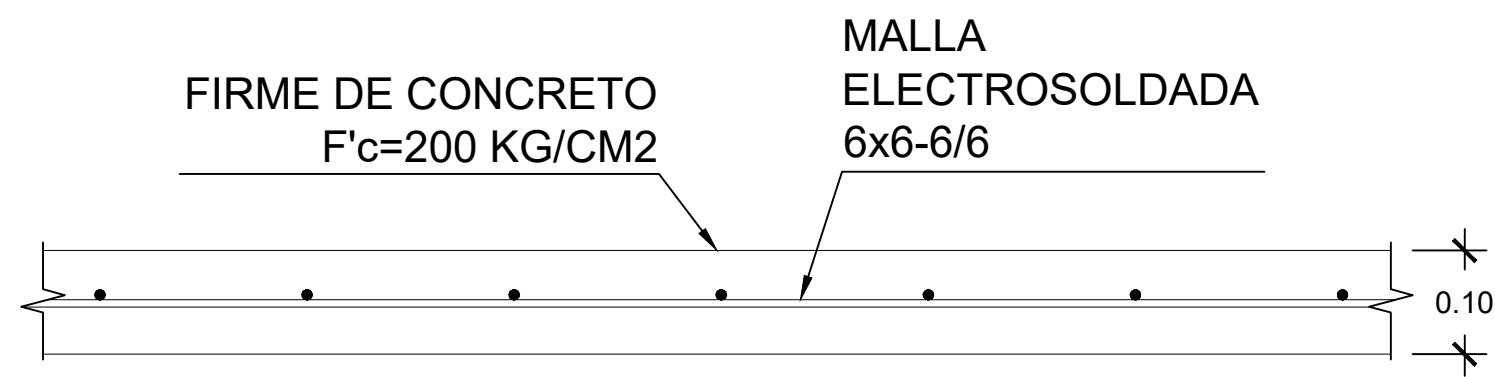


ARMADO DE FIRME DE CONCRETO
ALZADO
ESCALA 1:10

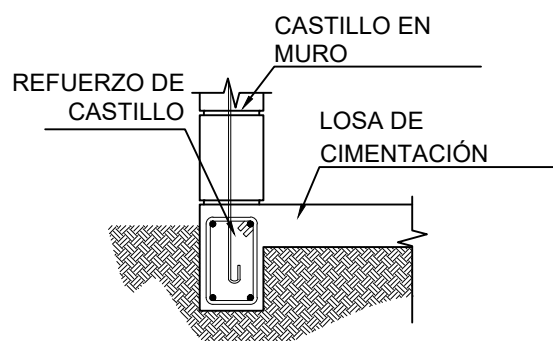


ANCLAJE DE REFUERZO DE MUROS
ALZADO

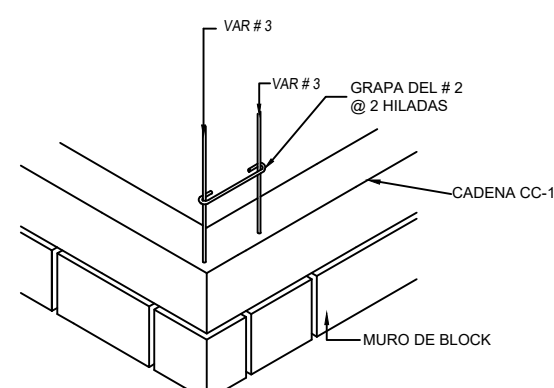

DETALLE DE ANCLAJE DE
CASTILLO EN ESQUINA O INTERSECCIÓN
ISOMETRICO-ESCALA 1:20

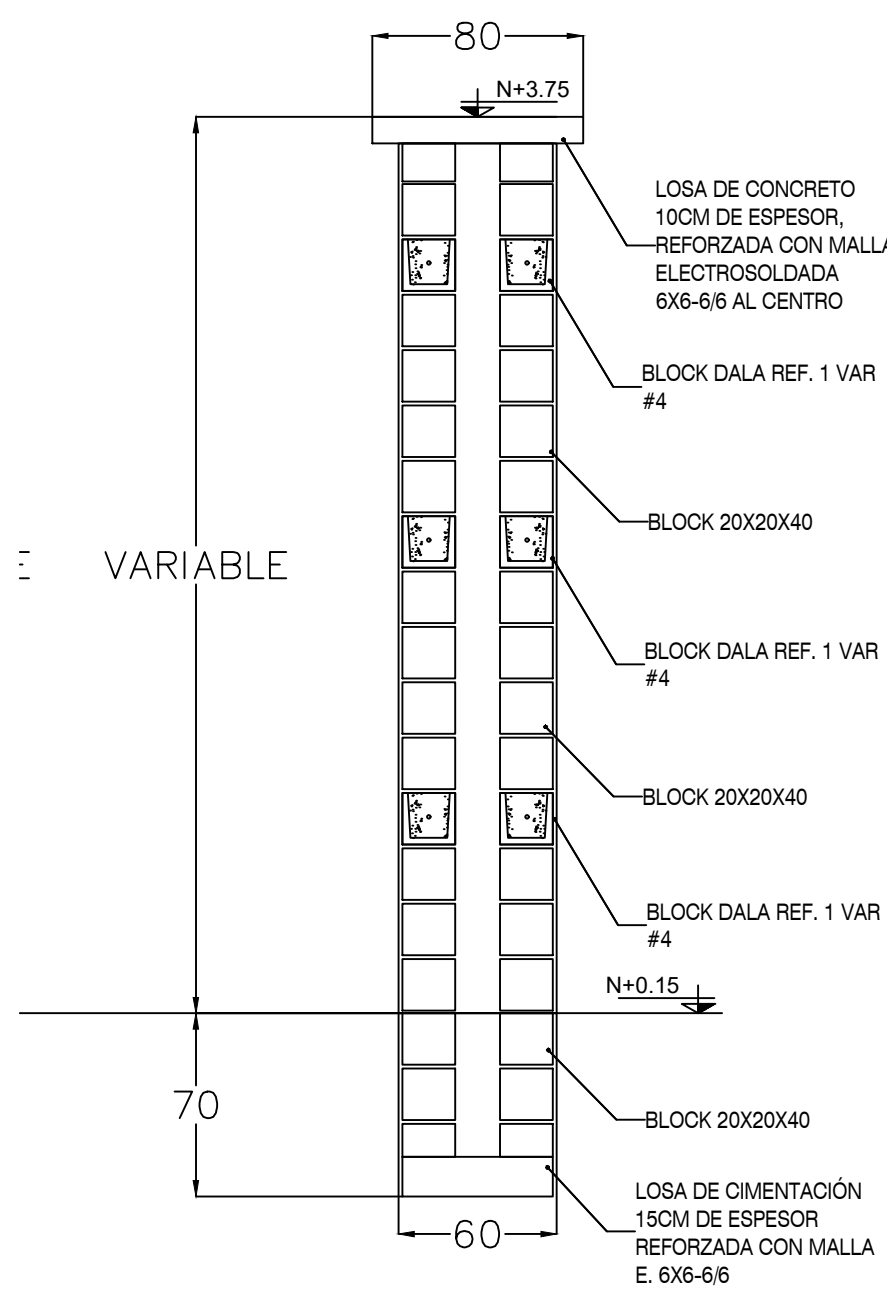


CORTE ESTRUCTURA DE PÓRTICO PR-01.
ALZADO

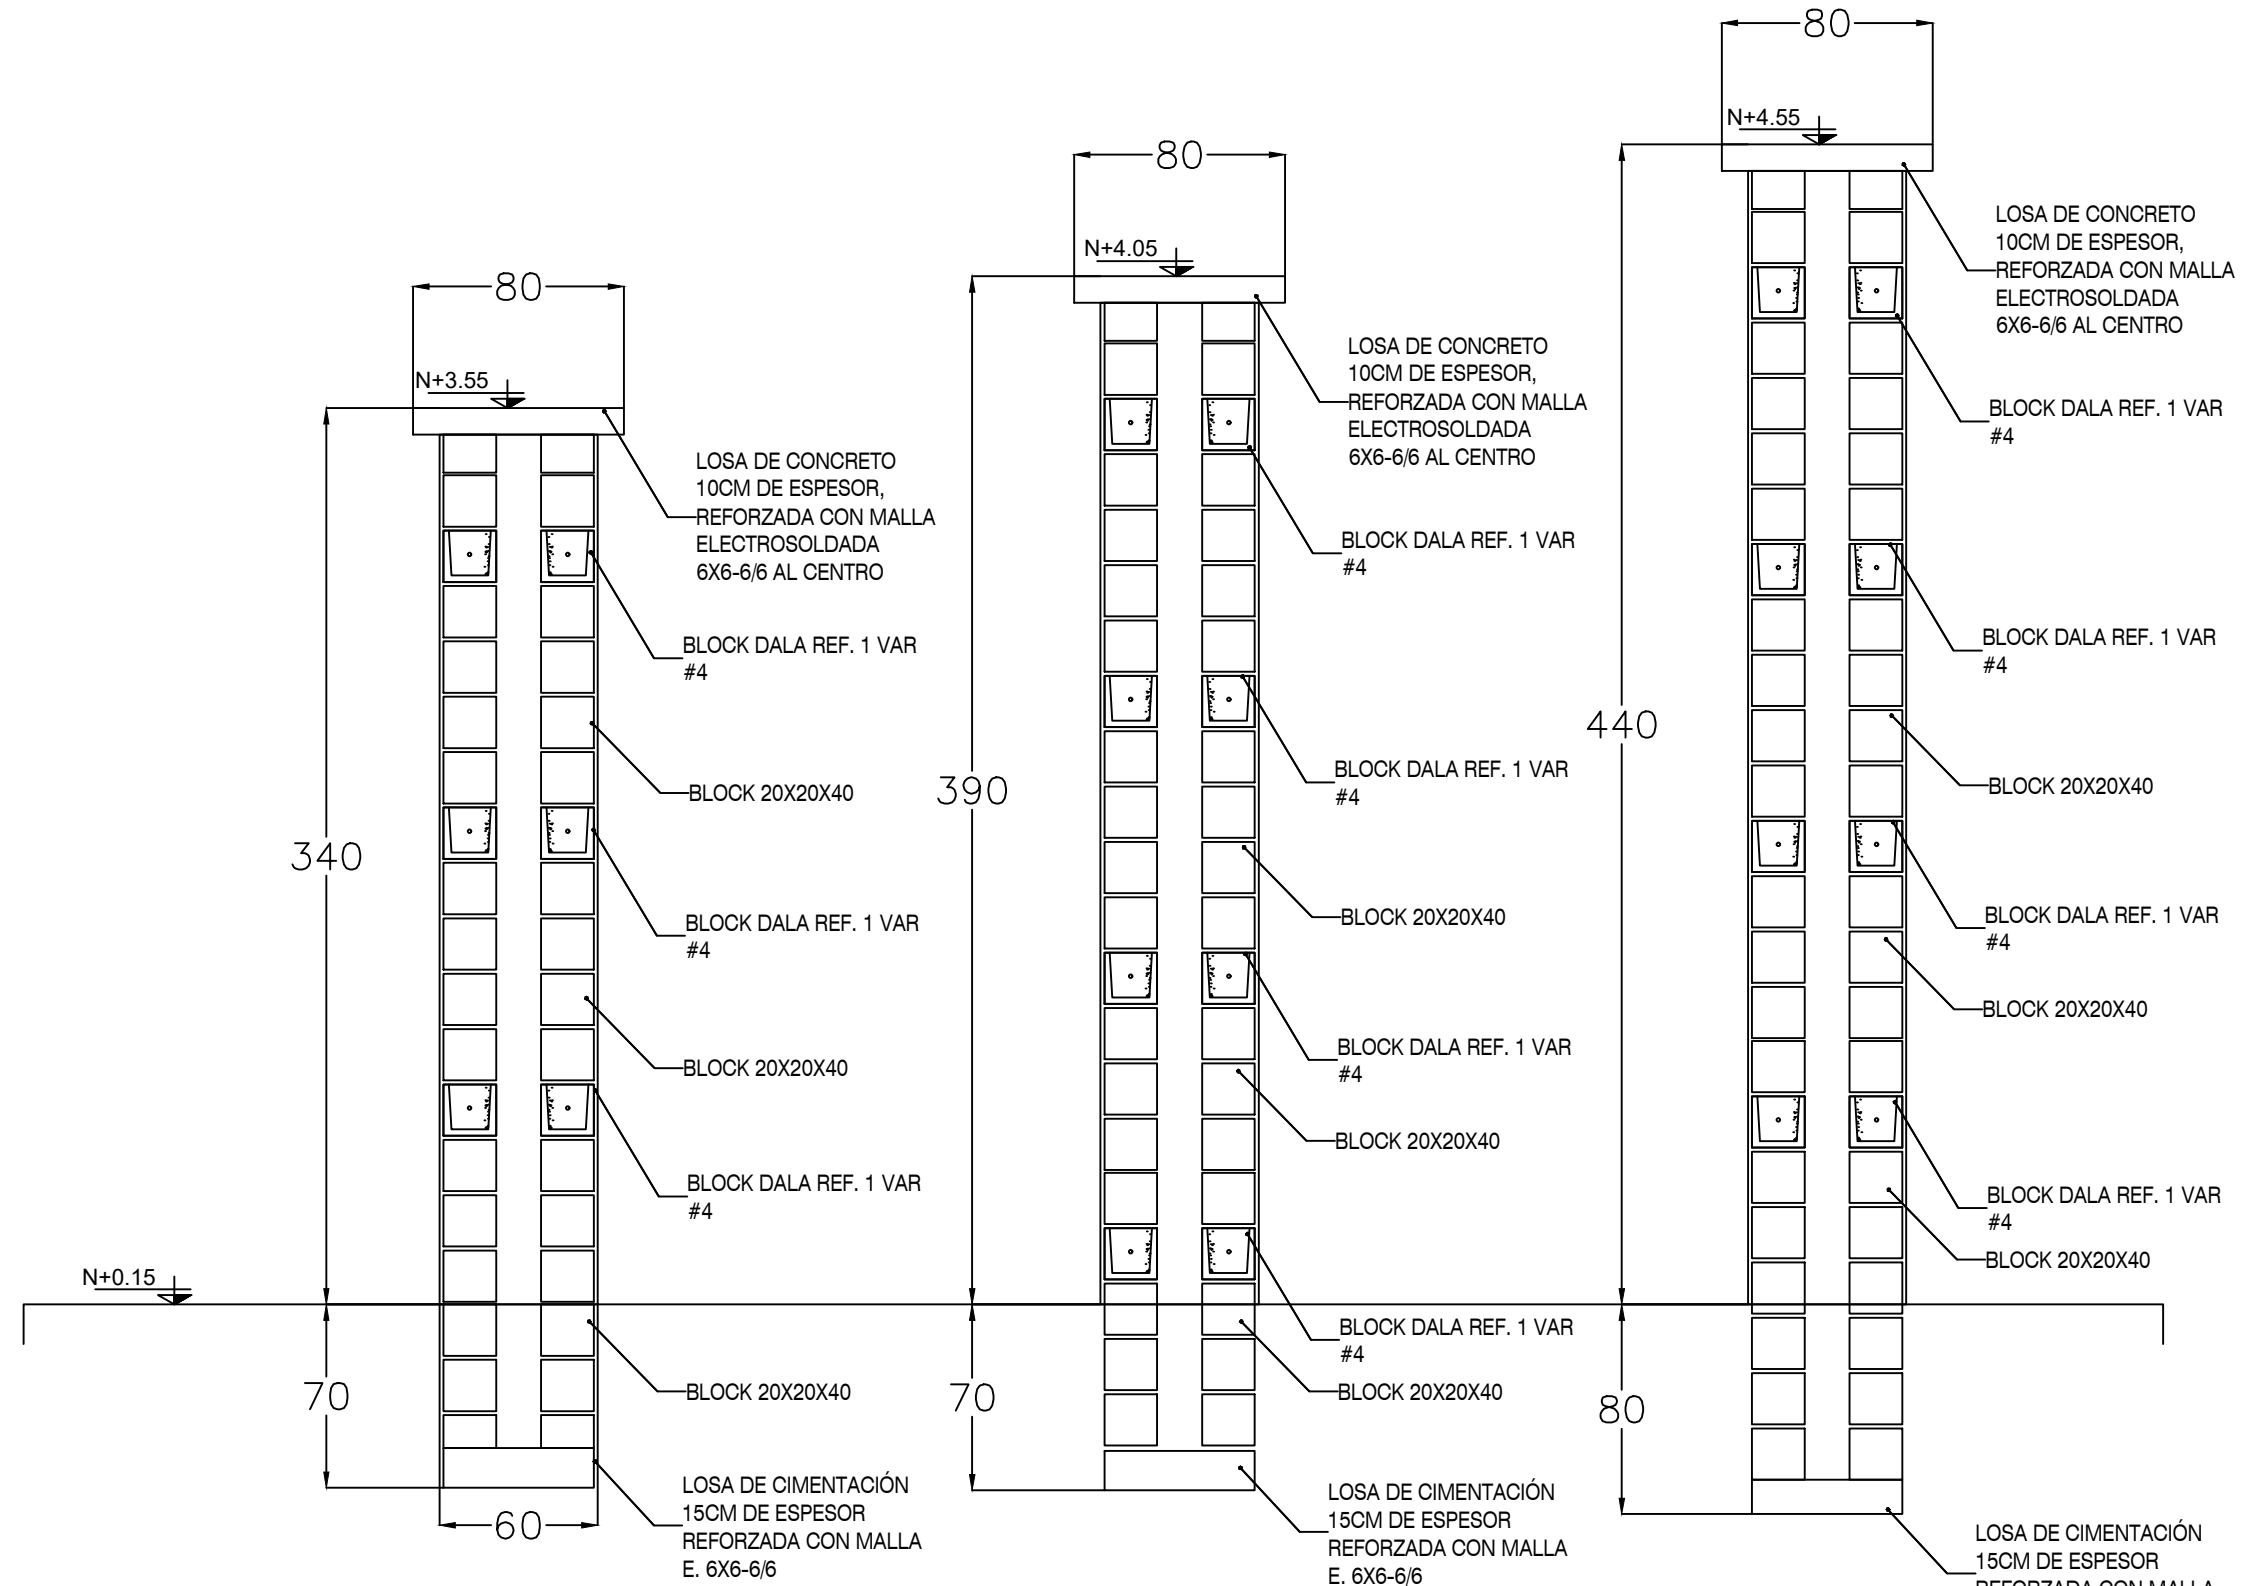


CORTE ESTRUCTURA DE PÓRTICO PR-01A, PR-01B Y PR-01C.
ALZADO

DETALLES DE REFUERZO											
FY=4,200 KG/CM2											
#	φ	AREA	L1	L2	L3	L4	rb	re	Ld	Lt	Lg
3	0.95	0.71	11	10	7	4	3	2	38	53	15
4	1.27	1.27	15	12	7	5	4	3	51	84	15

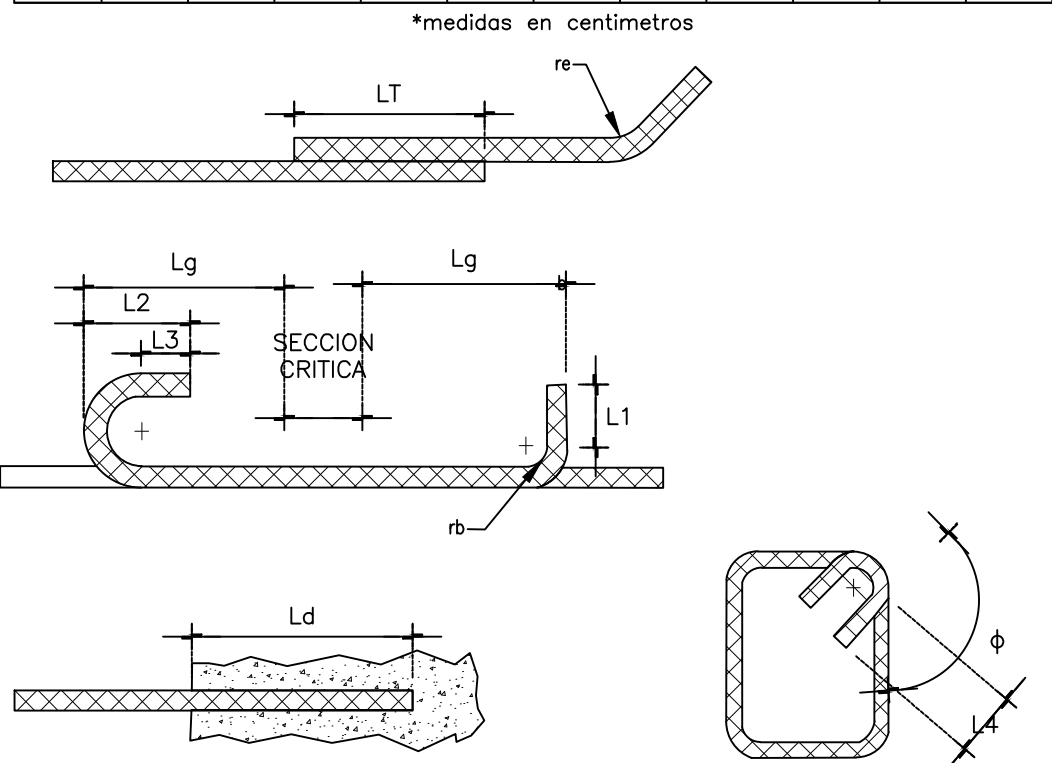

SIMBOLOGIA O ABREVIACIONES	
#	Numero de varilla
rb	Radio del dobles de la barra.
re	Radio del dobles del estribo.
Ld	Longitud de desarrollo.
Lt	Longitud de translope
Lg	Longitud del gancho.

- Notas:
- Longitudes segun ACI-318-19
 - Longitudes para acero corrugado, para acero liso multiplicar por 1.9
 - Para concreto peso normal (2400 kg/m³)
 - Para la varilla recta o en rollo con una fy=4200 kg/cm².
 - La separación de los empalmes debe ser 60 cm como minimo (ACI 12.15.5.1)

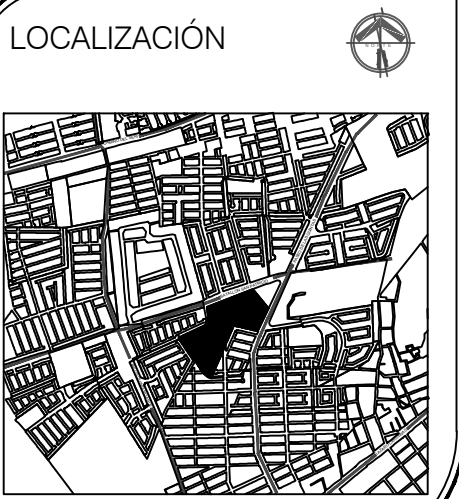

REVISIONES

NOTAS Y ESPECIFICACIONES.

RESPONSABLES

RESPONSABLE DE DISEÑO ARQUITECTÓNICO:

ARO. FRANCISCA ELIZABETH FLORES GARCIA

PROPIETARIO:

R.L. ING. ADRIAN CASTRO GUERRERO

DIRECTOR RESPONSABLE DE OBRA:

ING. RAFAEL MONDRAGON GARCIA

PROPIETARIO:

DESARROLLOS RESIDENCIALES
LANDER S. A. DE C. V.

Bulevard Naiman #1116 - Jalisco y Sufragio
CD. OREGÓN, SONORA.
TEL. 413 52 79 413 52 80 413 52 83 fax 413 52 82

ESCALA:	REVISION:
Esc: 1:50	1.0
UBICACIÓN:	FECHA:
E.F.G.	FEB/2026
REVISIÓN:	ADICIONES:
ARO, ELIZABETH FLORES	METROS

PROYECTO:
CASA CLUB MDP NORTE

UBICACIÓN:
MAR DE PLATA
HERMOSILLO, SONORA

CONTENIDO:
ESTRUCTURAL DE
PORTICOS PR-01

PLANO No:
EST - 07

ARCHIVO: 03- ESTRUCTURAL CASA CLUB MDP NORTE 260223.dwg