




ESTRUCTURA DE PÓRTICO PR-02
PLANTA

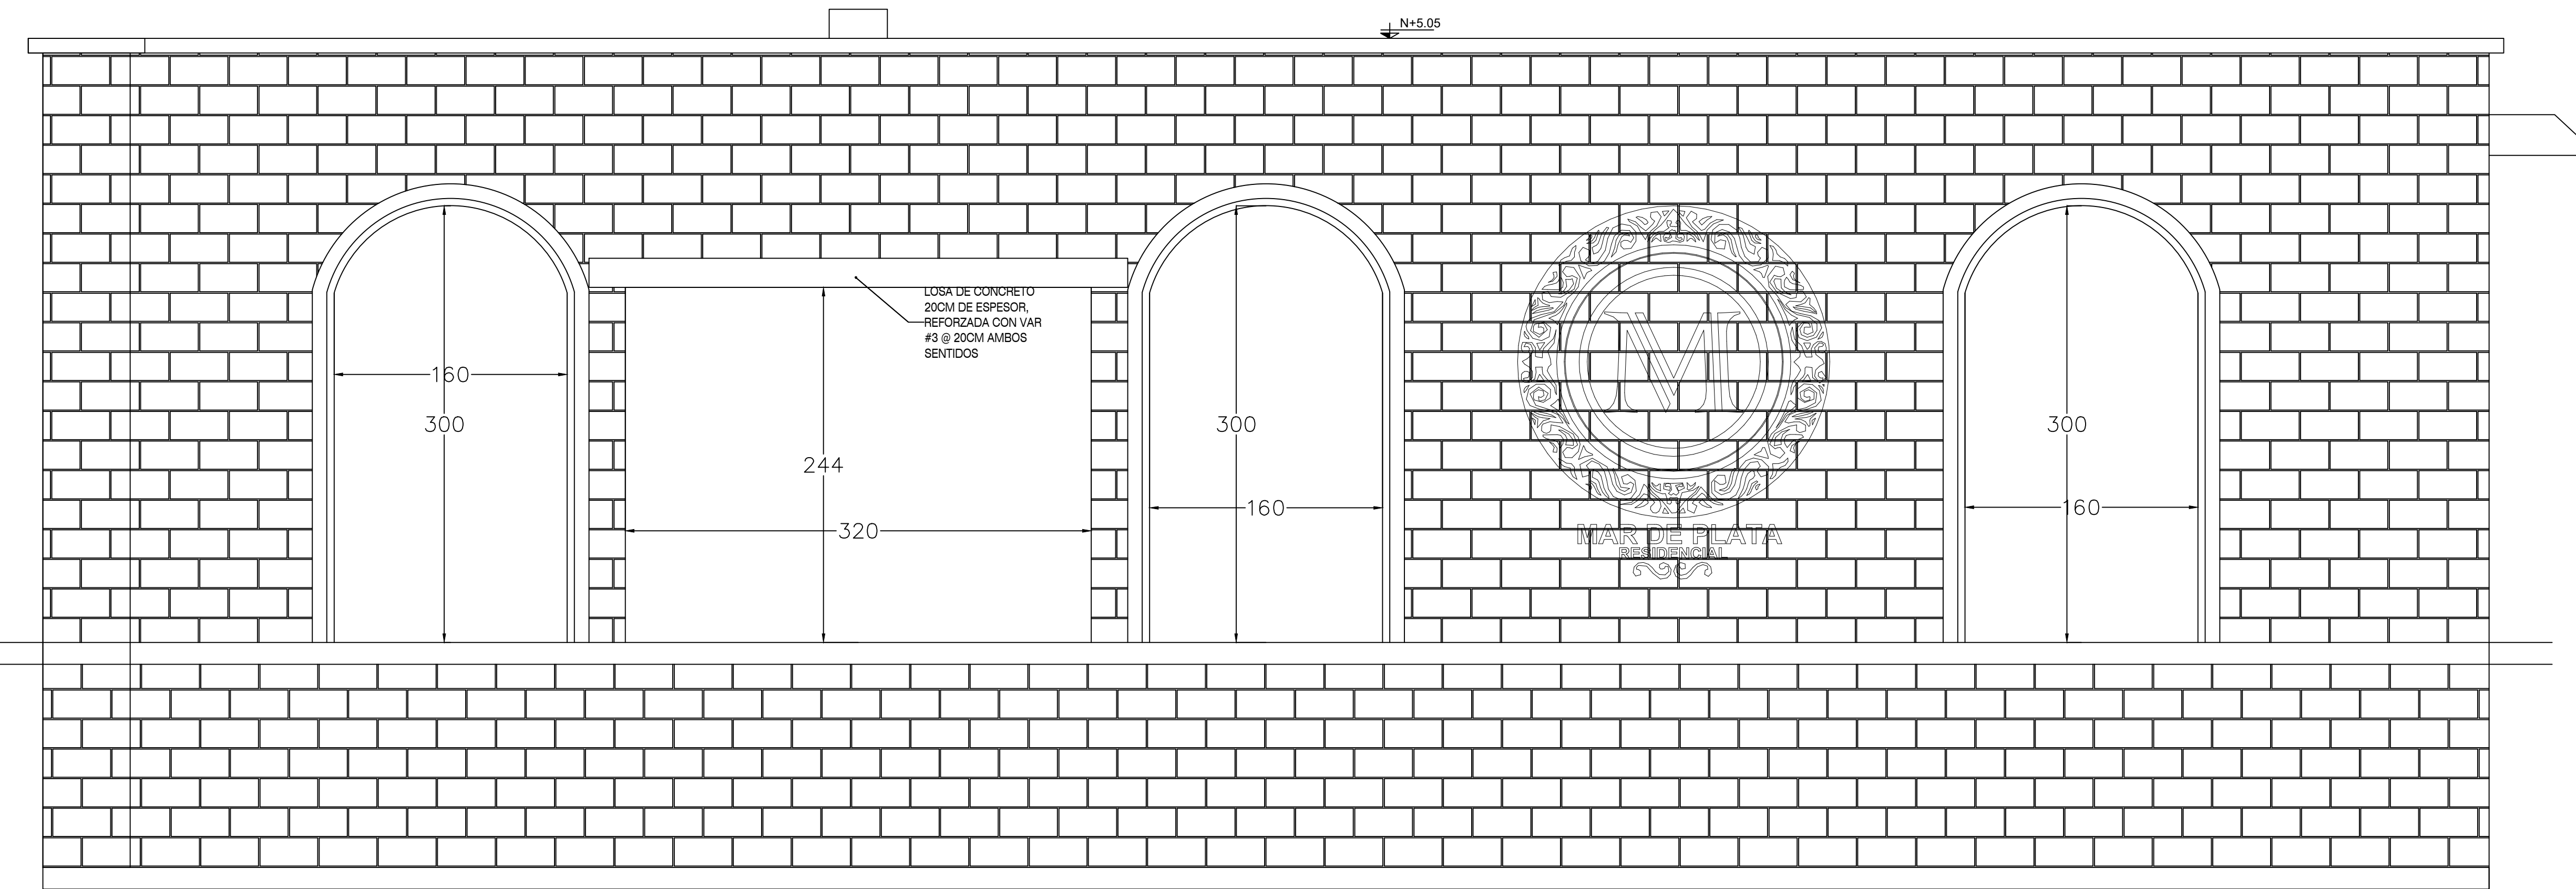


ESTRUCTURA DE PÓRTICO PR-02
ALZADO

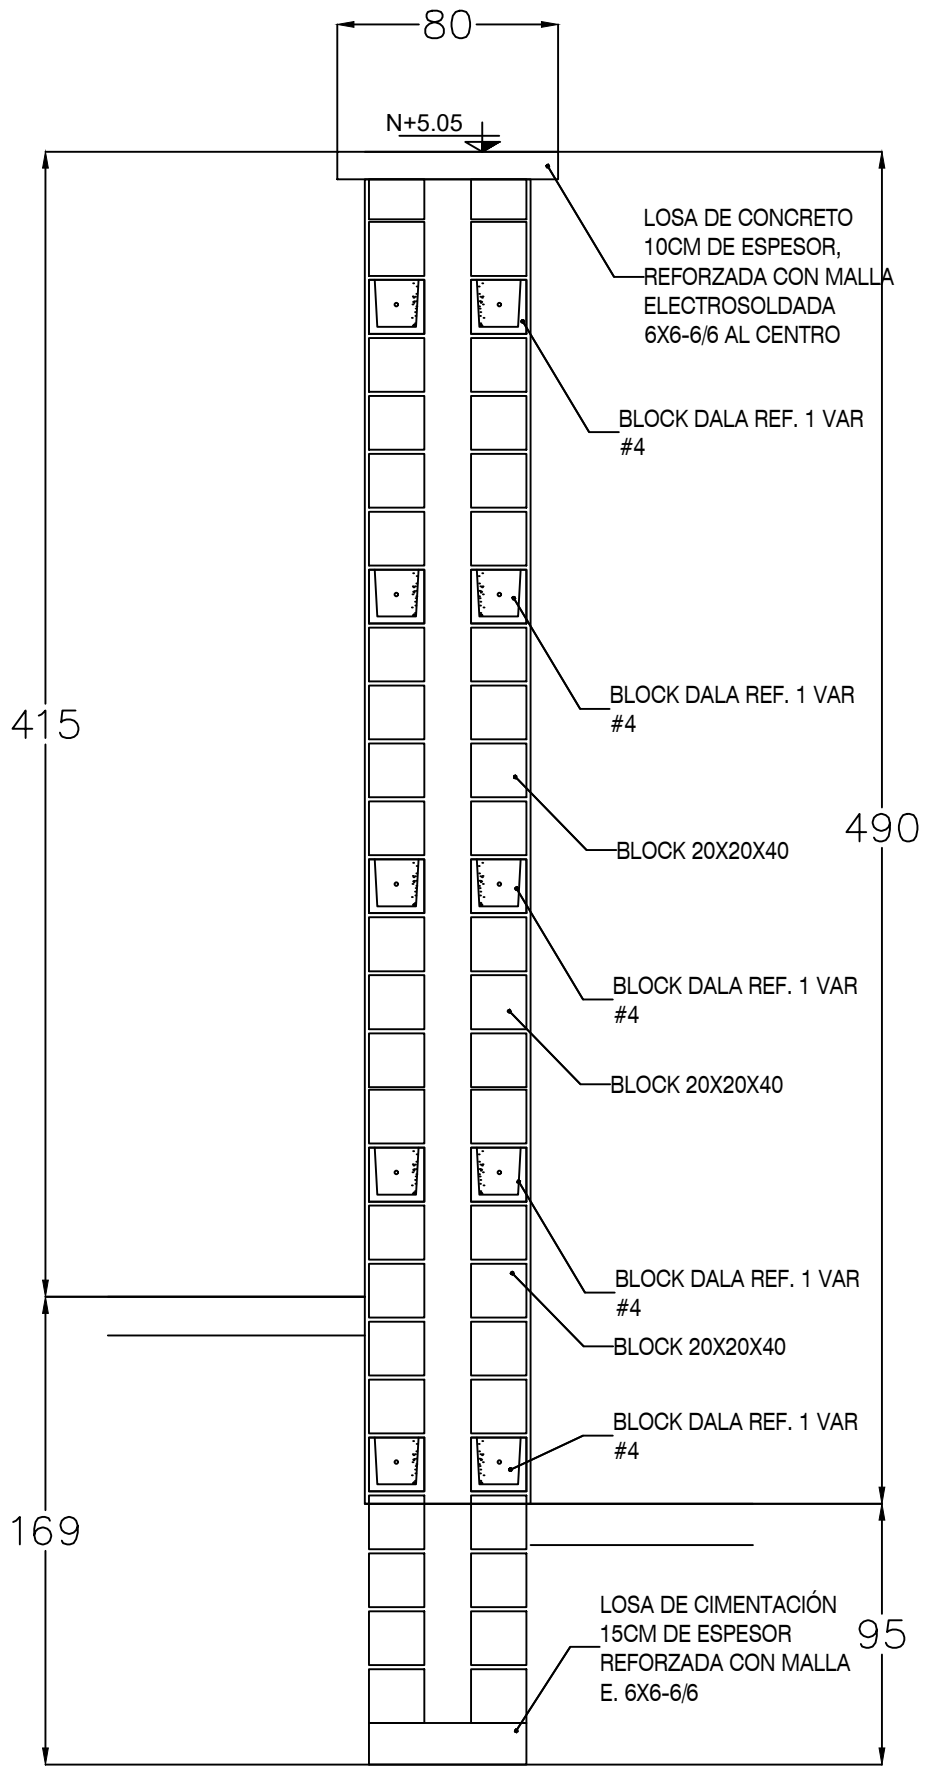


CORTE ESTRUCTURA DE PÓRTICO PR-02, PR-03 Y PR-04
ALZADO

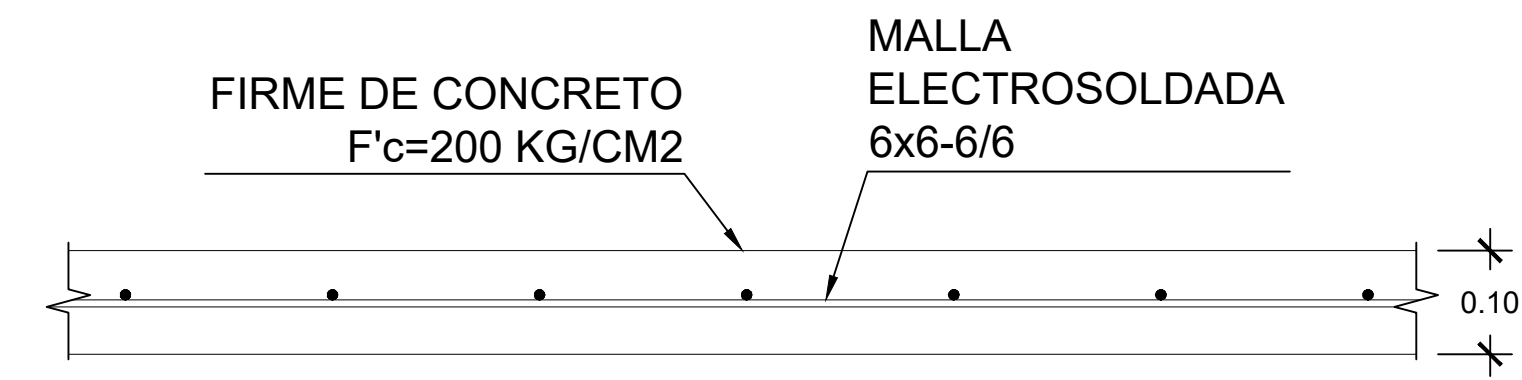


ARMADO DE FIRME DE CONCRETO
ALZADO
ESCALA 1:10

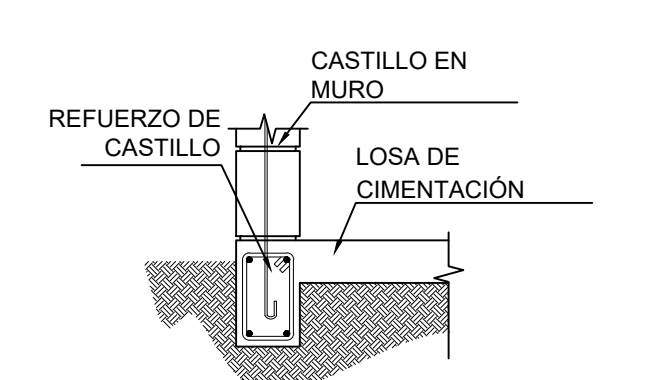


ANCLAJE DE REFUERZO DE MUROS
ALZADO

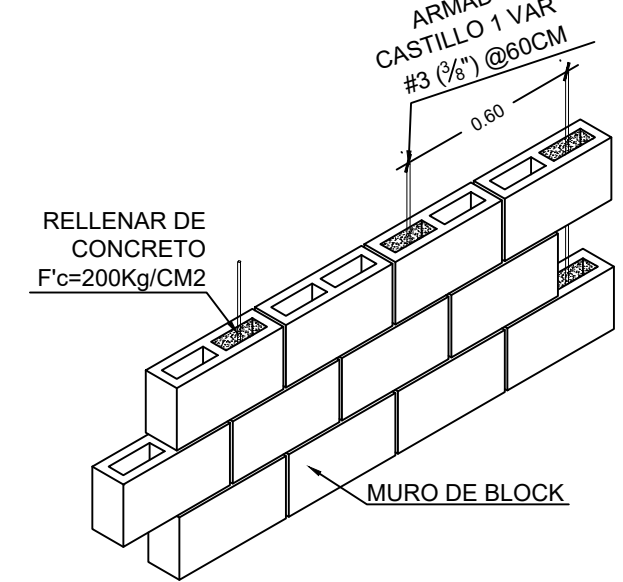


DETALLE TIPO DE REFUERZO PARA MURO DE BLOCK
ISOMETRICO
ESCALA 1:20

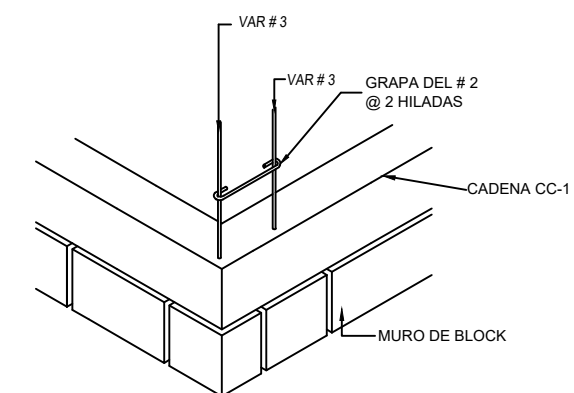


DETALLE DE ANCLAJE DE
CASTILLO EN ESQUINA O INTERSECCIÓN
ISOMETRICO-ESCALA 1:20

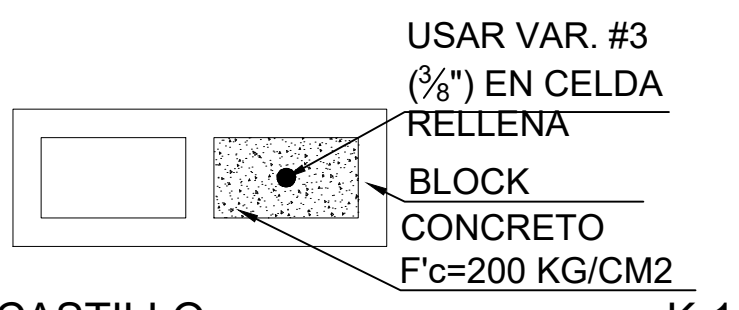

CASTILLO
PLANTA
ESC. 1:10

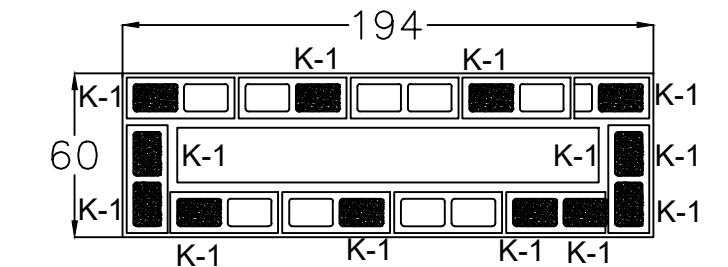

ESTRUCTURA DE PÓRTICO PR-03
PLANTA

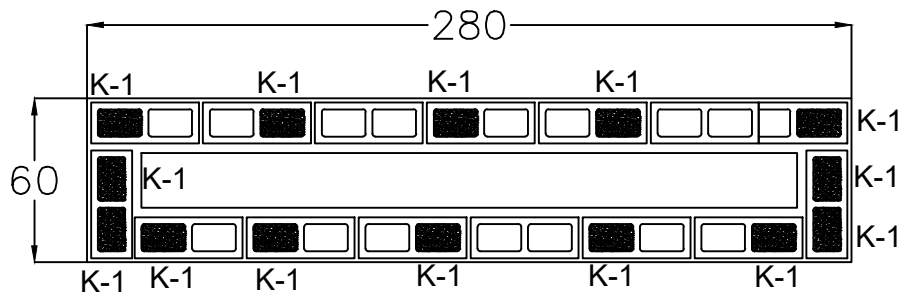

ESTRUCTURA DE PÓRTICO PR-04
PLANTA

LOCALIZACIÓN

LANDER

REVISIONES

NOTAS Y ESPECIFICACIONES

RESPONSABLES

RESPONSABLE DE DISEÑO ARQUITECTÓNICO:

ARQ. FRANCISCA ELIZABETH FLORES GARCIA

PROPIETARIO:

R.L. ING. ADRIAN CASTRO GUERRERO

DIRECTOR RESPONSABLE DE OBRA:

ING. RAFAEL MONDRAGON GARCIA

PROYECTO:

CASA CLUB MDP NORTE

UBICACION:

MAR DE PLATA
HERMOSILLO, SONORA

CONTENIDO:

ESTRUCTURAL DE
PÓRTICOS PR-02, 03 Y 04

PLANO No:

EST - 08

ARCHIVO: 03.-ESTRUCTURAL CASA CLUB MDP NORTE 260223.dwg