




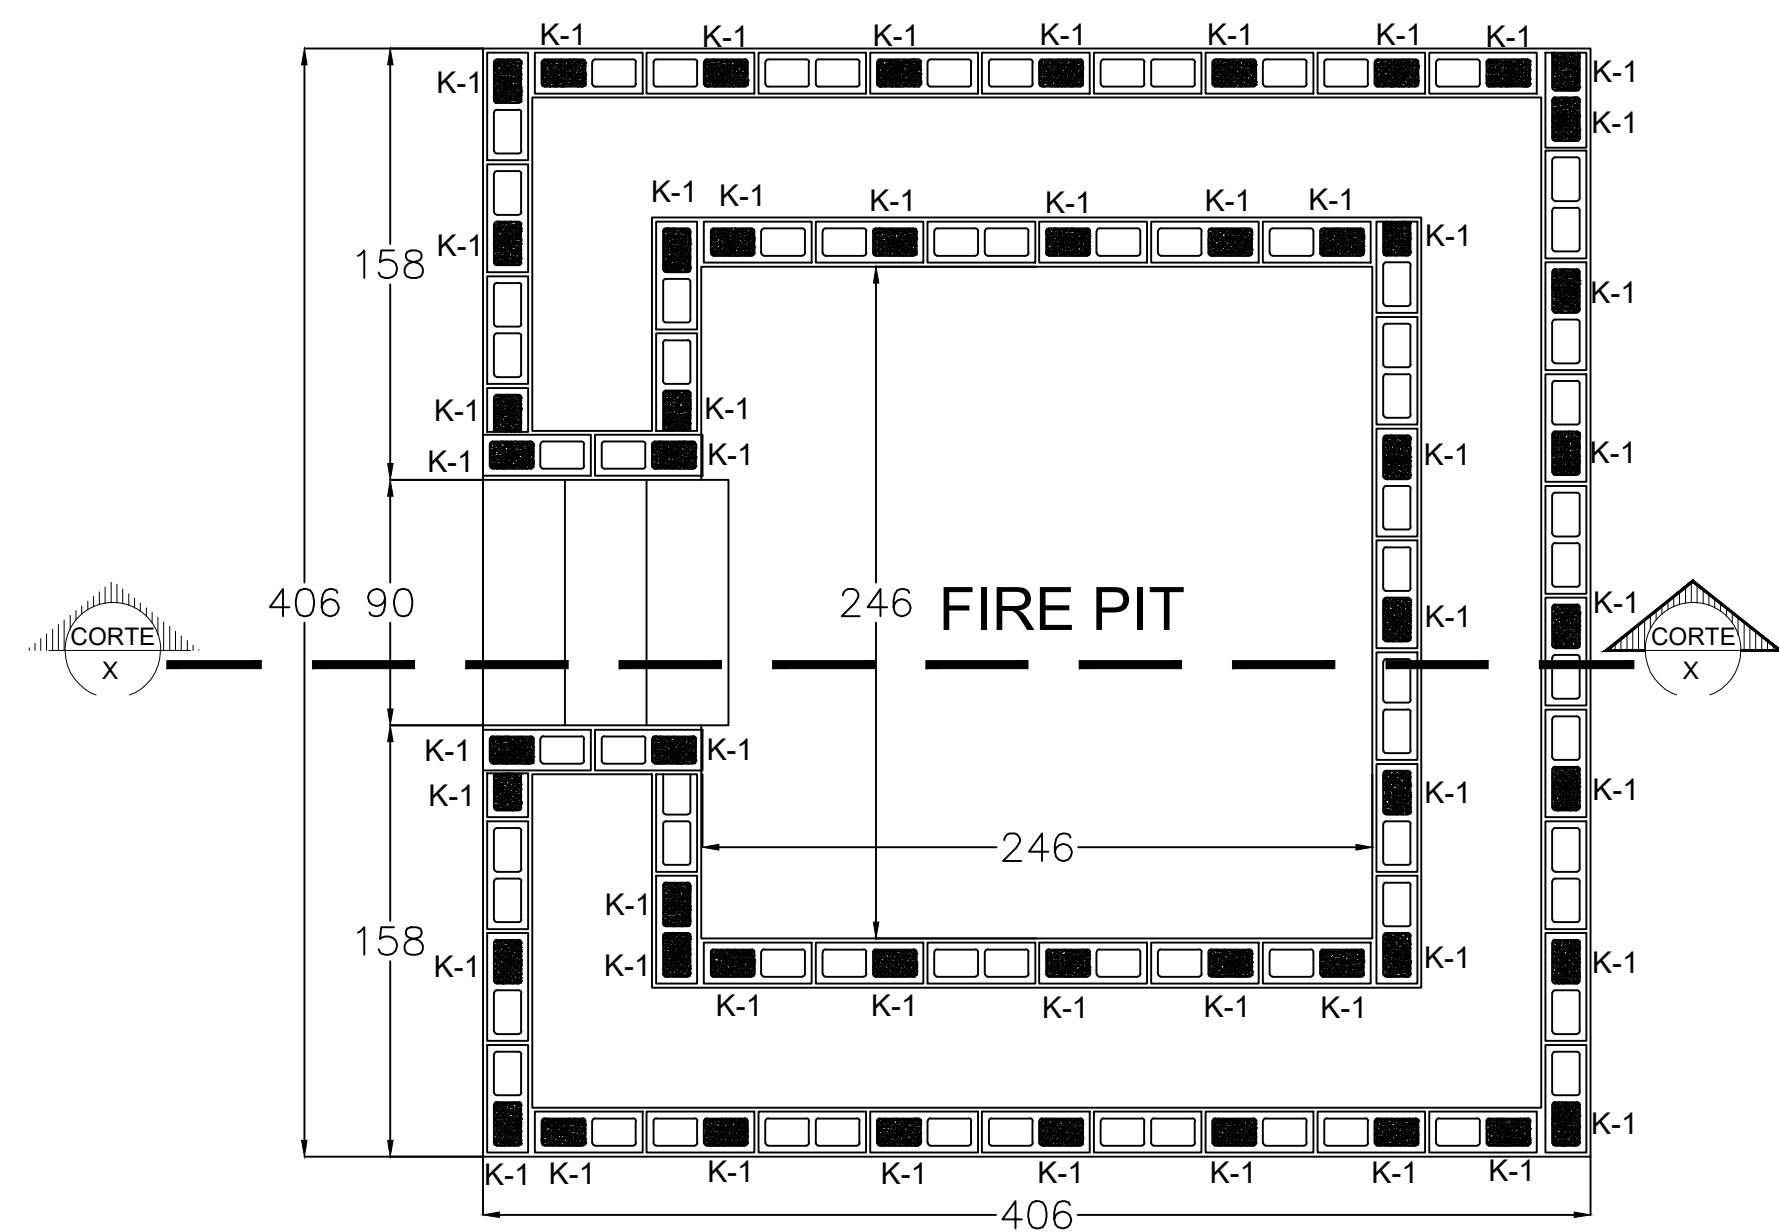


MUROS DE FIRE PIT
PLANTA

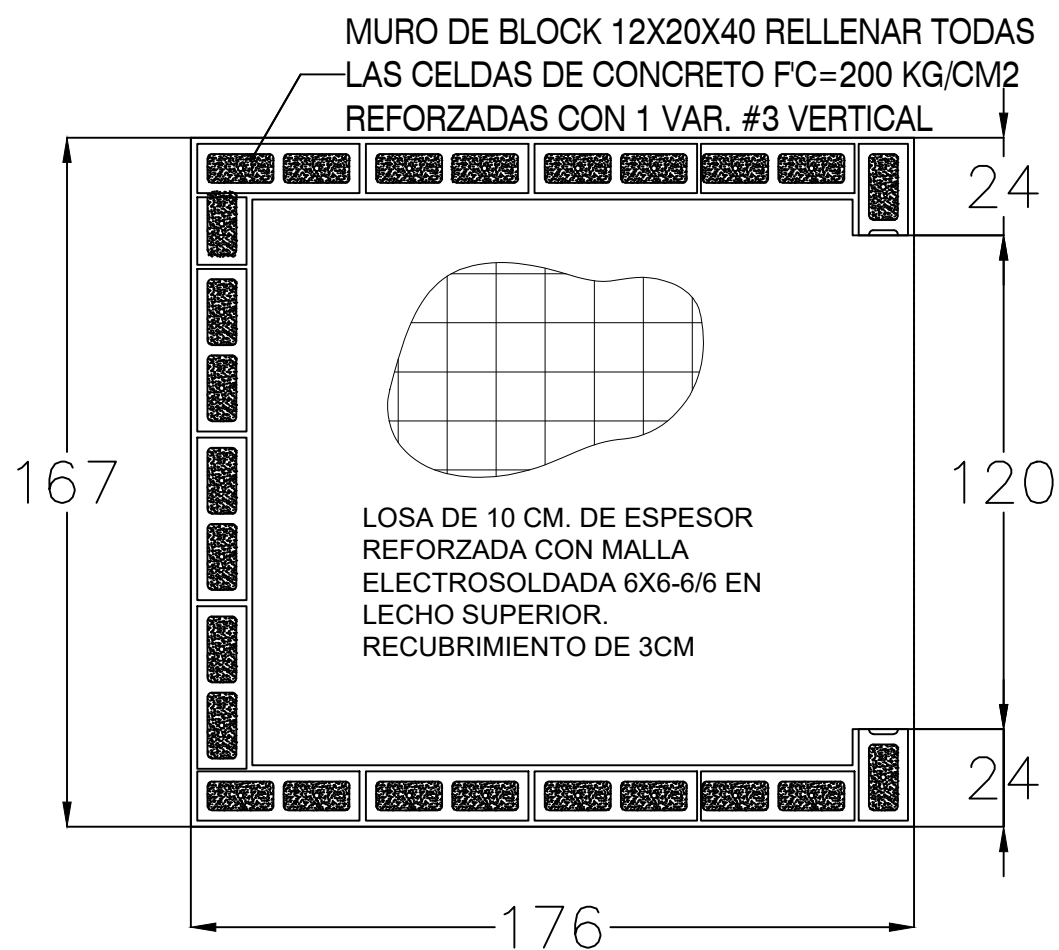


CIMENTACIÓN DE CUARTO DE MÁQUINAS
PLANTA

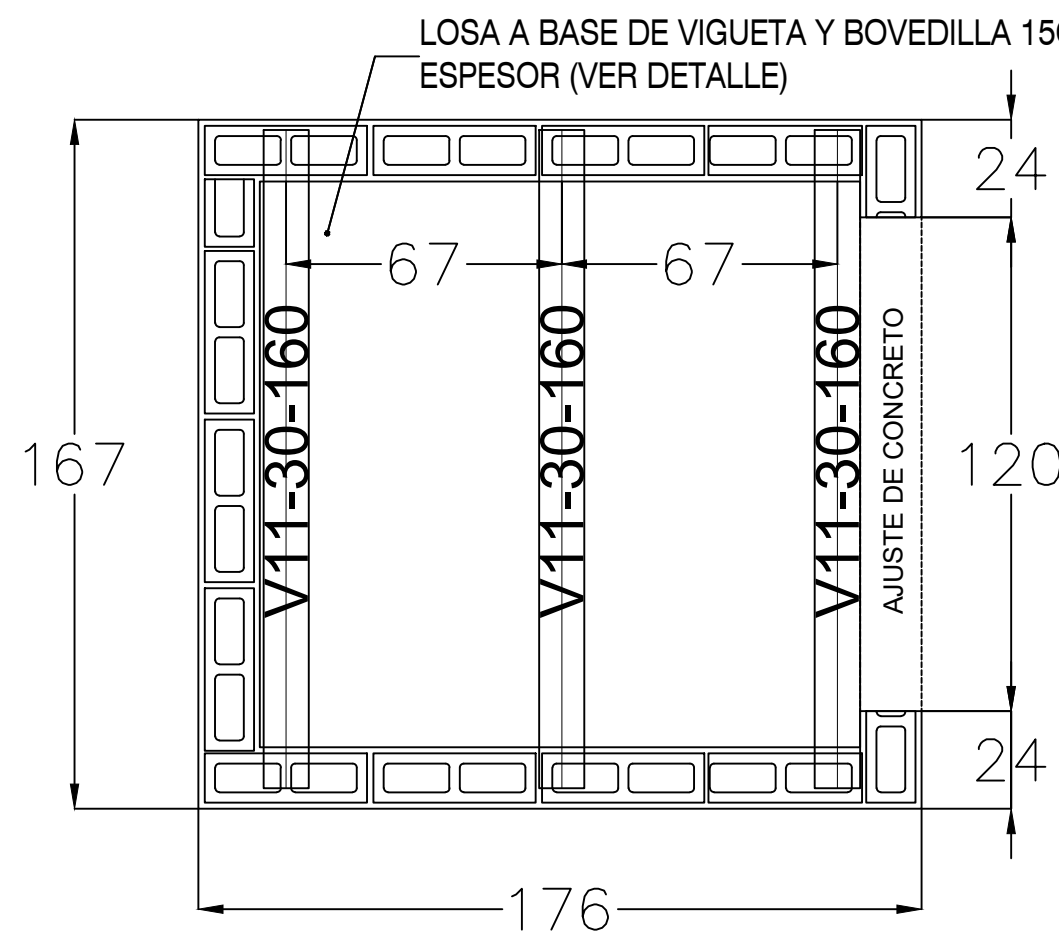


LOSA DE CUARTO DE MÁQUINAS
PLANTA

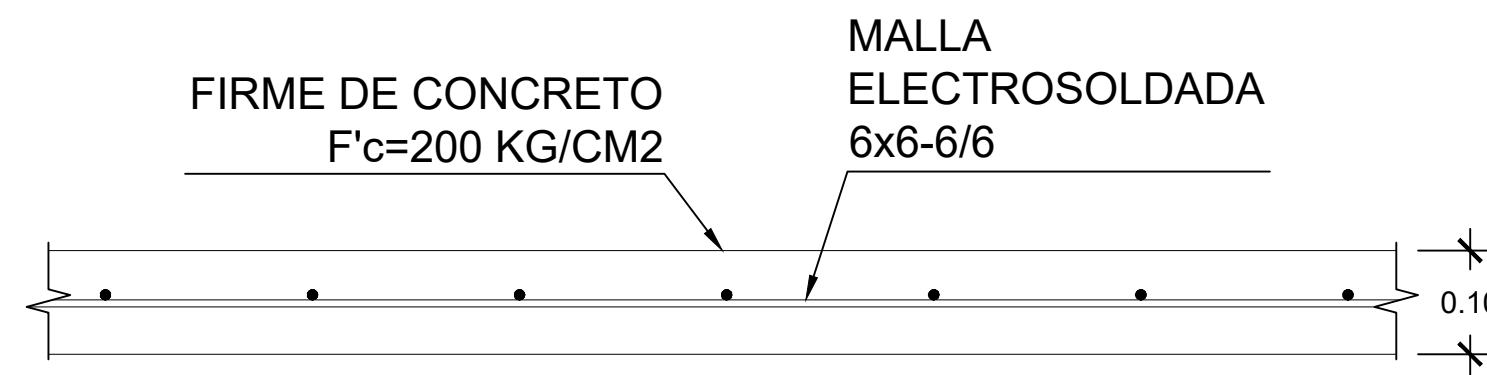


ARMADO DE FIRME DE CONCRETO
ALZADO
ESCALA 1:10

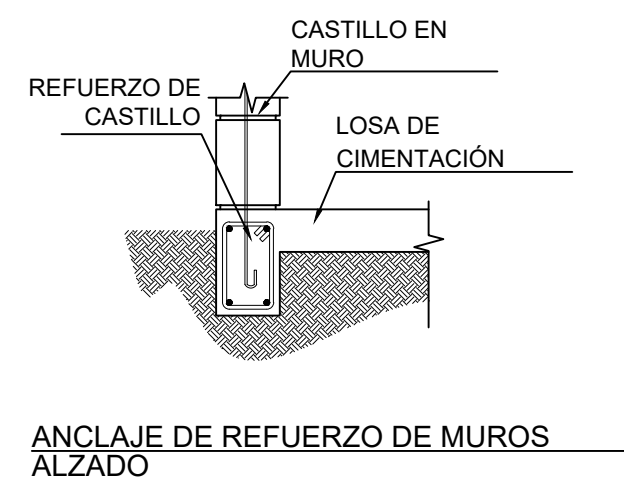


ANCLAJE DE REFUERZO DE MUROS
ALZADO

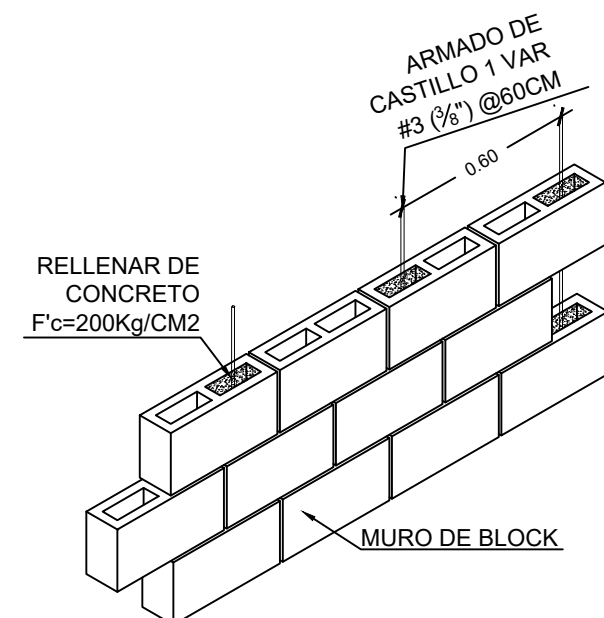


DETALLE TIPO DE REFUERZO PARA MURO DE BLOCK
ISOMETRICO
ESCALA 1:20

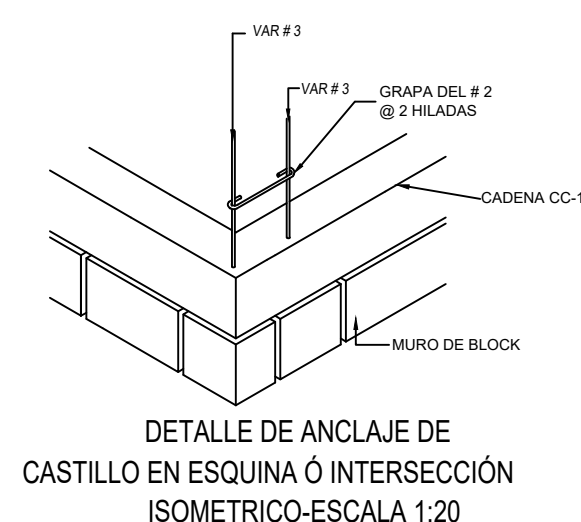


DETALLE DE ANCLAJE DE
CASTILLO EN ESQUINA O INTERSECCIÓN
ISOMETRICO-ESCALA 1:20

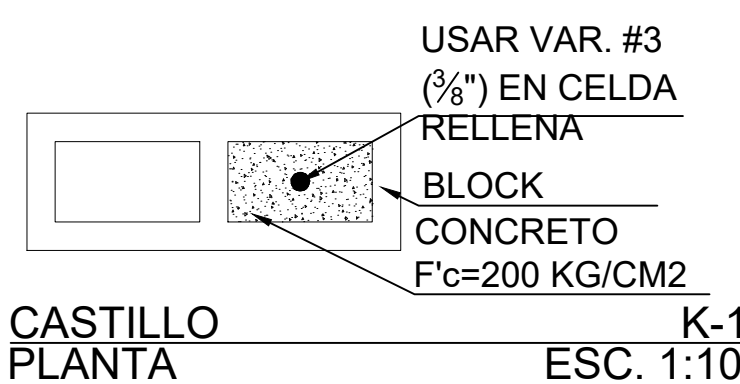



CASTILLO
PLANTA
K-1
ESC. 1:10

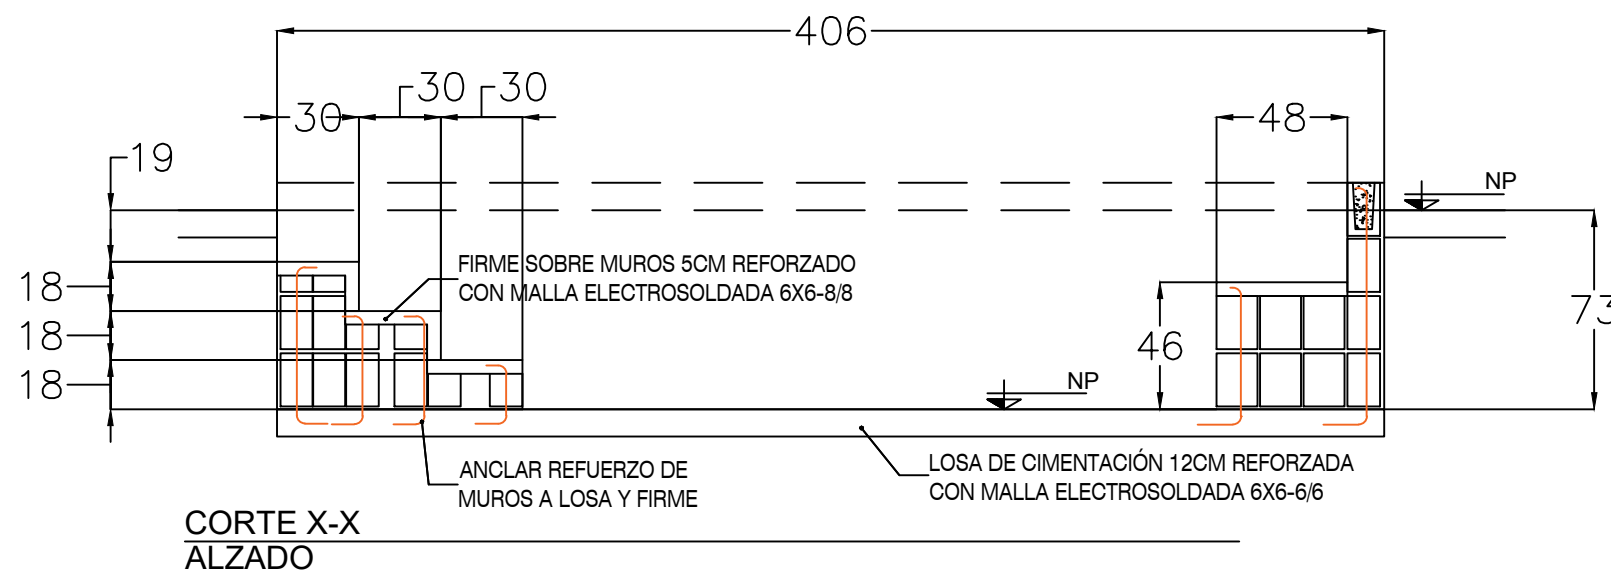


CORTE X-X
ALZADO

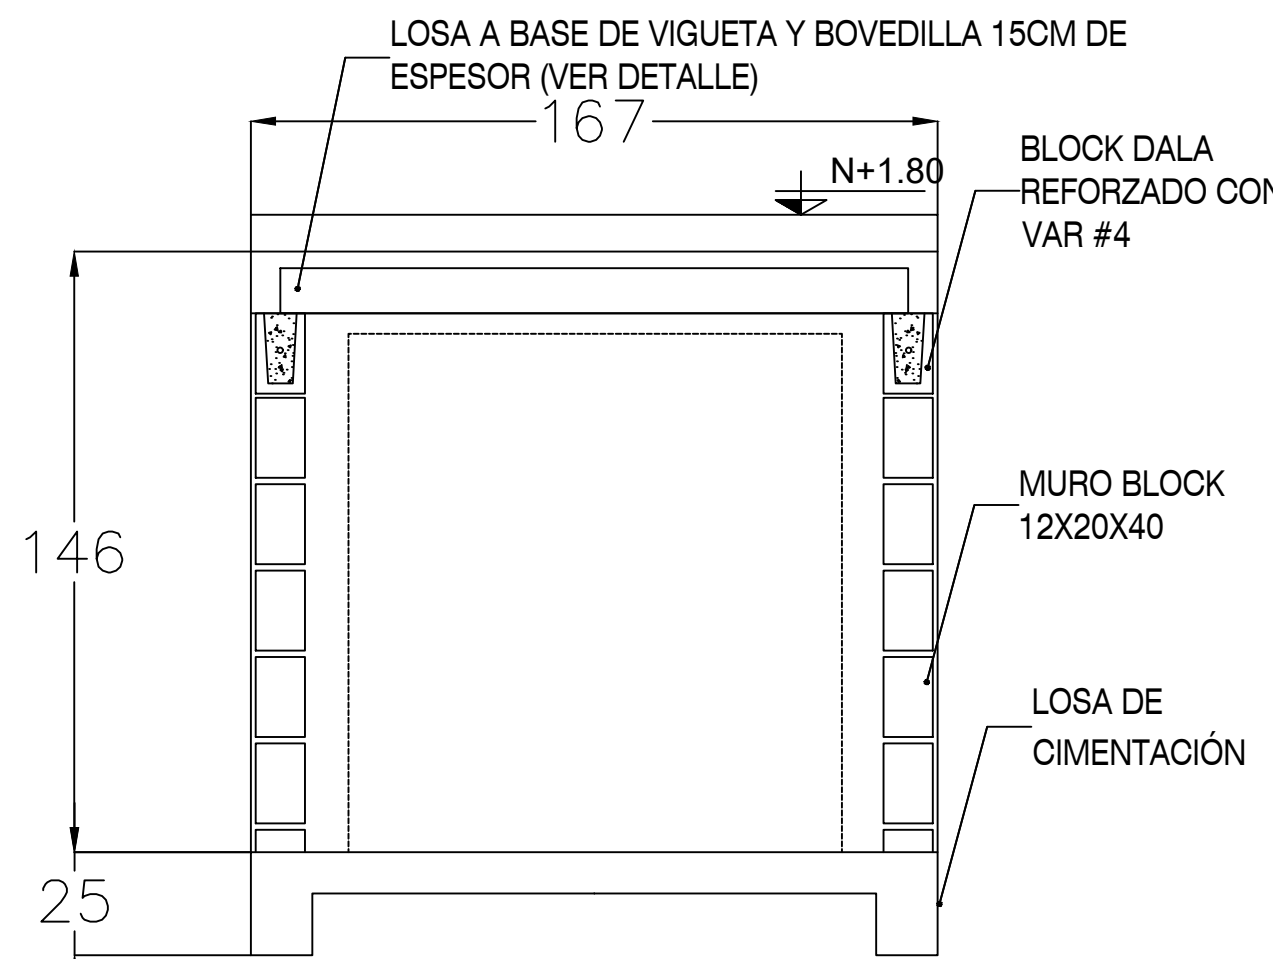


MUROS EN CUARTO DE MÁQUINAS
ALZADO

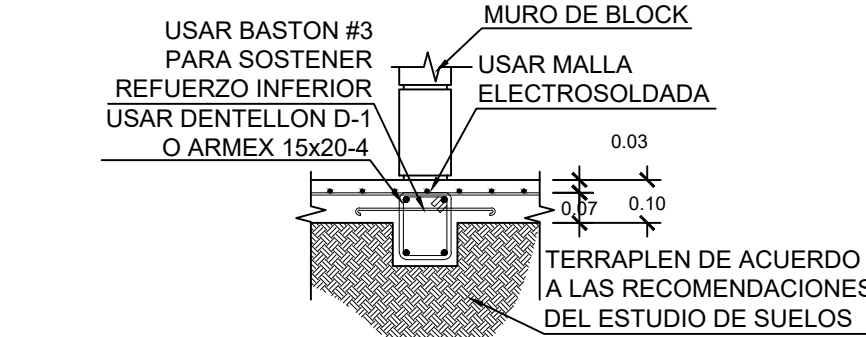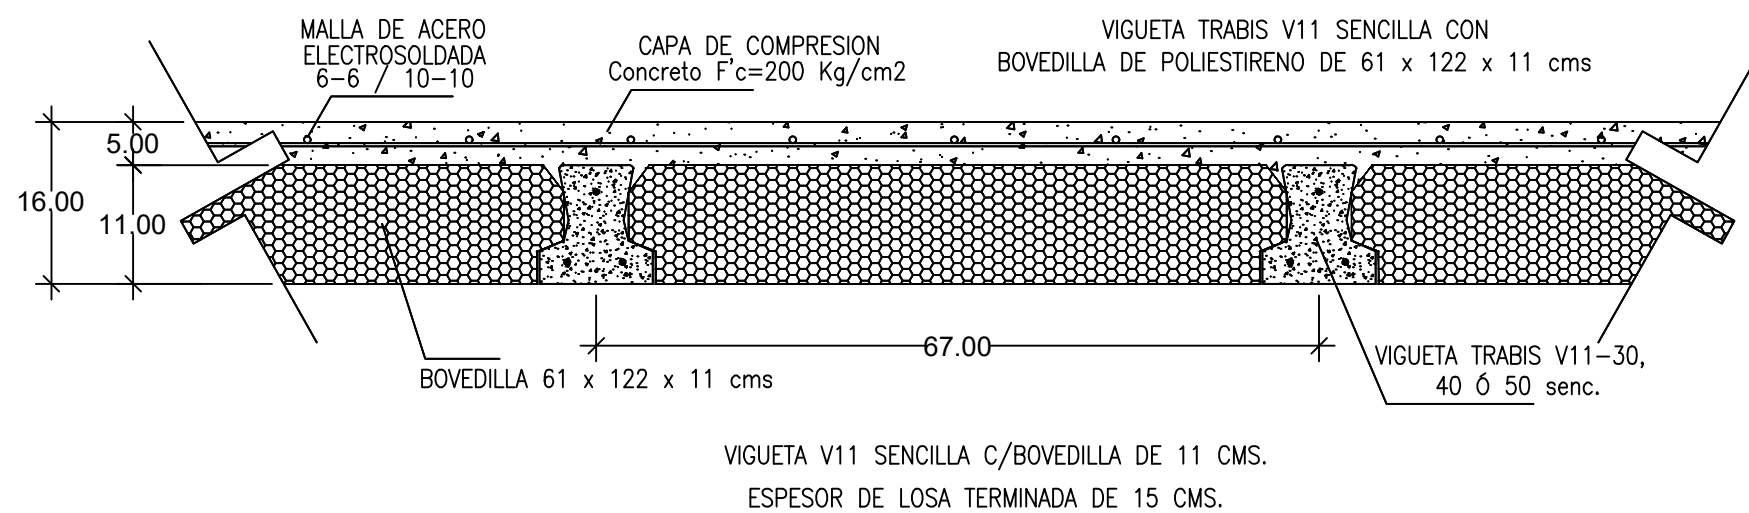


DENTELLON CENTRAL TIPO
ALZADO
DC-1
ESC. 1:15

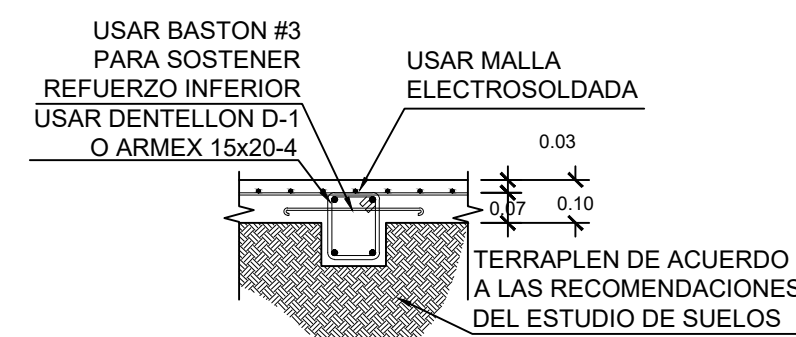


DENTELLON CENTRAL TIPO
ALZADO
DC-2
ESC. 1:15

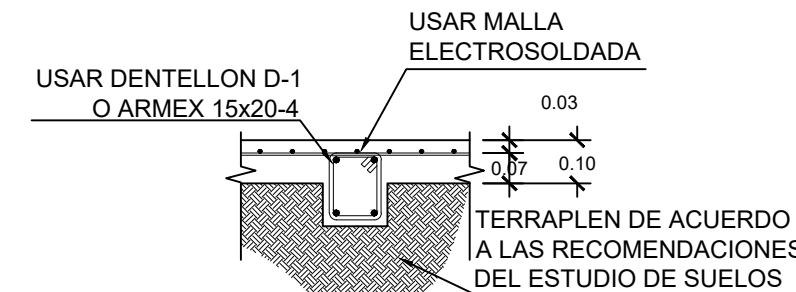


DENTELLON CENTRAL TIPO
ALZADO
DC-3
ESC. 1:15

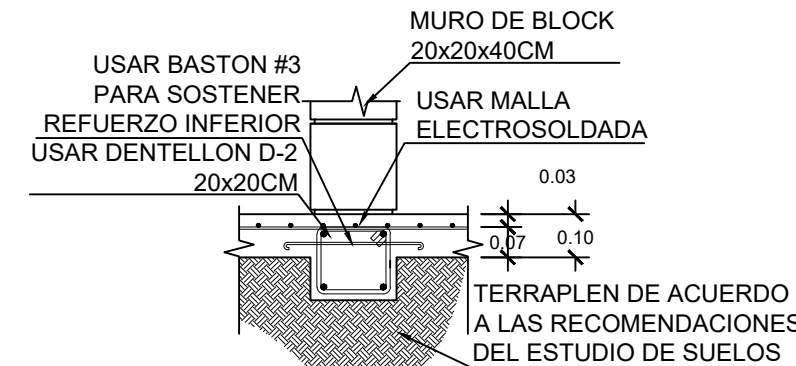


DENTELLON CENTRAL TIPO
ALZADO
DC-4
ESC. 1:15

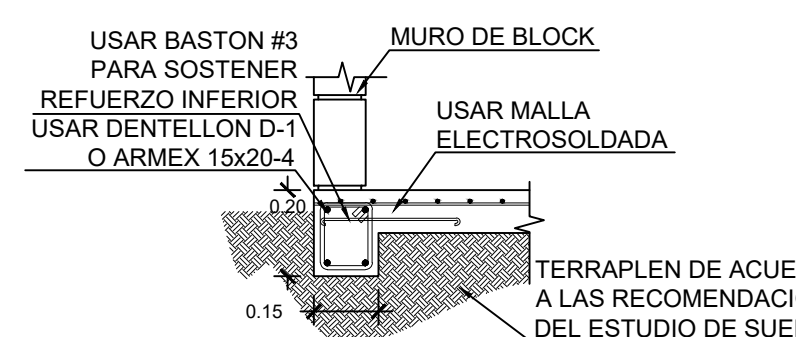


DENTELLON DE LINDERO TIPO
ALZADO
DL-1
ESC. 1:15

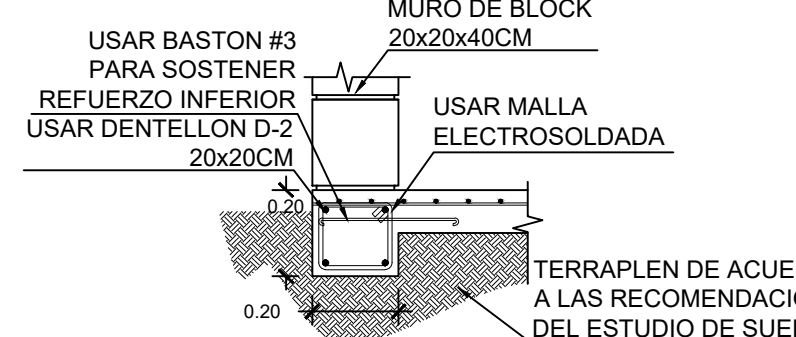


DENTELLON DE LINDERO TIPO
ALZADO
DL-2
ESC. 1:15

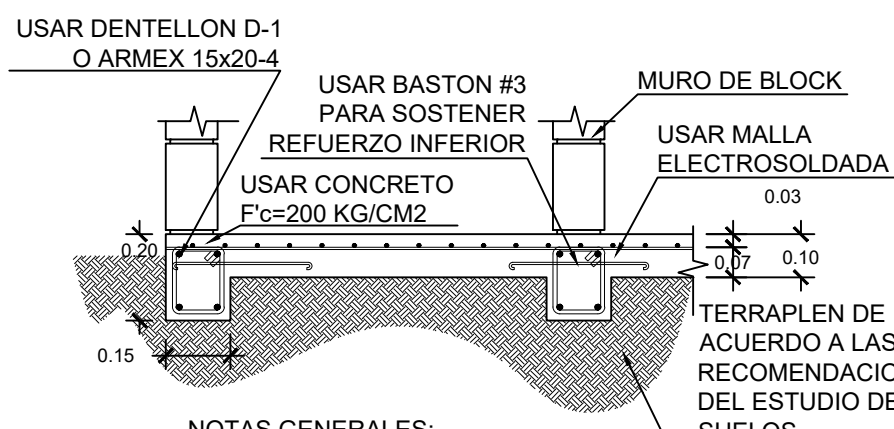

DETALLE DE LOSA DE CIMENTACIÓN TIPO
ALZADO
ESCALA 1:15

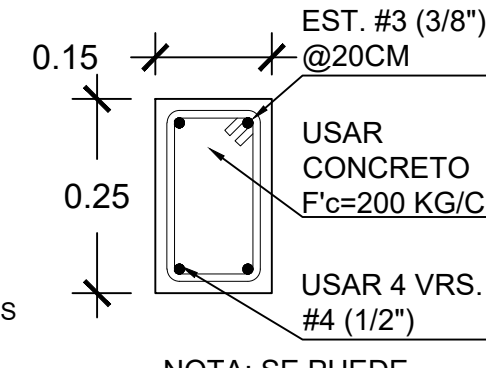


DENTELLON TIPO
ALZADO
D-1
ESC. 1:10

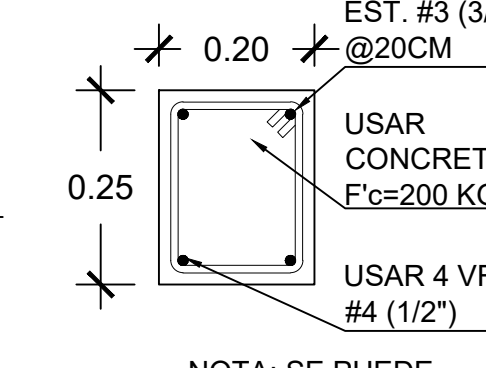


DENTELLON TIPO
ALZADO
D-2
ESC. 1:10



CADENA DE CERRAMIENTO CC-1
ALZADO
ESC. 1:10

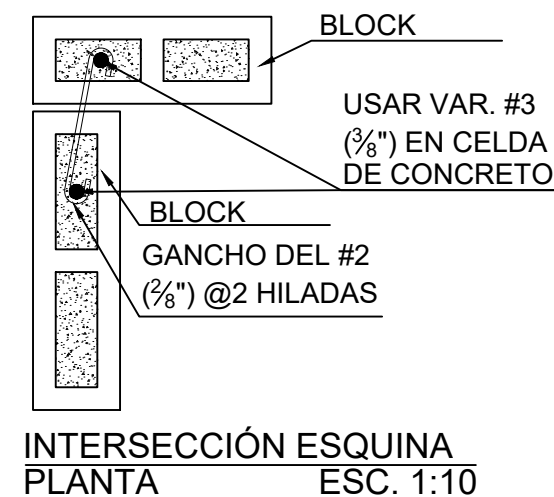

INTERSECCIÓN ESQUINA
PLANTA
ESC. 1:10

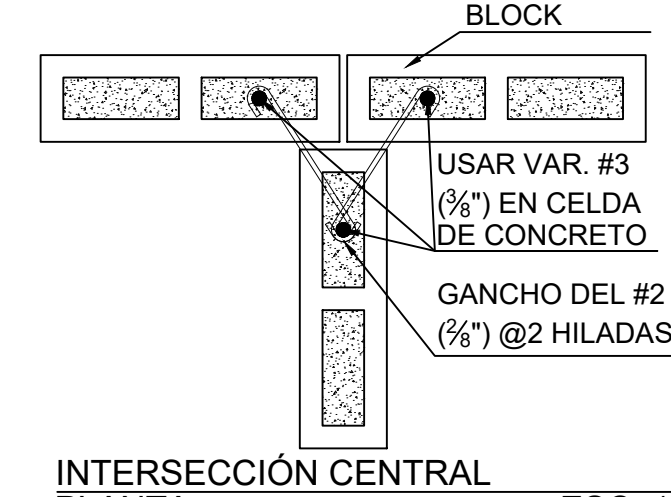

INTERSECCIÓN CENTRAL
PLANTA
ESC. 1:10

LOCALIZACIÓN

LANDER

REVISIONES

NOTAS Y ESPECIFICACIONES

RESPONSABLES

RESPONSABLE DE DISEÑO ARQUITECTÓNICO:
ARQ. FRANCISCA ELIZABETH FLORES GARCIA

PROPIETARIO:
R.L. ING. ADRIAN CASTRO GUERRERO

DIRECTOR RESPONSABLE DE OBRA:
ING. RAFAEL MONDRAGON GARCIA

PROYECTO:
CASA CLUB MDP NORTE

UBICACION:
MAR DE PLATA
HERMOSILLO, SONORA

CONTENIDO:
ESTRUCTURAL DE
CUARTO DE MÁQUINAS
Y FIRE PIT

PLANO No:
EST - 09

ARCHIVO: 03.-ESTRUCTURAL CASA CLUB MDP NORTE 260223.dwg