



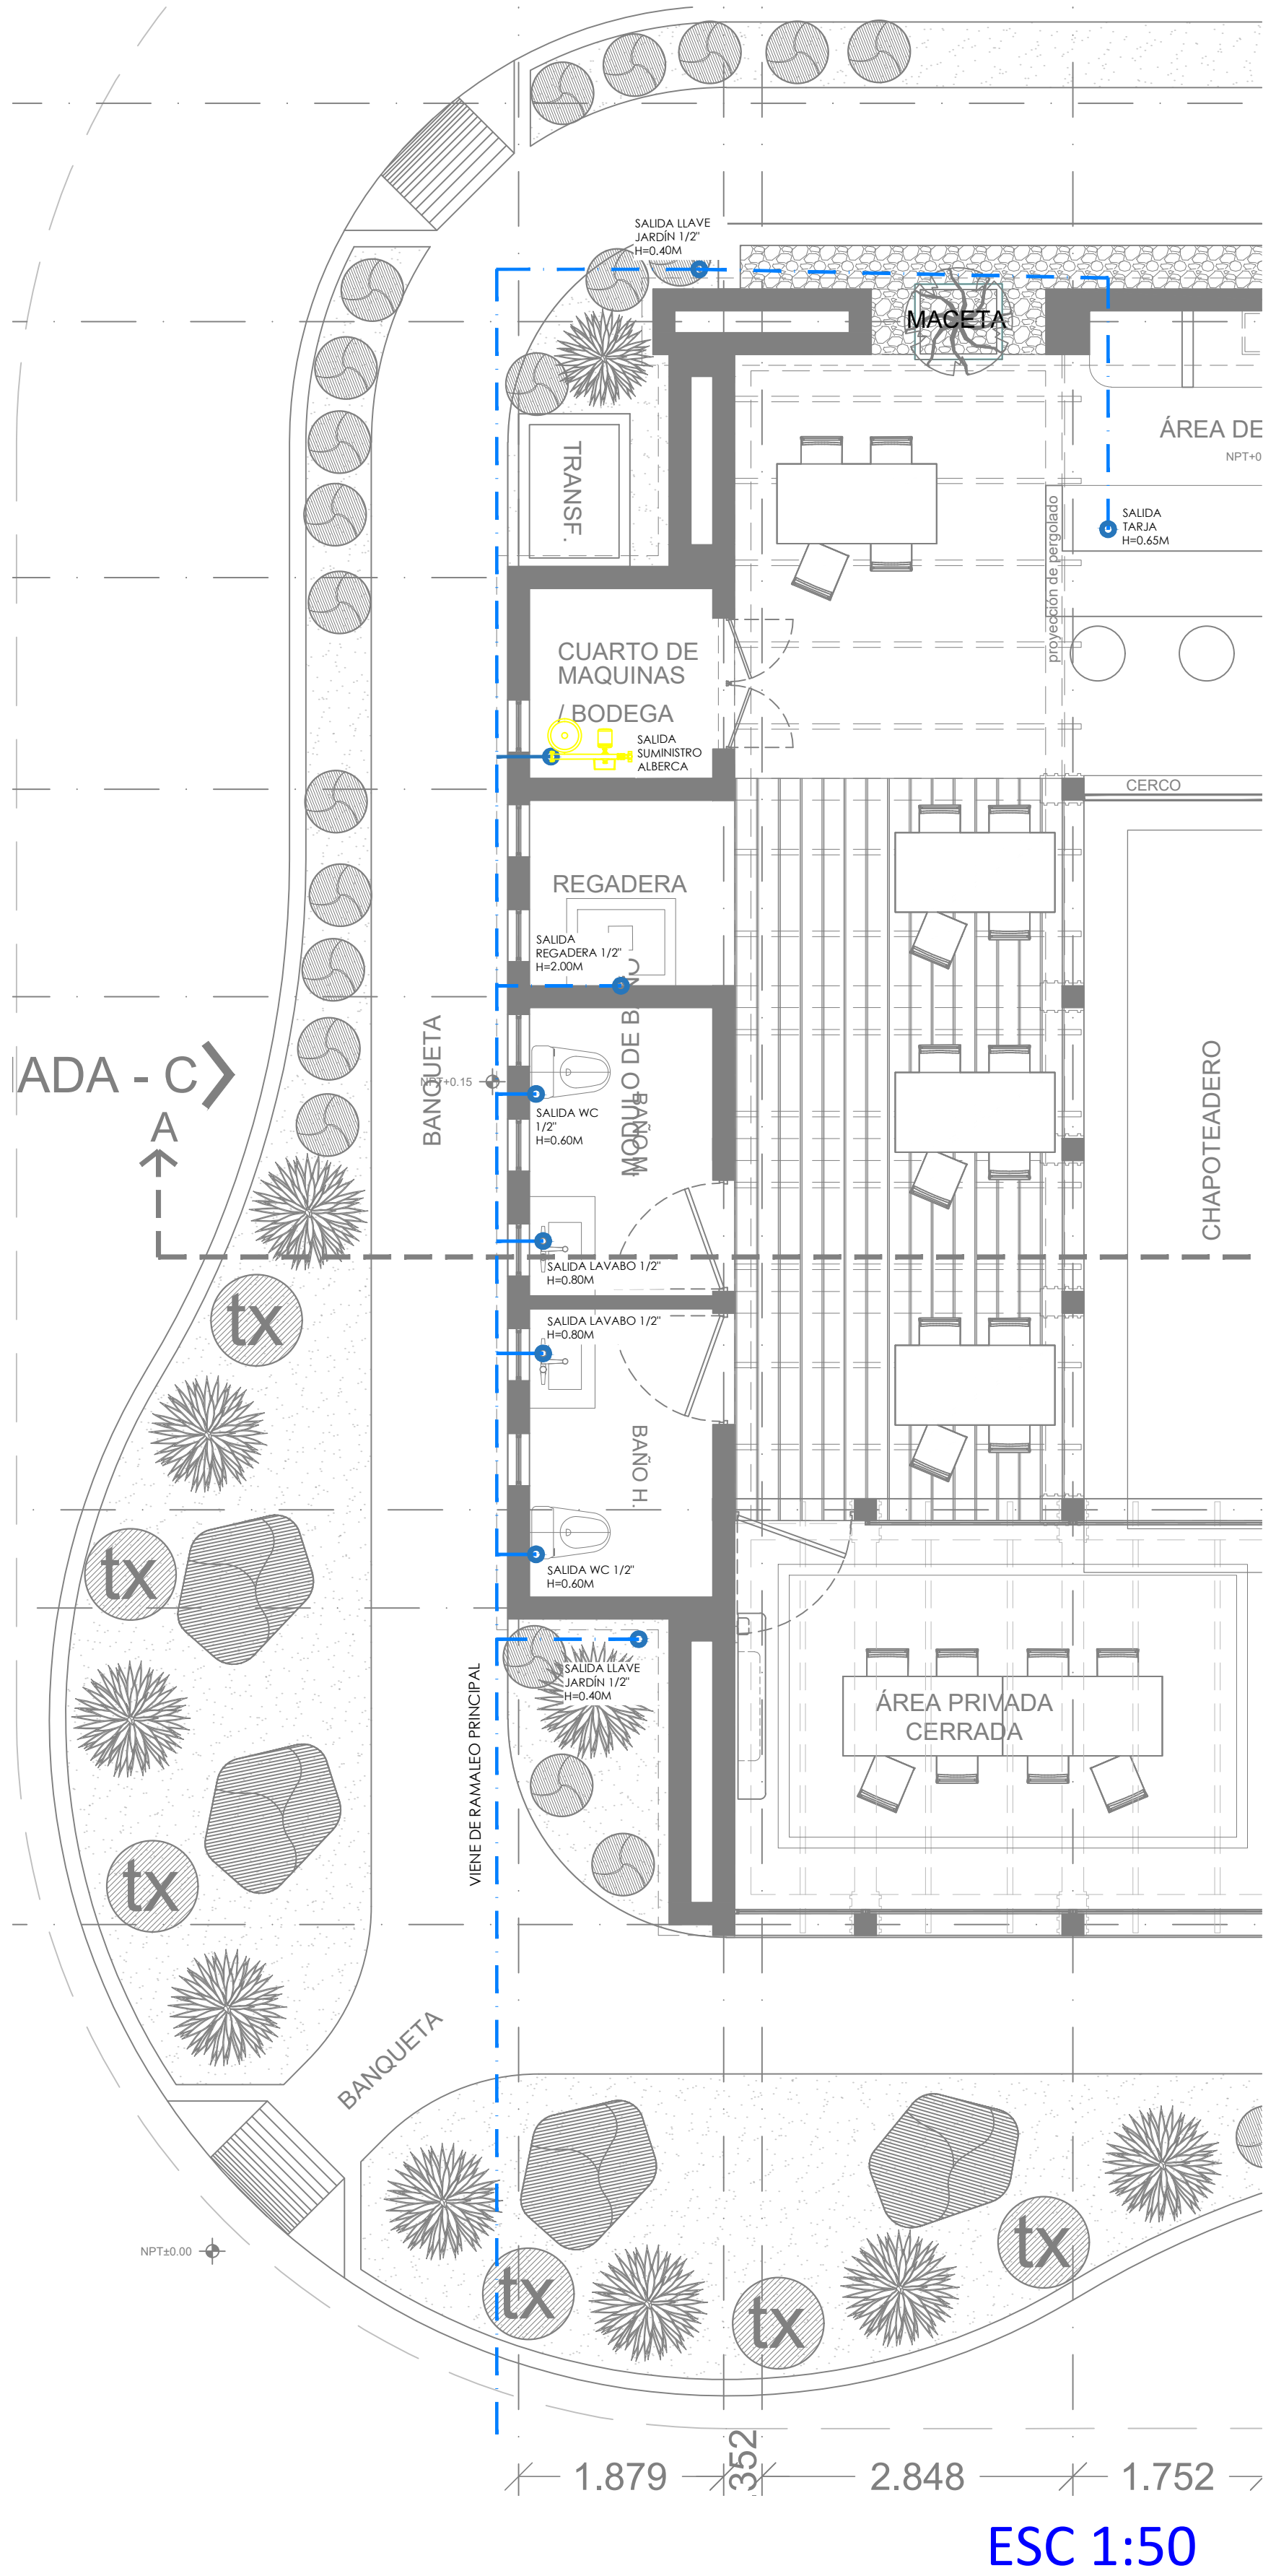

ESC 1:50

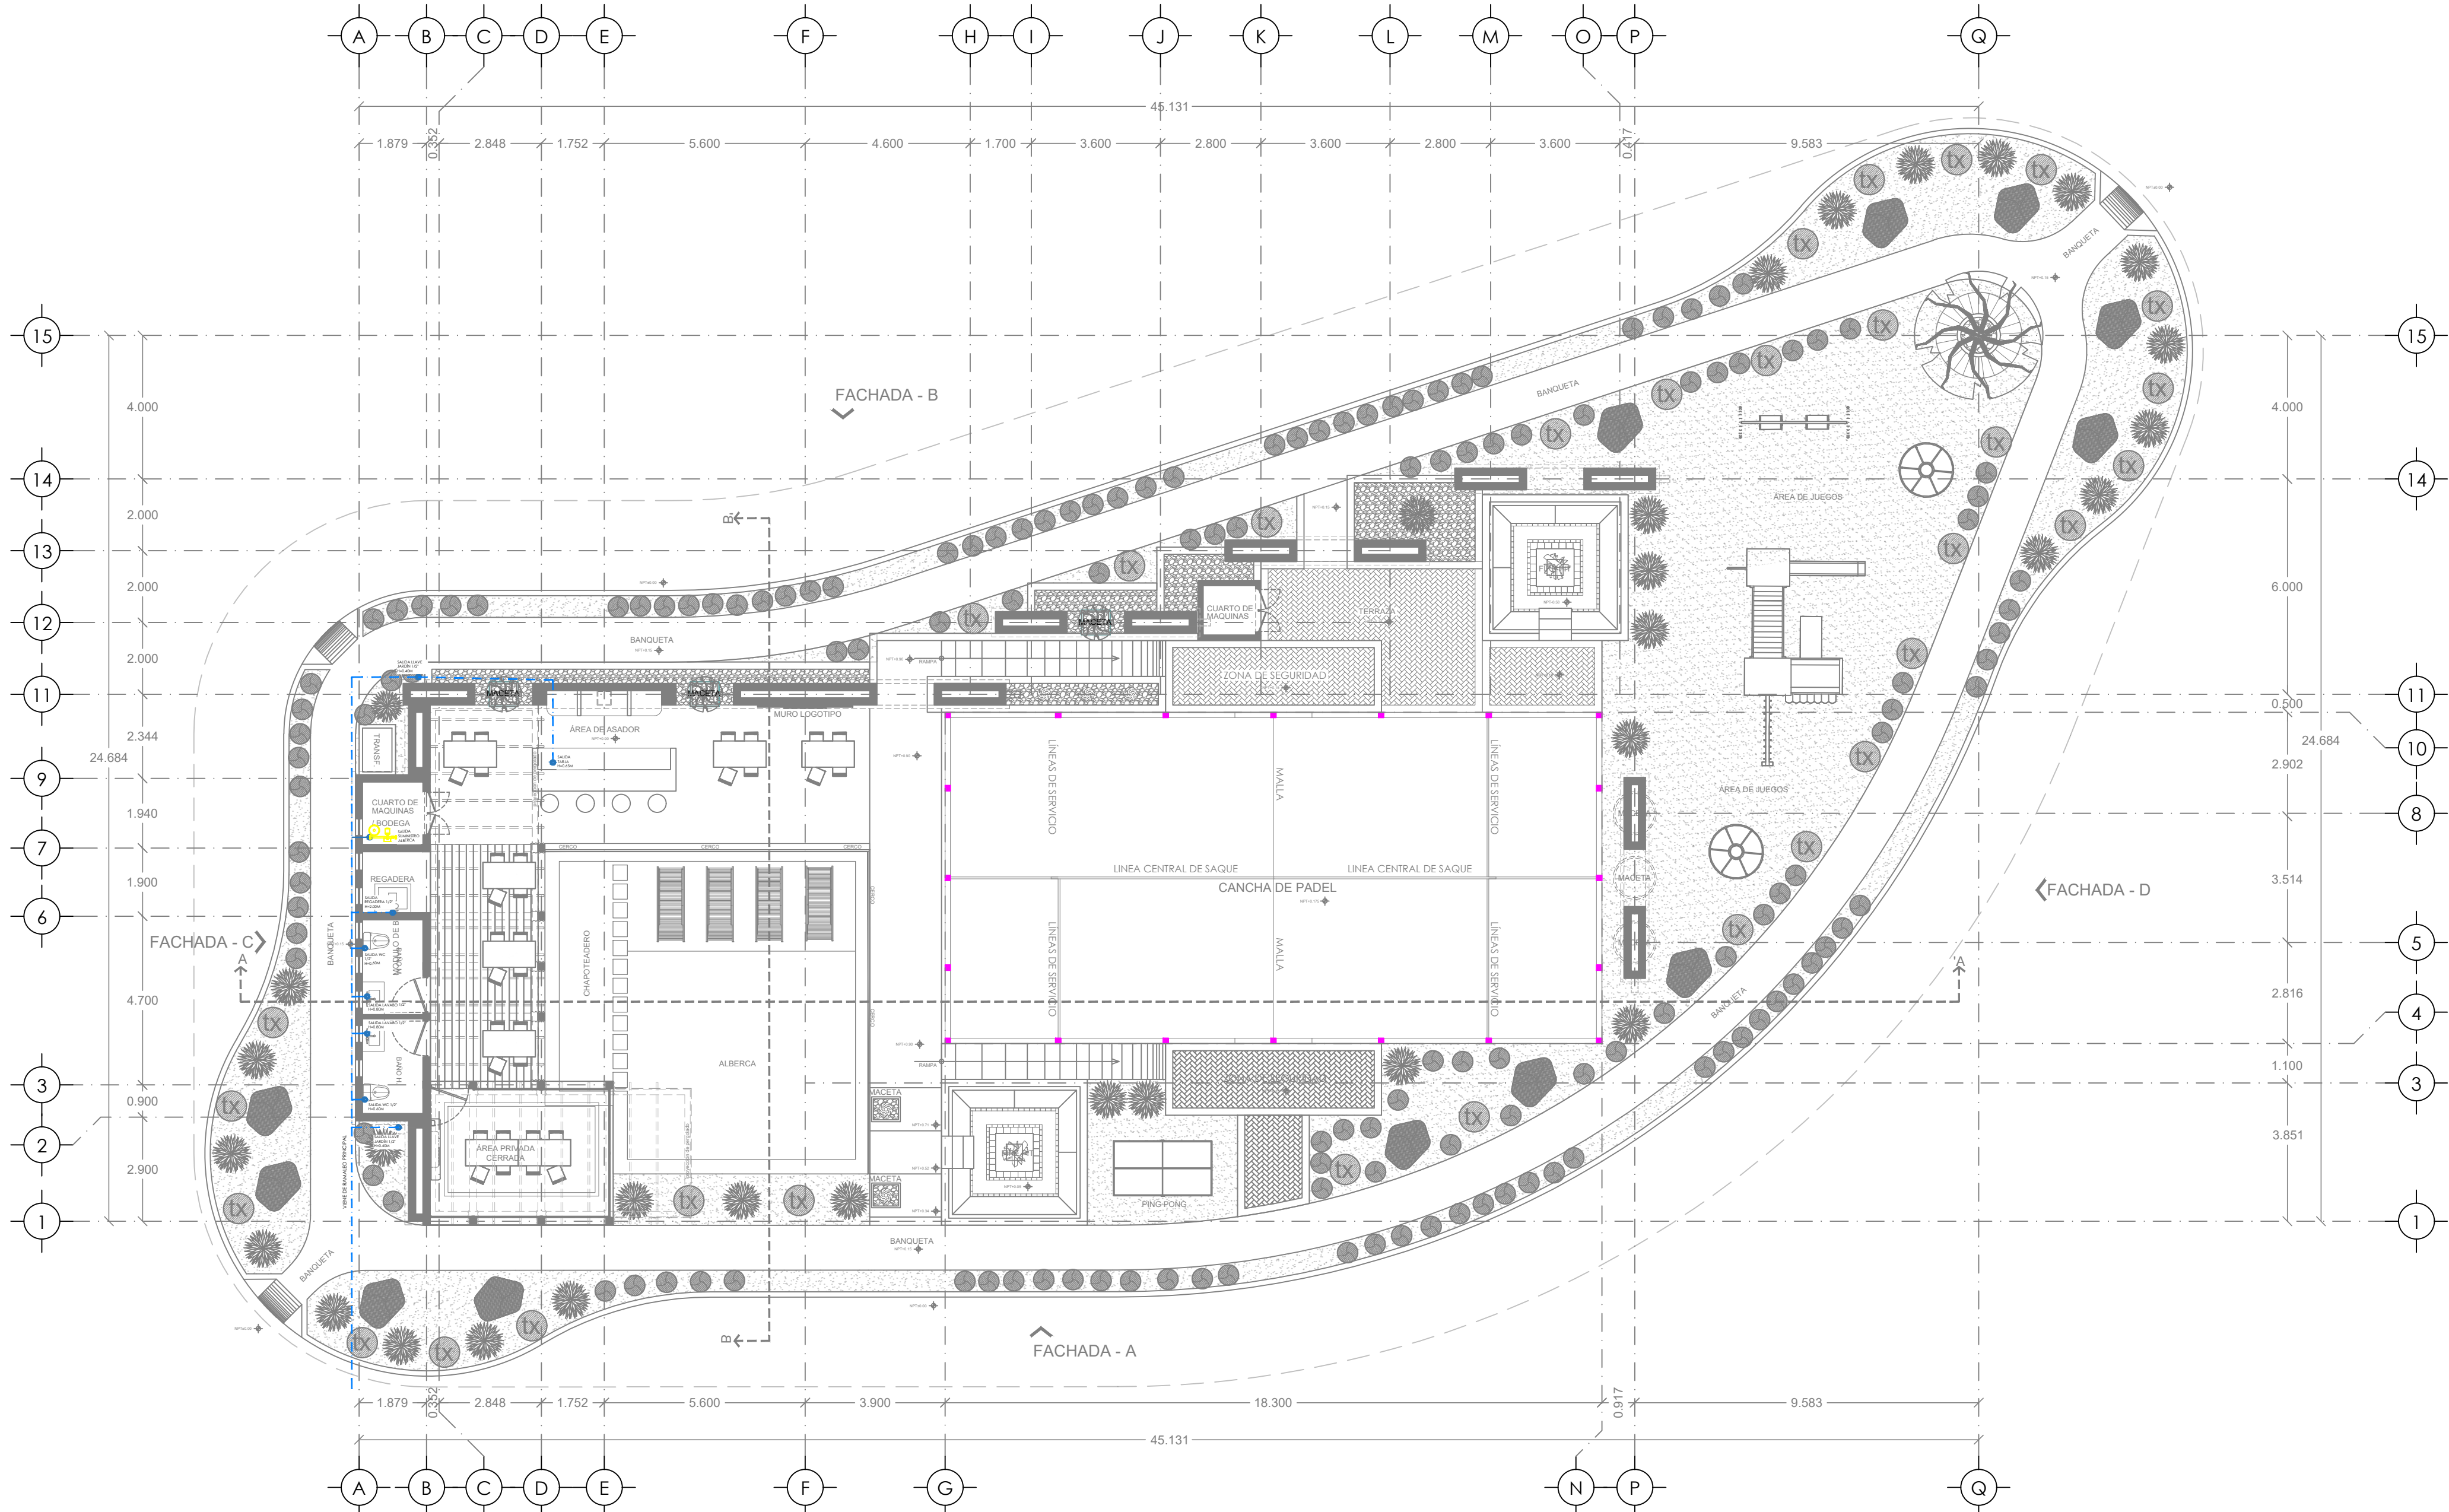


PLANTA DE INSTALACIÓN HIDRÁULICA ESC 1:125

MATERIAL DE TOMA:

- 1.- Codo 90° con rosca hembra de 1/2".
- 2.- Tubo Plus
- 3.- Llave de jardín de 1/2"
- 4.- Conector hembra de 1/2"
- 5.- Tee de 1/2"
- 6.- Conector macho de 1/2"
- 7.- Válvula tipo Check 1/2" c/ resorte
- 8.- Acople para medidor de 1/2"
- 9.- Medidor de plástico de 1/2"
- 10.- Acople para medidor de 1/2"
- 11.- Llave de globo roscable de 1/2"
- 12.- Codo 90° con rosca macho de 1/2"
- 13.- Tubo Plus
- 14.- Codo 90° con rosca hembra de 1/2"
- 15.- Válvula de banquetta Polietileno - NPT 1/2" con bota de PVC sanitario de 4" Ø, que incluye: una tapa de inserción y cople PVC sanitario 4" para proteger la llave de banquetta.
- 16.- Tubería para toma domiciliar de Agua Potable de PEAD marca Extrupak tipo II RD-9 de 1/2" que cumple con las especificaciones y métodos de prueba de la Norma NOM-001-CONAGUA-2011
- 17.- Válvula de inserción NPT (M) - Polietileno 1/2"
- 18.- Tacon doble PVC
- 19.- Adaptador

NOTA:

EL CUADRO DE TOMA SERA FABRICADO CON EL MATERIAL TUBOPLUS QUE ESTA CERTIFICADO BAJO LAS ESPECIFICACIONES DE LA NORMA MEXICANA NMX-E-226/2-1998-SCFI, EMITIDA POR LA SECRETARIA DE COMERCIO Y FOMENTO INDUSTRIAL Y LA DIRECCION GENERAL DE NORMAS. TUBO PLUS OFRECE DISTINTAS VENTAJAS ENTRE LAS CUALES ESTA CERO FUGAS, SEGURIDAD TOTAL EN LAS UNIONES, ALTA RESISTENCIA A LOS IMPACTOS, GRAN DURABILIDAD, TRANSPORTE EFICIENTE, AUSENCIA DE CORROSION, RESISTENCIA A ALTAS PRESIONES, FACILIDAD EN EL TRABAJO, MANIOBRA Y TRANSPORTE. LA TUBERIA PARA LA TOMA DOMICILIARIA SE ESPECIFICA TUBERIA EXTRUPAK, LA RESINA DE POLIETILENO, DE ACUERDO A SUS CARACTERISTICAS SE ENCUENTRA CLASIFICADA COMO TIPO III GRADO P-34 POR ASTM-1248 Y ES DESIGNADO COMO PE-3408 POR EL INSTITUTO DE TUBERIAS PLASTICAS (PTI) ASI COMO TAMBIEN POR LA NORMA OFICIAL MEXICANA NMX-E-18 COMO PE-3456. EL POLETILENO UTILIZADO PARA LA ELABORACION DE TUBERIA Y CONEXIONES EXTRU-PAK CUENTA CON UNA CELDA DE CLASIFICACION POR ASTM-D3350 CUYA CLASIFICACION SE BASA EN SUS PROPIEDADES FISICAS. DICHA CLASIFICACION ES LA SIGUIENTE: PE 345464-C.

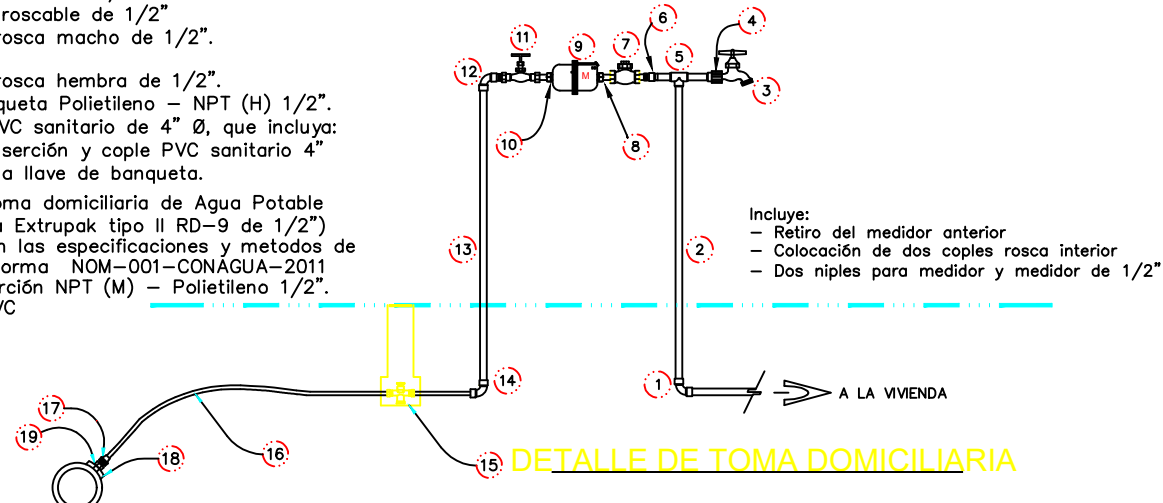


SIMBOLOGIA HIDRAULICA

	ACCESO TOMA DOMICILIARIA
	TUBERIA DE AGUA FRIA, TUBOPLUS DE Ø1/2" Y Ø3/4"
	TUBERIA DE AGUA CALIENTE TUBOPLUS DE Ø1/2" Y Ø3/4"
	LLAVE DE JARDIN
	VALVULA CHECK

ESPECIFICACIONES HIDRAULICAS

TODA LA TUBERIA SERA DE TUBOPLUS. LAS TUBERIAS POR MUROS IRAN OCULTAS EN RANURAS Y CUBIERTAS POR MORTERO ANTES DE CUBRIR LA TUBERIA SE REALIZA UNA PRUEBA DE HERMETECIDAD, CON AGUA A UNA PRESION DE 7KG/CM2 DURANTE UN PERIODO DE UNA HORA, DURANTE LA CUAL NO SE DEBEN OBSERVAR CAIDAS DE PRESION EN LA RED.

LOCALIZACIÓN

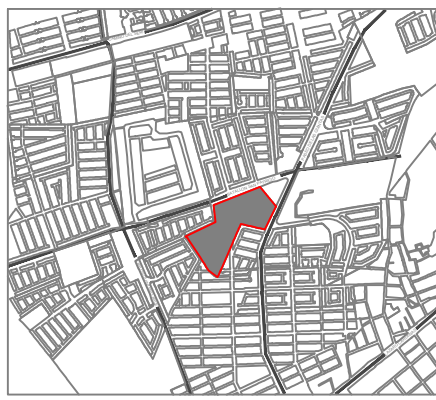

REVISIONES

NOTAS Y ESPECIFICACIONES

RESPONSABLES

RESPONSABLE DE DISEÑO DE INSTALACIONES:

PROPIETARIO:

R.L. ING. ADRIAN CASTRO GUERRERO

DIRECTOR RESPONSABLE DE OBRA:

ING. RAFAEL MONDRAGON GARCIA

PROPIETARIO:

DESARROLLOS RESIDENCIALES LANDER S. A. DE C. V.

Bulevard Naranjal #1116 - Jalisco y Subragio
CD. OBRERON, SONORA
TEL. 413 92 79 413 92 80 413 92 83

ESCALA:

INDICADA

VERSION: 2.0

DESENHO: ARQ. GUADALUPE VAZQUEZ

FECHA: NOV/2025

REVISOR: ARQ. ELIZABETH FLORES

ACOTACIONES: METROS

PROYECTO:

CASA CLUB

UBICACION:

MAR DE PLATA HERMOSILLO, SONORA

CONTENIDO:

INSTALACIÓN HIDRÁULICA

PLANO No:

IH-01

ARCHIVO: 04INST. HIDROSANITARIA-CC-MOPL I V2.019