




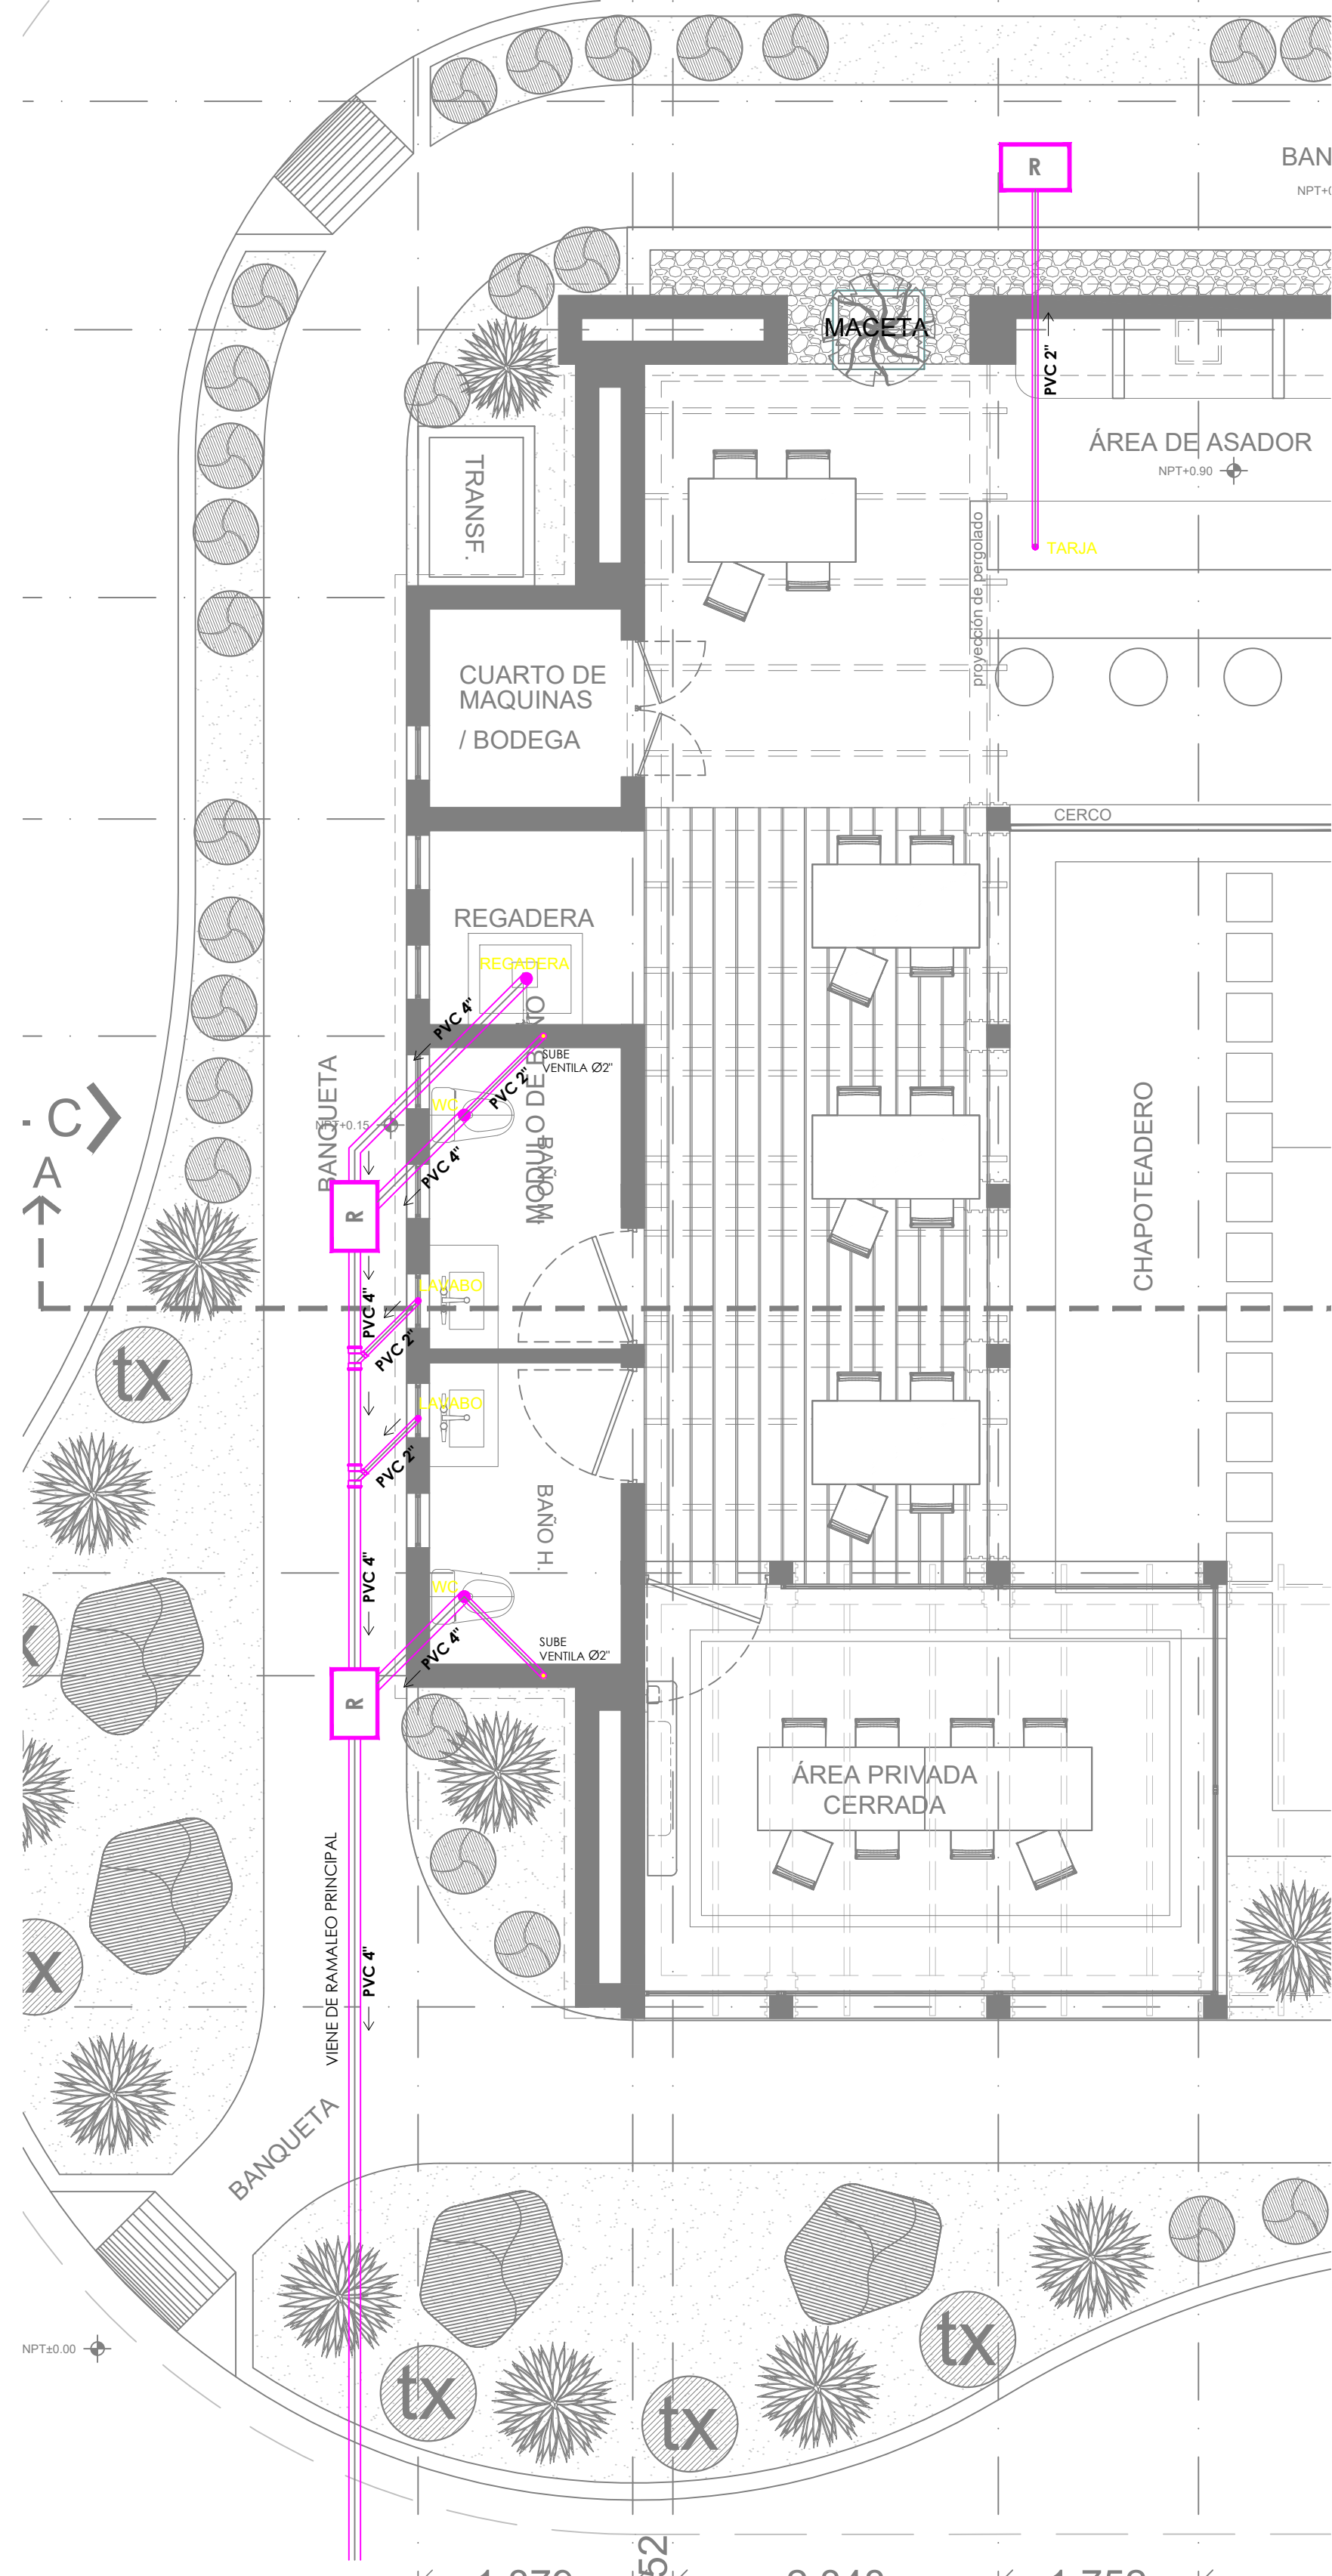


ESC 1:50

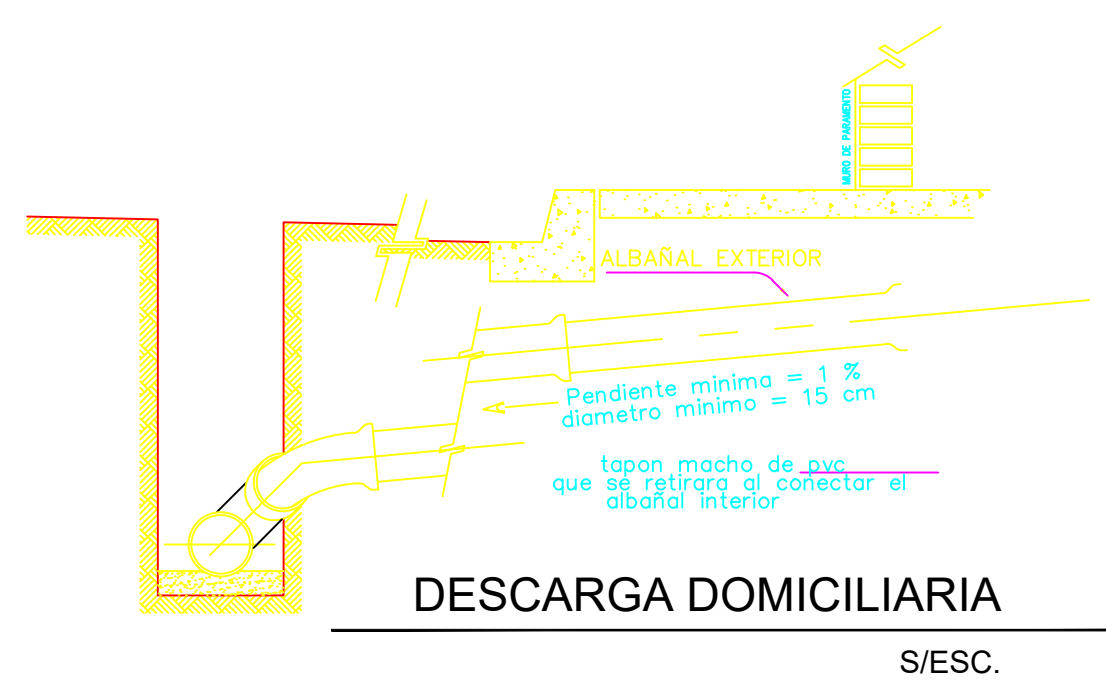

DESCARGA DOMICILIARIA
S/ESC.

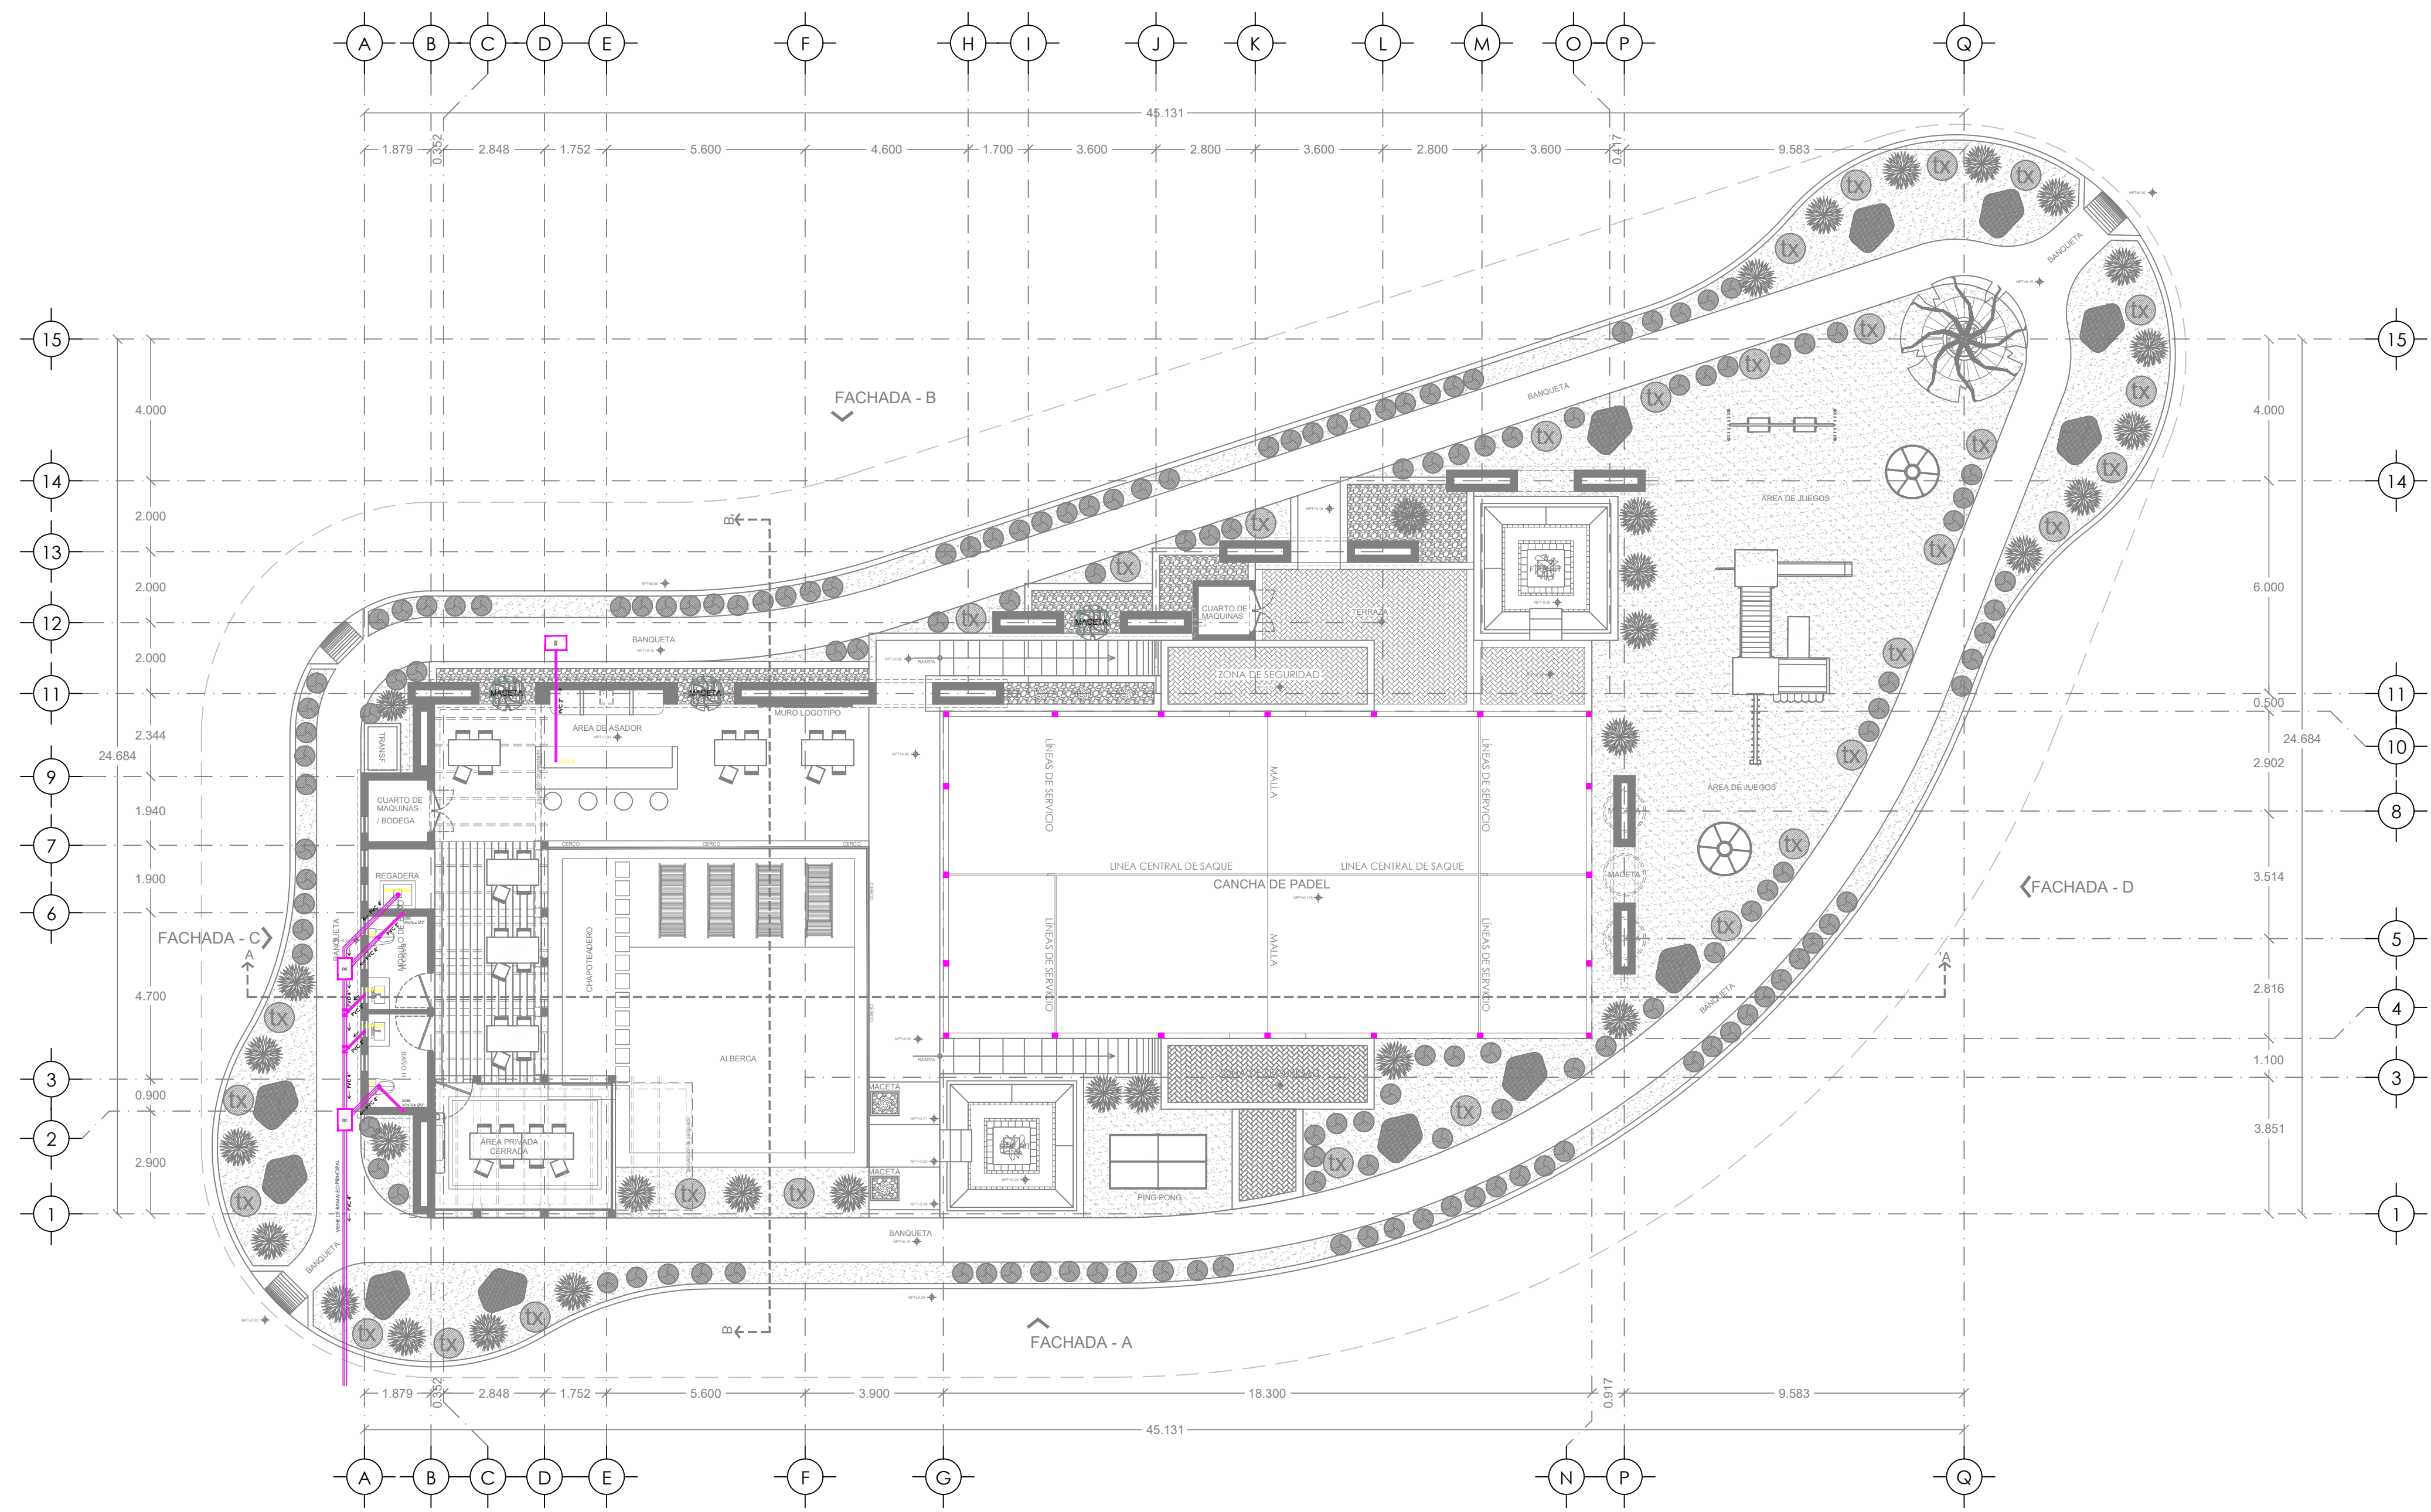

PLANTA DE INSTALACIÓN SANITARIA ESC 1:125

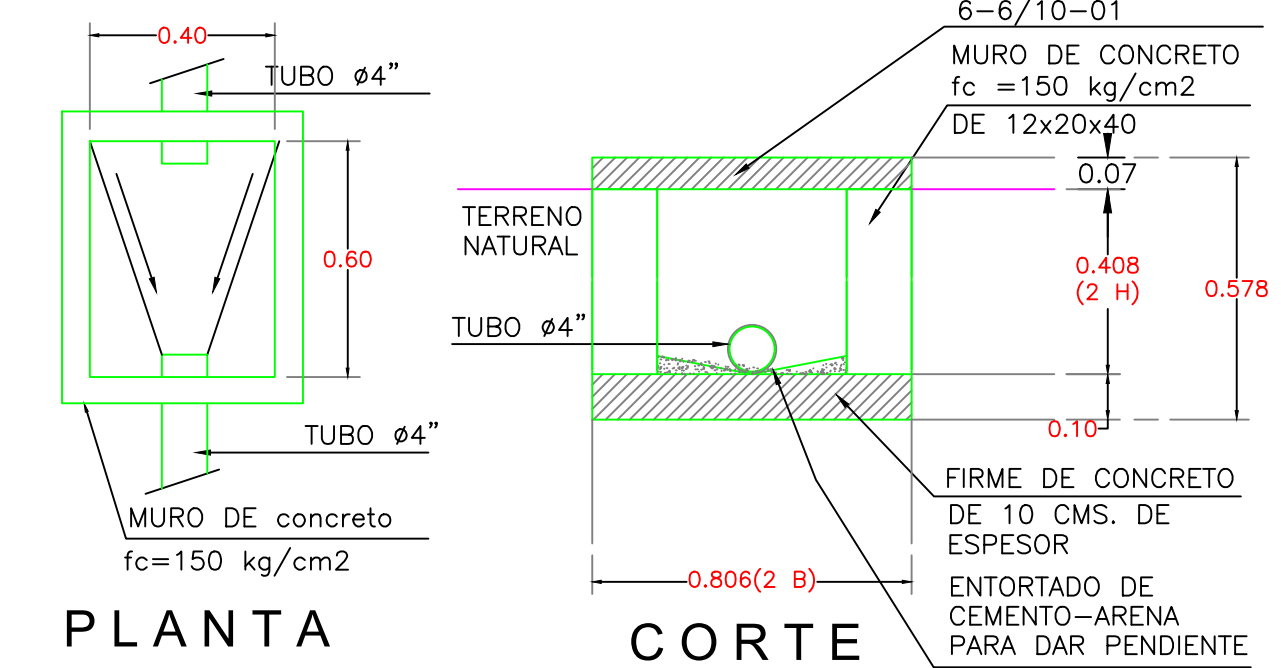

DETALLE DE REGISTRO SANITARIO
S/ESC.

ESPECIFICACIONES SANITARIAS

LA TUBERIA Y ACCESORIOS UTILIZADOS PARA LAS INSTALACIONES SANITARIAS SERAN DE PVC DE 2" Y 4".

LA TUBERIA SALIENTE DEL LAVADERO, DUCHA Y W.C. SERA DE DIAMETRO DE 2" Y SE UNIRAN A LA TUBERIA DE DESCARGA DE 4" POR MEDIO DE UN ACCESORIO DE REDUCCION DE 4" A 2".

TODA LA RED DESCARGA EN UN REGISTRO SANITARIO INTERIOR A TRAVES DE LA TUBERIA DE PVC DE 4", GRACIAS A UNA PENDIENTE MINIMA DEL 2%.

LAS AGUAS NEGRAS CAPTADAS POR EL REGISTRO SANITARIO INTERIOR CONTINUAN SU DESCARGA HACIA LA RED MUNICIPAL A TRAVES DE TUBERIA DE PVC DE 4" CON PENDIENTE MINIMA DE 2%.

SE DEJARA PREPARACION PARA MINISPLIT, ESTA SERA DE TUBERIA DE PVC DE Ø3/4" PARA LA DESCARGA, Y SE CONECTARAN AL REGISTRO SANITARIO.

LOCALIZACIÓN

LANDER

REVISIONES

NOTAS Y ESPECIFICACIONES

RESPONSABLES

RESPONSABLE DE DISEÑO DE INSTALACIONES:
PROPIETARIO:
R.L. ING. ADRIAN CASTRO GUERRERO
DIRECTOR RESPONSABLE DE OBRA:
ING. RAFAEL MONDRAGON GARCIA

PROPIETARIO:
DESARROLLOS RESIDENCIALES
LANDER S. A. DE C. V.
Boulevard Nariari #1116 - Jalisco y Subrango
CD. OBRERON, SONORA.
TEL. 413 92 79 413 92 80 413 92 83

ESCALA:
INDICADA
VERSION: 2.0
DIBUJO:
ARQ. GUADALUPE VAZQUEZ
FECHA: NOV/2025
REVISOR:
ARQ. ELIZABETH FLORES
ACOTACIONES:
METROS

PROYECTO:
CASA CLUB

UBICACION:
MAR DE PLATA
HERMOSILLO, SONORA

CONTENIDO:
INSTALACIÓN
SANITARIA

PLANO No:
IS-01

ARCHIVO: 04INST. HIDROSANITARIA-CC-MOPL-1-1-2025