




FACHADA - A

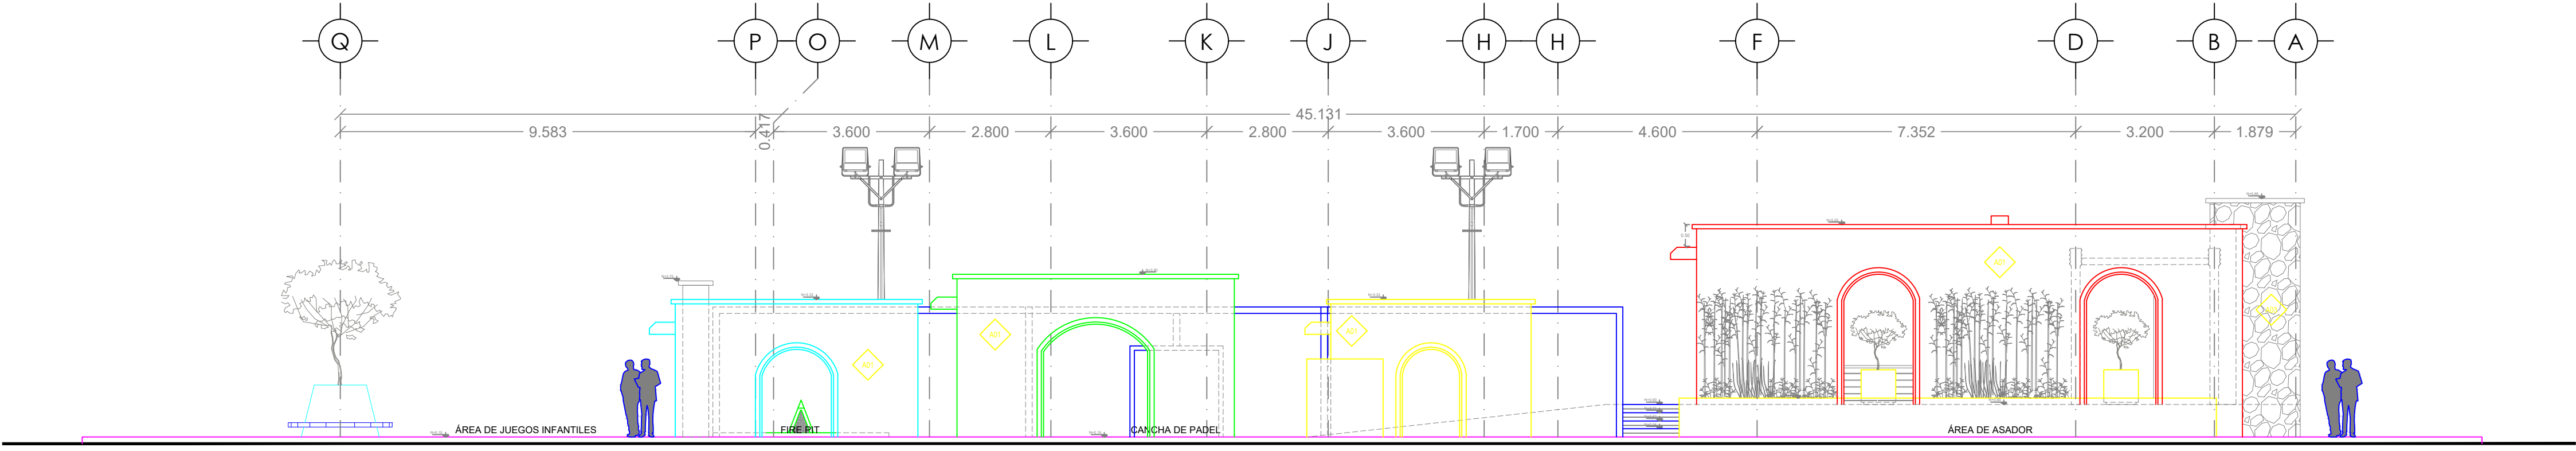

FACHADA - B

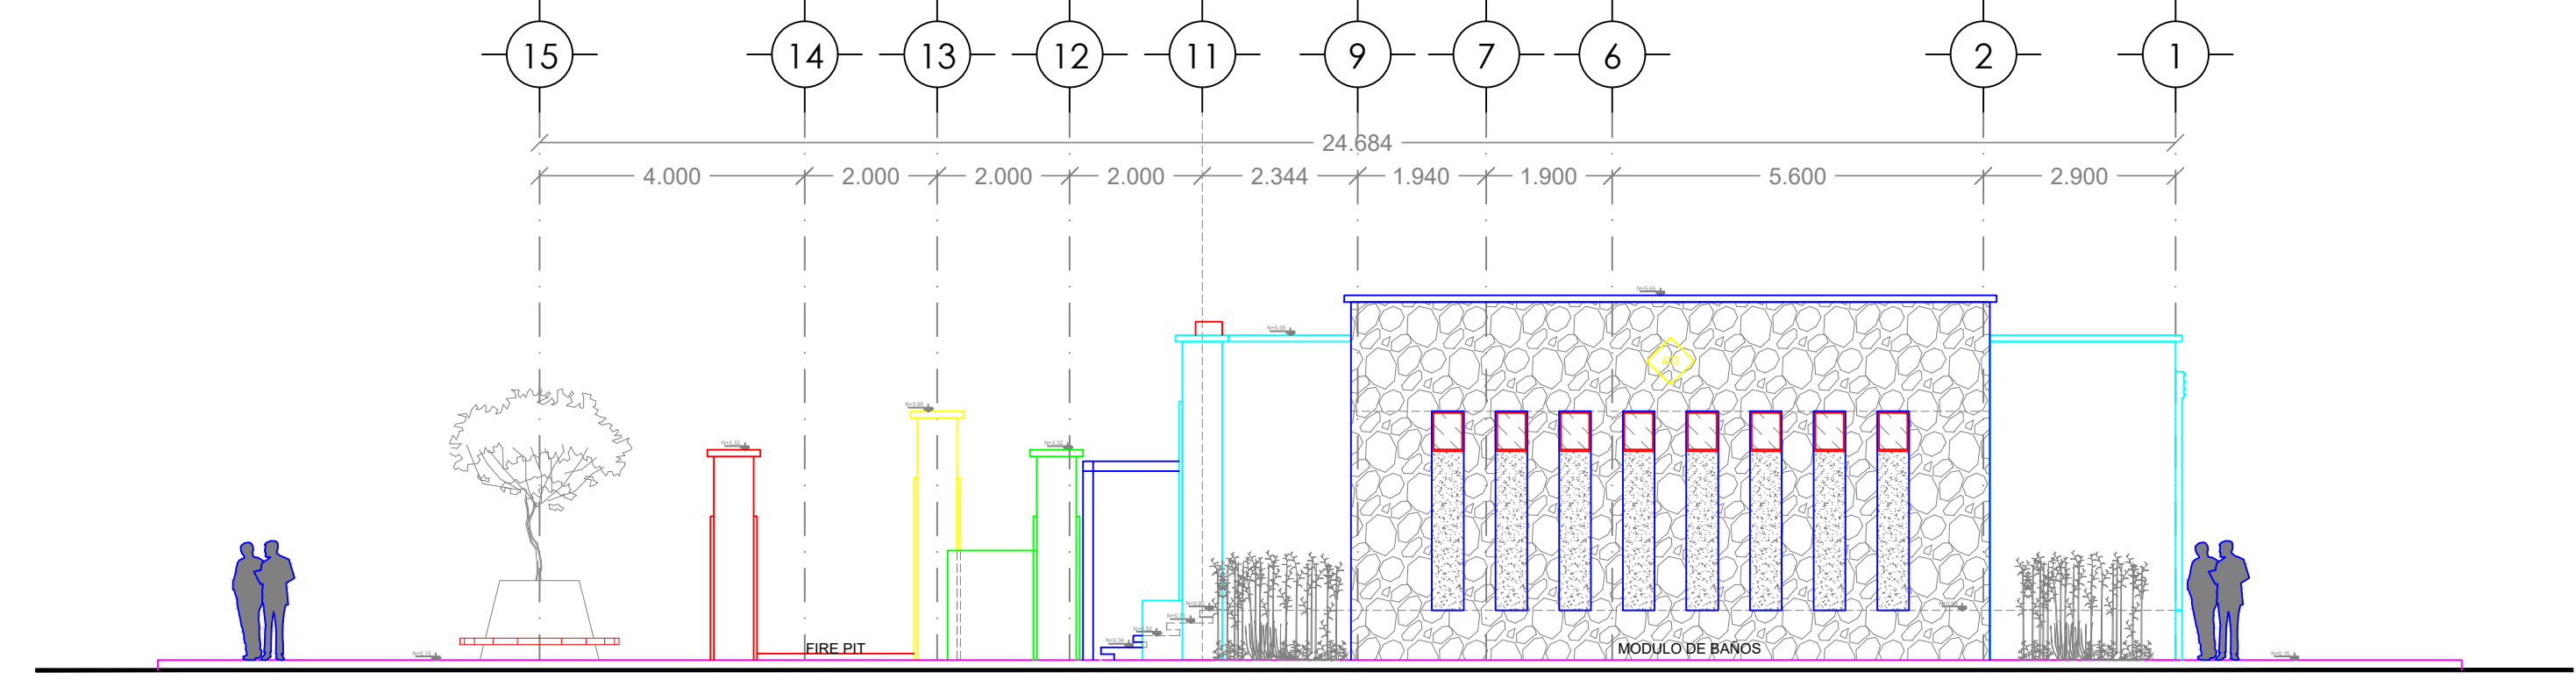

FACHADA - C

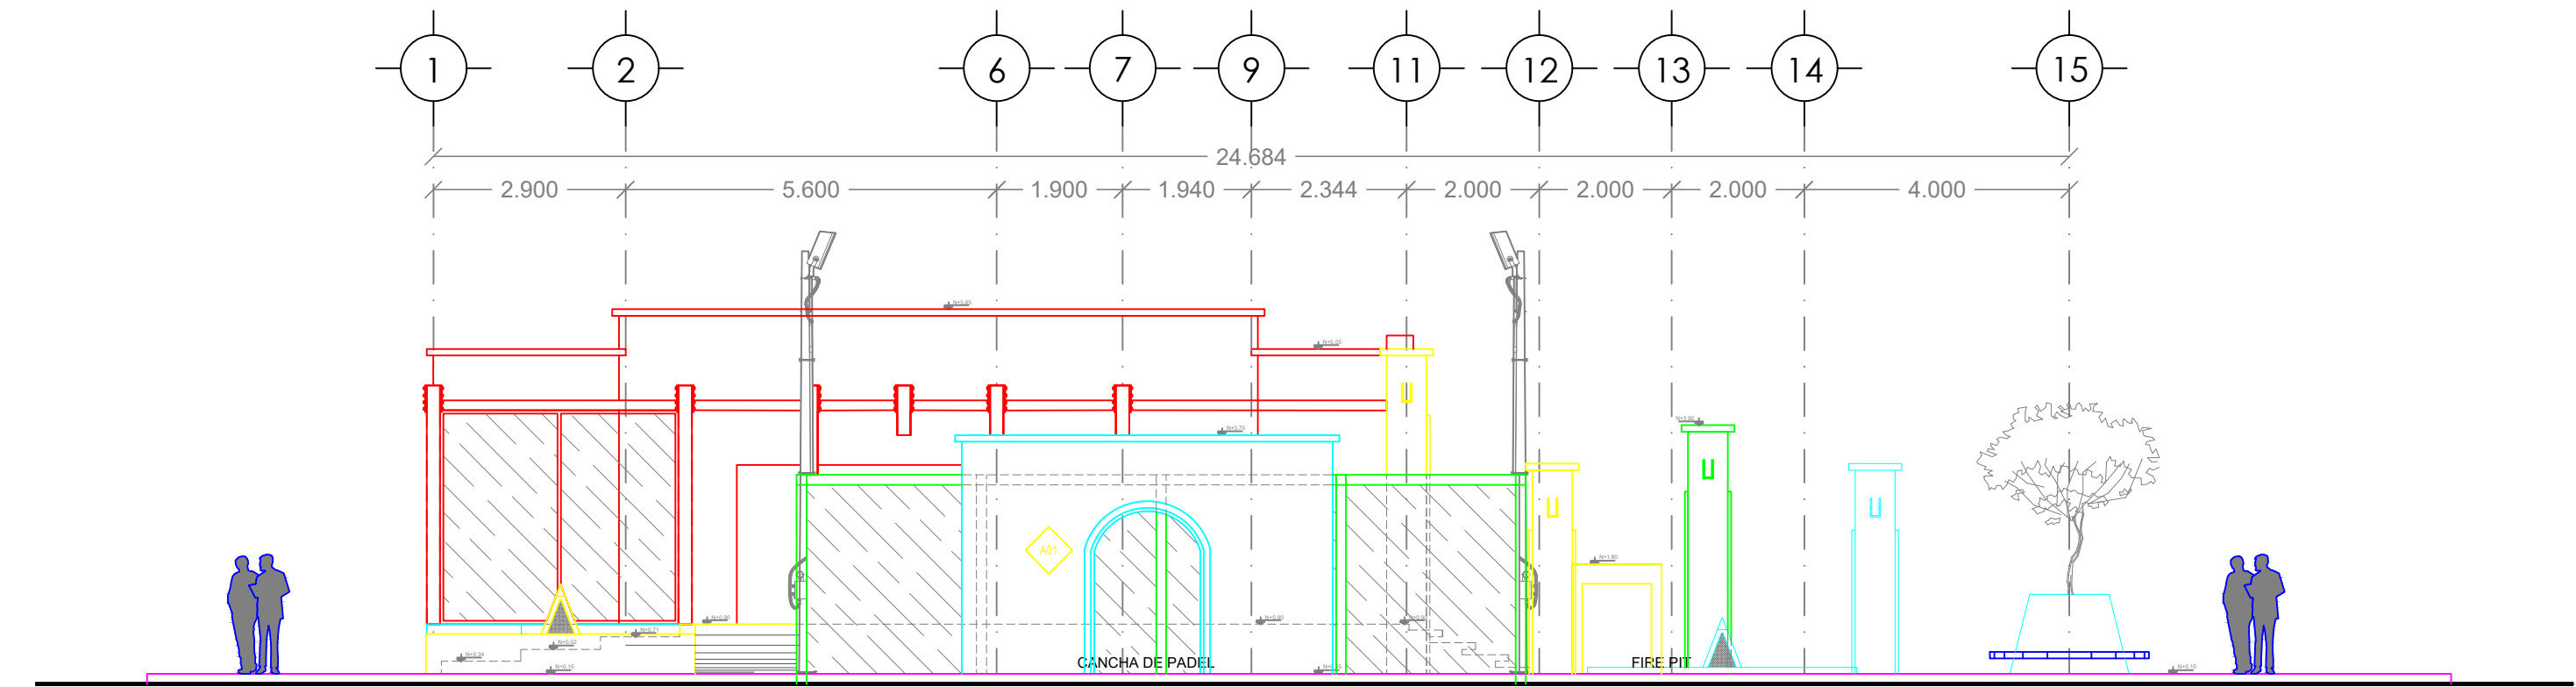

FACHADA - D

LOCALIZACIÓN

REVISIONES

NOTAS Y ESPECIFICACIONES

RESPONSABLES

RESPONSABLE DE DISEÑO DE INSTALACIONES:

PROPIETARIO:

R.L. ING. ADRIAN CASTRO GUERRERO

DIRECTOR RESPONSABLE DE OBRA:

ING. RAFAEL MONDRAGON GARCIA

PROPIETARIO:

DESARROLLOS RESIDENCIALES
LANDER S. A. DE C. V.

Bulevar Nariari #1116 - Jalisco y Subragio
CDJ OBREGÓN, SONORA
TEL. 413 52 79 413 52 80 413 52 83

ESCALA:

1:100

VERSIÓN:

3.0

DIBUJO:

ARQ. GUADALUPE VAZQUEZ

FECHA:

JUN/2026

REVISÓ:

ARQ. ELIZABETH FLORES

ACOTACIONES:

METROS

PROYECTO:

CASA CLUB

UBICACIÓN:

MAR DE PLATA
HERMOSILLO, SONORA

CONTENIDO:

ACABADOS EN
FACHADA

PLANO No:

ACA-02

ARCHIVO: 05 PLANO DE ACABADOS-CC-MDPL II V.03.00

ESC 1:100